

Mục đích phát hành/Release status:
Thiết kế sơ/Preliminary:
Bản vẽ trình duyệt/For approval:
Bản vẽ tham khảo/For reference:
Bản vẽ thi công/For construction: <input checked="" type="checkbox"/>
Bản vẽ hiệu chỉnh/Revising:
Bản vẽ hoàn công/As built:

DANH MỤC BẢN VẼ - DRAWING LIST			
SỐ HIỆU - NO.	TÊN BẢN VẼ	HỆU CHỈNH - REVISION	NGÀY PHÁT HÀNH - ISSUED DATE
000	BÌA	0	04/2025
001	DANH MỤC BẢN VẼ	0	04/2025
E1-101	SƠ ĐỒ NGUYÊN LÝ-HỆ THỐNG CẤP ĐIỆN	0	04/2025
E1-102	SƠ ĐỒ NGUYÊN LÝ-TỦ ĐIỆN MDB-1F	0	04/2025
E1-103	SƠ ĐỒ NGUYÊN LÝ-TỦ ĐIỆN MDB-MF	0	04/2025
E1-104	SƠ ĐỒ NGUYÊN LÝ-TỦ ĐIỆN MDB-(2-6)F	0	04/2025
E1-105	SƠ ĐỒ NGUYÊN LÝ-TỦ ĐIỆN MDB-TF	0	04/2025
E1-201	HỆ THỐNG CẤP NGUỒN, Ô CĂM-TẦNG 1	0	04/2025
E1-202	HỆ THỐNG CẤP NGUỒN, Ô CĂM-TẦNG LƯỜNG	0	04/2025
E1-203	HỆ THỐNG CẤP NGUỒN, Ô CĂM-TẦNG 2-6	0	04/2025
E1-204	HỆ THỐNG CẤP NGUỒN, Ô CĂM-TẦNG SÂN THƯỢNG	0	04/2025
E2-201	HỆ THỐNG CHIẾU SÁNG-TẦNG 1	0	04/2025
E2-202	HỆ THỐNG CHIẾU SÁNG-TẦNG LƯỜNG	0	04/2025
E2-203	HỆ THỐNG CHIẾU SÁNG-TẦNG 2-6	0	04/2025
E2-204	HỆ THỐNG CHIẾU SÁNG-TẦNG SÂN THƯỢNG	0	04/2025
E3-201	HỆ THỐNG MẠNG, CAMERA-TẦNG 1	0	04/2025
E3-202	HỆ THỐNG MẠNG, CAMERA-TẦNG LƯỜNG	0	04/2025
E3-203	HỆ THỐNG MẠNG, CAMERA-TẦNG 2-6	0	04/2025
E3-204	HỆ THỐNG MẠNG, CAMERA-TẦNG SÂN THƯỢNG	0	04/2025
E4-401	CHI TIẾP LẮP ĐẶT ĐIỆN 1	0	04/2025
E4-402	CHI TIẾP LẮP ĐẶT ĐIỆN 2	0	04/2025
M-201	HỆ THỐNG DHKK-TẦNG 1	0	04/2025
M-202	HỆ THỐNG DHKK-TẦNG LƯỜNG	0	04/2025
M-203	HỆ THỐNG DHKK-TẦNG 2-6	0	04/2025
M-204	HỆ THỐNG DHKK-TẦNG SÂN THƯỢNG	0	04/2025
M-401	CHI TIẾP LẮP ĐẶT DHKK 1	0	04/2025
M-402	CHI TIẾP LẮP ĐẶT DHKK 2	0	04/2025
P1-101	SƠ ĐỒ NGUYÊN LÝ-HỆ THỐNG CẤP NƯỚC	0	04/2025
P1-201	HỆ THỐNG CẤP NƯỚC-TẦNG 1	0	04/2025
P1-202	HỆ THỐNG CẤP NƯỚC-TẦNG LƯỜNG	0	04/2025
P1-203	HỆ THỐNG CẤP NƯỚC-TẦNG 2-4	0	04/2025
P1-204	HỆ THỐNG CẤP NƯỚC-TẦNG 5, 6	0	04/2025
P1-205	HỆ THỐNG CẤP NƯỚC-TẦNG SÂN THƯỢNG	0	04/2025
P1-206	HỆ THỐNG CẤP NƯỚC-MÁI	0	04/2025
P2-101	SƠ ĐỒ NGUYÊN LÝ-HỆ THỐNG CẤP NƯỚC	0	04/2025
P2-201	HỆ THỐNG THOÁT NƯỚC-TẦNG 1	0	04/2025
P2-202	HỆ THỐNG THOÁT NƯỚC-TẦNG LƯỜNG	0	04/2025
P2-203	HỆ THỐNG THOÁT NƯỚC-TẦNG 2	0	04/2025
P2-204	HỆ THỐNG THOÁT NƯỚC-TẦNG 3-6	0	04/2025
P2-205	HỆ THỐNG THOÁT NƯỚC-SÂN THƯỢNG	0	04/2025
P2-206	HỆ THỐNG THOÁT NƯỚC-MÁI	0	04/2025
P3-401	CHI TIẾP LẮP ĐẶT CTN 1	0	04/2025
P3-402	CHI TIẾP LẮP ĐẶT CTN 2	0	04/2025

Đơn vị thiết kế - Thi công:
**CÔNG TY
CỔ PHẦN KIẾN TRÚC
- XÂY DỰNG ĐỨC AN**

Địa chỉ:
60/10/2 Lâm Văn Bền - Phường
Tân Kiêng - Quận 7- TP.HCM

Công trình/ Project:
BINH DUONG HOTEL

Hạng mục/ Item:
**THIẾT KẾ
ĐIỆN NƯỚC**

Bản vẽ/ Drawing name:

DANH MỤC BẢN VẼ


Chủ trì thiết kế/ Project manager:


KTS. Vũ Minh Lâm

Thiết kế/ Desginer:


KTS. Vũ Minh Lâm

Tỉ lệ/ Scale: 1/100 Ngày: 04/2025
Số bản vẽ: 001 No:

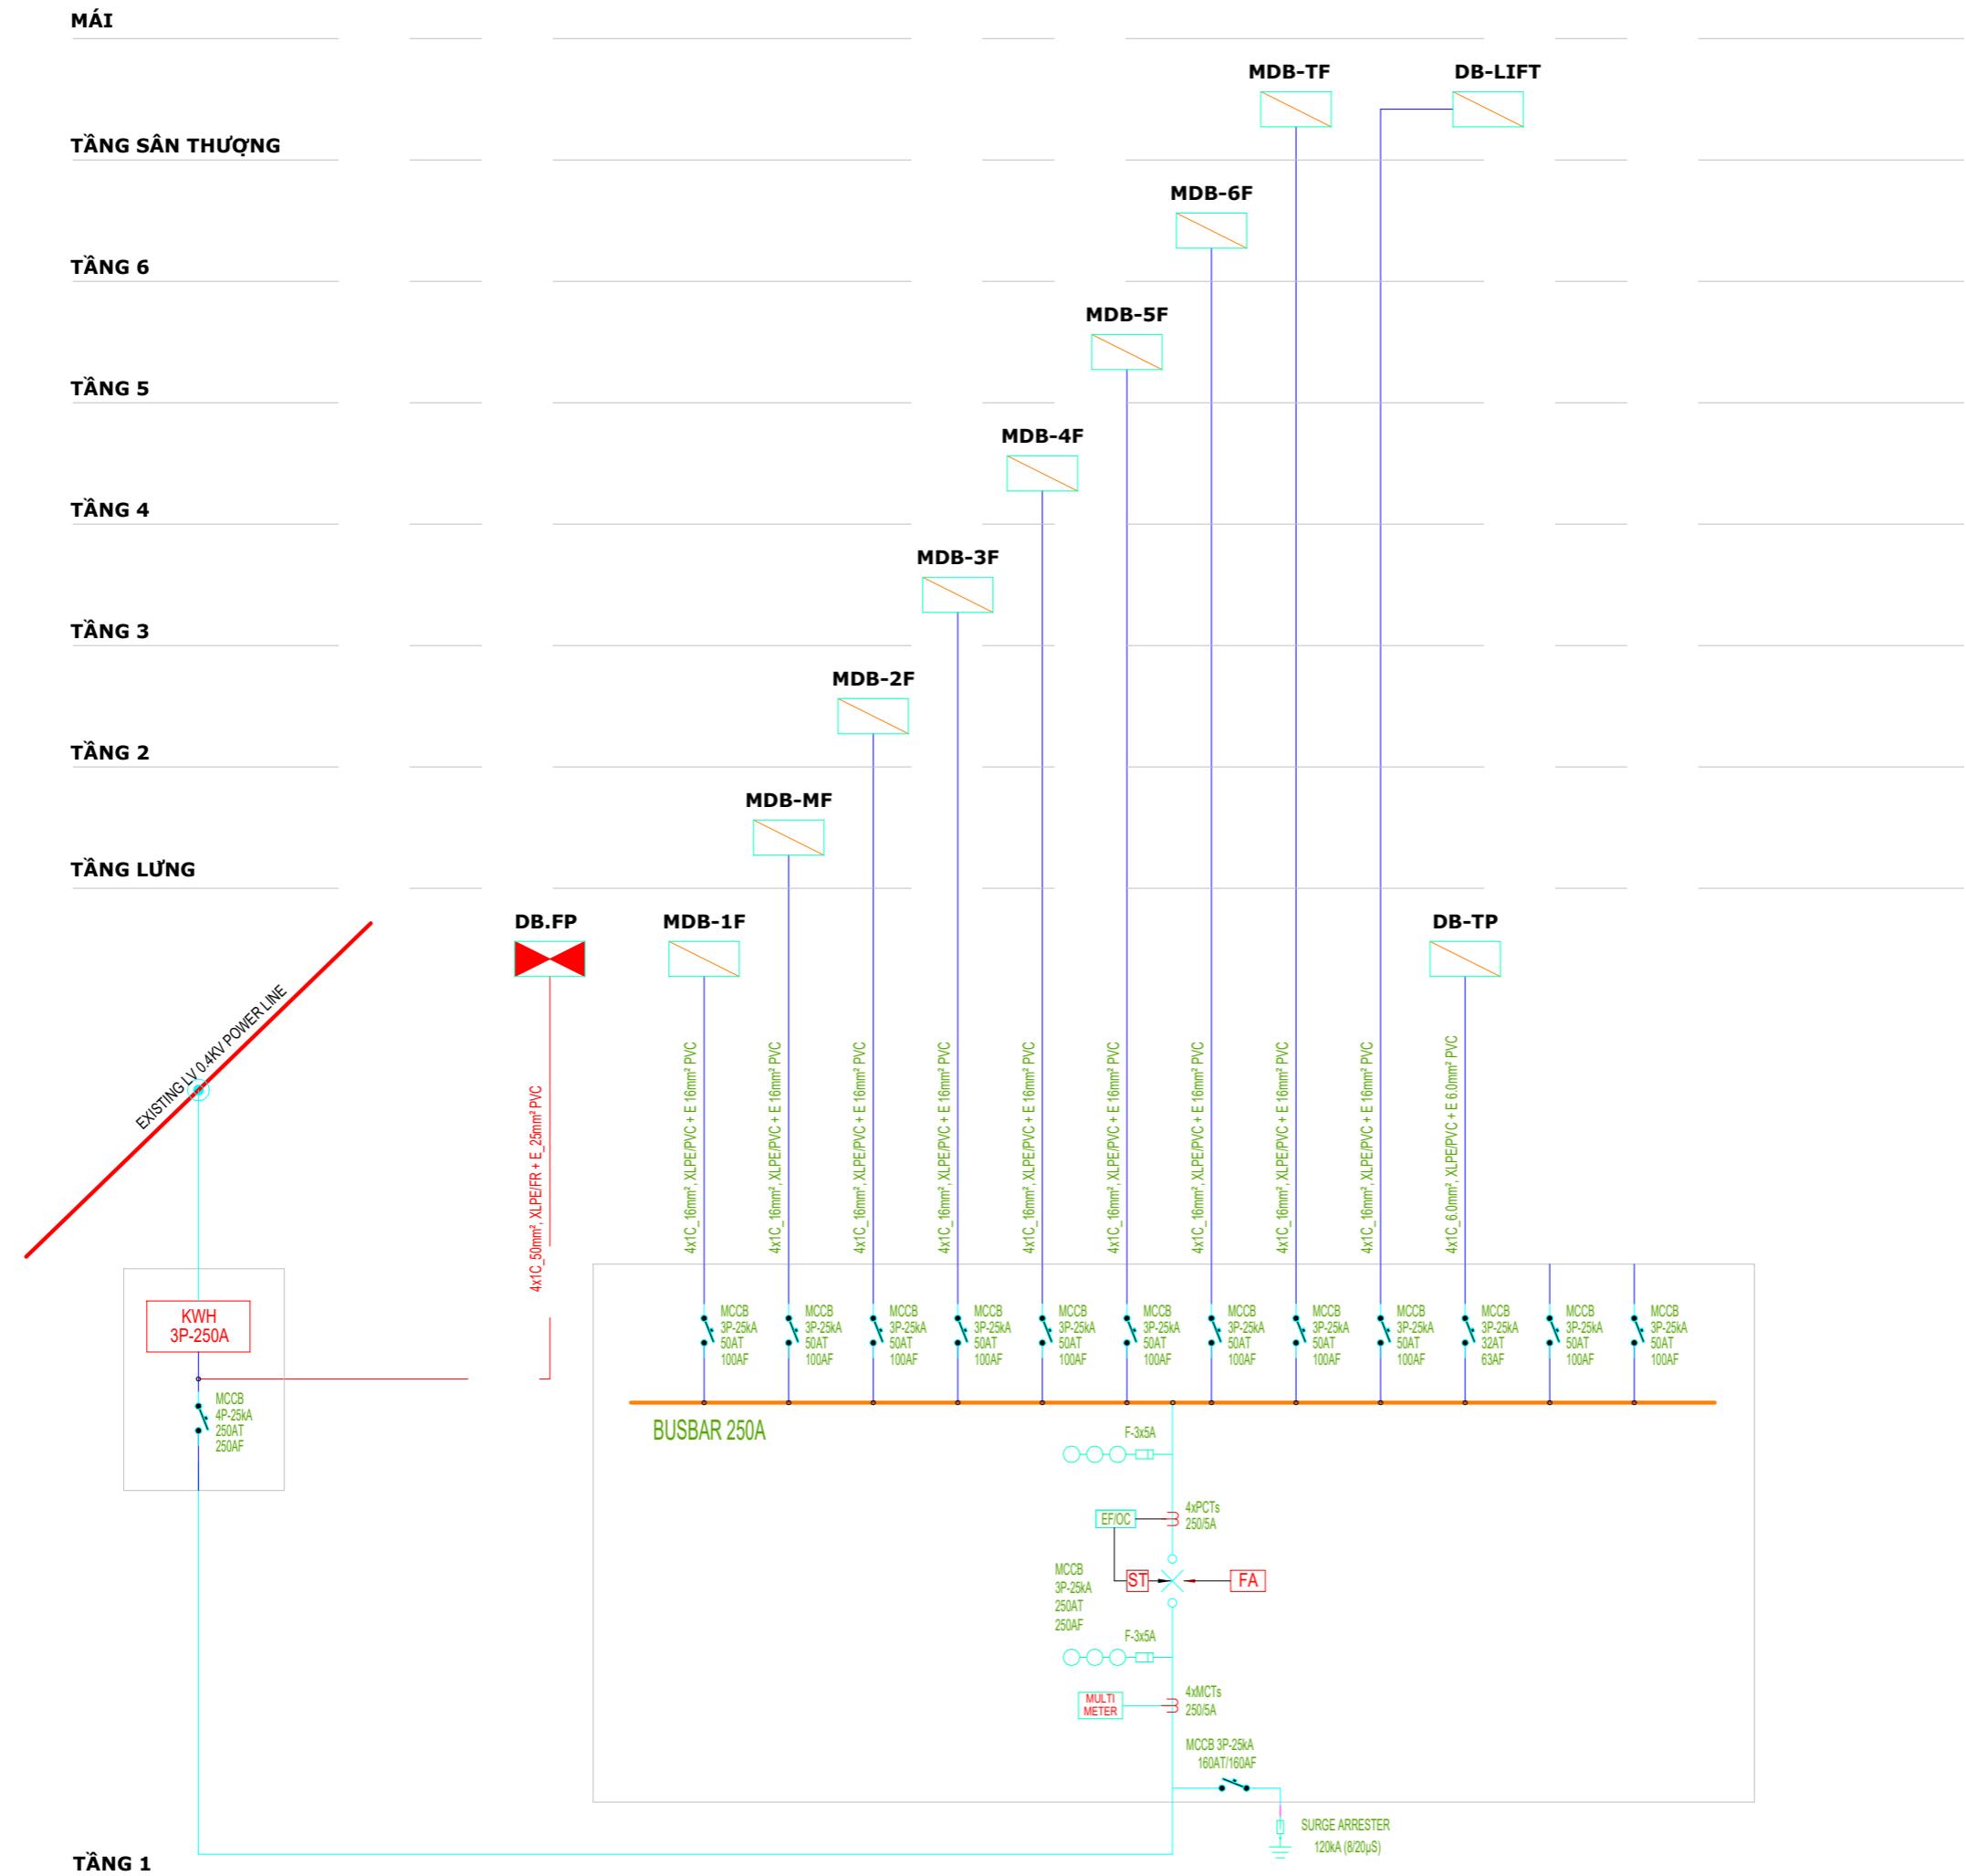

Mục đích phát hành/Release status:	
Thiết kế sơ/Preliminary:	
Bản vẽ trình duyệt/For approval:	
Bản vẽ tham khảo/For reference:	
Bản vẽ thi công/For construction:	X
Bản vẽ hiệu chỉnh/Revising:	
Bản vẽ hoàn công/As built:	

Đơn vị thiết kế - Thi công:

**CÔNG TY
CỔ PHẦN KIẾN TRÚC
- XÂY DỰNG ĐỨC AN**

Địa chỉ:
Lâm Văn Bền - Phường
Lênh - Quận 7- TP.HCM

Công trình/ Project:

BINH DUONG HOTEL

Hàng mục/ Item

THIẾT KẾ ĐIỆN NƯỚC

Bản vẽ/ Drawing name:

SƠ ĐỒ NGUYÊN LÝ-HỆ THỐNG CẤP ĐIỆN

Chủ trì thiết kế/ Project manager:



KTS. Vũ Minh Lâm

Thiết kế/ Desginer:



KTS. Vũ Minh Lâm

Tỉ lệ/ Scale: 1/100 Ngày: 04/2025

Số bản vẽ: E1-101

Mục đích phát hành/Release status:
Thiết kế sơ/Preliminary:
Bản vẽ trình duyệt/For approval:
Bản vẽ tham khảo/For reference:
Bản vẽ thi công/For construction:
Bản vẽ hiệu chỉnh/Revising:
Bản vẽ hoàn công/As built:

	PANEL NAME:	MDB-1F													
	Location:	PHÒNG TỦ ĐIỆN TẦNG													
	Supply From:	MDB													
Circuit Number	Line Name	Type	Protection Current Ic [A]	Short Circuit Current Ics [kA]	Poles of CB	Control Type	Voltage	A	B	C	Load Name	Wire Type	WireSize	Installation Method	
1	S1	MCB	20 A	10	1		220 V	800			Ổ CĂM	Cu/PVC	2 x 2.5mm2, CV + E_2.5mm2, CV	PVC D20	
2	S2	MCB	20 A	10	1		220 V		2,000		Ổ CĂM	Cu/PVC	2 x 2.5mm2, CV + E_2.5mm2, CV	PVC D20	
3	S3	MCB	20 A	10	1		220 V			750	Ổ CĂM	Cu/PVC	2 x 2.5mm2, CV + E_2.5mm2, CV	PVC D20	
4	S4	MCB	20 A	10	1		220 V	500			Ổ CĂM	Cu/PVC	2 x 2.5mm2, CV + E_2.5mm2, CV	PVC D20	
5	S5	MCB	20 A	10	1		220 V		500		Ổ CĂM	Cu/PVC	2 x 2.5mm2, CV + E_2.5mm2, CV	PVC D20	
6	S5	MCB	20 A	10	1		220 V			800	Ổ CĂM	Cu/PVC	2 x 2.5mm2, CV + E_2.5mm2, CV	PVC D20	
7	S5	MCB	20 A	10	1		220 V	250			Ổ CĂM	Cu/PVC	2 x 2.5mm2, CV + E_2.5mm2, CV	PVC D20	
8	S6	MCB	20 A	10	1		220 V		250		Ổ CĂM	Cu/PVC	2 x 2.5mm2, CV + E_2.5mm2, CV	PVC D20	
9	P1	MCB	25 A	10	1		220 V			3,000	CỬA CUÔN	Cu/PVC	2 x 4.0mm2, CV + E_4.0mm2, CV	PVC D20	
10	AC	MCB	20 A	10	1		220 V	2,500			MÁY LẠNH	Cu/PVC	2 x 4.0mm2, CV + E_2.0mm2, CV	PVC D20	
11	LTG1	MCB	20 A	6	1		220 V		293		LTG	Cu/PVC	2 x 1.5mm2, CV + E_1.5mm2, CV	PVC D20	
12	LTG2	MCB	20 A	6	1		220 V			278	LTG	Cu/PVC	2 x 1.5mm2, CV + E_1.5mm2, CV	PVC D20	
13	LTG3	MCB	20 A	6	1		220 V	21			LTG	Cu/PVC	2 x 1.5mm2, CV + E_1.5mm2, CV	PVC D20	
14	ST1	MCB	20 A	6	1		220 V		168		LTG	Cu/PVC	2 x 1.5mm2, CV + E_1.5mm2, CV	PVC D20	
15	ST2	MCB	20 A	6	1		220 V			126	LTG	Cu/PVC	2 x 1.5mm2, CV + E_1.5mm2, CV	PVC D20	
16											Space				
17											Space				
18											Space				
Total Load: [kVA]							4.1	3.2	4.9						
Total Amps: [A]							19 A	14 A	23 A						
Total Connected Load: [kA]							12.11373								
Factor							1								
Spare [%]							20								
Calculation Total Load: [kA]							14.540002								
Calculation Total Amps: [A]							22.024963								
Line In:	MCB-3P 50 A-10 kA		Main Cable:					4x16mm2, CXV + E_16mm2, CV				MÁNG CẤP			
Legend:															

Mục đích phát hành/Release status:
Thiết kế sơ/Preliminary:
Bản vẽ trình duyệt/For approval:
Bản vẽ tham khảo/For reference:
Bản vẽ thi công/For construction:
Bản vẽ hiệu chỉnh/Revising:
Bản vẽ hoàn công/As built:

Đơn vị thiết kế - Thi công:
**CÔNG TY
CỔ PHẦN KIẾN TRÚC
- XÂY DỰNG ĐỨC AN**

Địa chỉ:
60/10/2 Lâm Văn Bền - Phường
Tân Kiểng - Quận 7- TP.HCM

Công trình/ Project:
BINH DUONG HOTEL

Hạng mục/ Item:
**THIẾT KẾ
ĐIỆN NƯỚC**

Bản vẽ/ Drawing name:
**SƠ ĐỒ NGUYỄN LÝ-TU
ĐIỆN MDB-1F**

Chủ trì thiết kế/ Project manager:

KTS. Vũ Minh Lâm

Thiết kế/ Desginer:

KTS. Vũ Minh Lâm

Tỉ lệ/ Scale: 1/100 Ngày: 04/2025

Số bản vẽ: E1-102 No:

Mục đích phát hành/Release status:
Thiết kế sơ/Preliminary:
Bản vẽ trình duyệt/For approval:
Bản vẽ tham khảo/For reference:
Bản vẽ thi công/For construction: <input checked="" type="checkbox"/>
Bản vẽ hiệu chỉnh/Revising:
Bản vẽ hoàn công/As built:

BMT Building Management Technology		PANEL: MDB-MF																	
		Location: PHÒNG TỦ ĐIỆN TẦNG																	
		Supply From: MDB																	
<hr/>																			
Circuit Number	Line Name	Type	Protection Current Ic [A]	Short Circuit Current Ics [kA]	Poles of CB	Control Type	Voltage	A	B	C	Load Name	Wire Type	WireSize		Installation Method				
1	P1	MCB	32 A	10	2		220 V	6,117			DB-MF-P1	Cu/PVC	2 x 6.0mm2, CV + E_6.0mm2, CV		PVC D20				
2	P2	MCB	32 A	10	2		220 V		6,134		DB-MF-P2	Cu/PVC	2 x 6.0mm2, CV + E_6.0mm2, CV		PVC D20				
3	P3	MCB	32 A	10	2		220 V			7,400	DB-MF-P3	Cu/PVC	2 x 6.0mm2, CV + E_6.0mm2, CV		PVC D20				
4	P4	MCB	32 A	10	2		220 V	7,400			DB-MF-P4	Cu/PVC	2 x 6.0mm2, CV + E_6.0mm2, CV		PVC D20				
5	P5	MCB	32 A	10	2		220 V		7,000		DB-MF-P5	Cu/PVC	2 x 6.0mm2, CV + E_6.0mm2, CV		PVC D20				
6	EAF	MCB	20 A	6	2		220 V			500	QUẠT HÚT	Cu/PVC	2 x 2.5mm2, CV + E_2.5mm2, CV		PVC D20				
7	S1	MCB	20 A	6	1		220 V	1,200			Ô CĂM	Cu/PVC	2 x 2.5mm2, CV + E_2.5mm2, CV		PVC D20				
8	LTG	MCB	10 A	6	1		220 V		258		CHIẾU SÁNG	Cu/PVC	2 x 1.5mm2, CV + E_1.5mm2, CV		PVC D20				
9																			
											Space								
											Space								
											Space								
								Total Load: [kVA]	14.7	13.4	7.9								
								Total Amps: [A]	71 A	65 A	36 A								
								Total Connected Load: [kA]	35.962929										
								Factor	0.7										
								Spare [%]	10										
								Calculation Total Load: [kA]	27.698172										
								Calculation Total Amps: [A]	41.956751										
Line In:	MCB-3P 50 A-10kA											4x16mm2, CXV + E_16mm2, CV		MÁNG CÁP					
Legend:																			

Mục đích phát hành/Release status:	
Thiết kế sơ/Preliminary:	
Bản vẽ trình duyệt/For approval:	
Bản vẽ tham khảo/For reference:	
Bản vẽ thi công/For construction:	<input checked="" type="checkbox"/>
Bản vẽ hiệu chỉnh/Revising:	
Bản vẽ hoàn công/As built:	
Đơn vị thiết kế - Thi công:	CÔNG TY CỔ PHẦN KIẾN TRÚC - XÂY DỰNG ĐỨC AN
Địa chỉ:	60/10/2 Lâm Văn Bền - Phường Tân Kiểng - Quận 7- TP.HCM
Công trình/ Project:	BINH DUONG HOTEL
Hạng mục/ Item:	THIẾT KẾ ĐIỆN NƯỚC
Bản vẽ/ Drawing name:	SƠ ĐỒ NGUYỄN LÝ-TU ĐIỆN MDB-MF
Chủ trì thiết kế/ Project manager:	
KTS. Vũ Minh Lâm	
Thiết kế/ Desginer:	
	
KTS. Vũ Minh Lâm	
Tỉ lệ/ Scale:	1/100
Ngày: Ngày:	04/2025
Số bản vẽ:	E1-103
No:	

Mục đích phát hành/Release status:
Thiết kế sơ/Preliminary:
Bản vẽ trình duyệt/For approval:
Bản vẽ tham khảo/For reference:
Bản vẽ thi công/For construction: <input checked="" type="checkbox"/>
Bản vẽ hiệu chỉnh/Revising:
Bản vẽ hoàn công/As built:

BMT Building Management Technology		PANEL: MDB-2F																	
		Location:																	
		Supply From: MDB																	
Circuit Number	Line Name	Type	Protection Current Ic [A]	Short Circuit Current Ics [kA]	Poles of CB	Control Type	Voltage	A	B	C	Load Name	Wire Type	WireSize		Installation Method				
1		MCB	32 A	10	2		220 V	7,187			DB-2F-P1	Cu/PVC	2 x 6.0mm2, CV + E_6.0mm2, CV		MÁNG CÁP				
2		MCB	32 A	10	2		220 V		7,153		DB-2F-P2	Cu/PVC	2 x 6.0mm2, CV + E_6.0mm2, CV		MÁNG CÁP				
3		MCB	32 A	10	2		220 V			7,170	DB-2F-P3	Cu/PVC	2 x 6.0mm2, CV + E_6.0mm2, CV		MÁNG CÁP				
4		MCB	32 A	10	2		220 V	3,434			DB-2F-P4	Cu/PVC	2 x 6.0mm2, CV + E_6.0mm2, CV		MÁNG CÁP				
5		MCB	32 A	10	2		220 V		7,551		DB-2F-P5	Cu/PVC	2 x 6.0mm2, CV + E_6.0mm2, CV		MÁNG CÁP				
6		MCB	32 A	10	2		220 V			7,551	DB-2F-P6	Cu/PVC	2 x 6.0mm2, CV + E_6.0mm2, CV		MÁNG CÁP				
7		MCB	32 A	10	2		220 V	7,117			DB-2F-P7	Cu/PVC	2 x 4.0mm2, CV + E_4.0mm2, CV		MÁNG CÁP				
8		MCB	20 A	6	1		220 V		1,200		Ổ CĂM	Cu/PVC	2 x 2.5mm2, CV + E_2.5mm2, CV		PVC D20				
9		MCB	20 A	6	1		220 V			500	QUẠT HÚT	Cu/PVC	2 x 2.5mm2, CV + E_2.5mm2, CV		PVC D20				
10		MCB	10 A	6	1		220 V	200			CHIẾU SÁNG	Cu/PVC	2 x 1.5mm2, CV + E_1.5mm2, CV		PVC D20				
11																			
12																			
13																			
14																			
15																			
											Space								
											Space								
											Space								
				Total Load: [kVA]		17.9	15.9	15.2											
				Total Amps: [A]		82 A	73 A	69 A											
				Total Connected Load: [kA]		49.021715													
				Factor															
				Spare [%]															
				Calculation Total Load: [kVA]		0													
				Calculation Total Amps: [A]		0													
Line In:		1 A																	
Legend:																			

Đơn vị thiết kế - Thi công:
**CÔNG TY
CỔ PHẦN KIẾN TRÚC
- XÂY DỰNG ĐỨC AN**

Địa chỉ:
60/10/2 Lâm Văn Bền - Phường
Tân Kiêng - Quận 7- TP.HCM

Công trình/ Project:
BINH DUONG HOTEL

Hạng mục/ Item:
**THIẾT KẾ
ĐIỆN NƯỚC**

Bản vẽ/ Drawing name:
**SƠ ĐỒ NGUYỄN LÝ-TỦ
ĐIỆN MDB-(2-6)F**

Chủ trì thiết kế/ Project manager:

KTS. Vũ Minh Lâm

Thiết kế/ Desginer:

KTS. Vũ Minh Lâm

Tỉ lệ/ Scale: 1/100 Ngày: 04/2025
Số bản vẽ: E1-104 No:

Mục đích phát hành/Release status:	
Thiết kế sơ/Preliminary:	
Bản vẽ trình duyệt/For approval:	
Bản vẽ tham khảo/For reference:	
Bản vẽ thi công/For construction:	<input checked="" type="checkbox"/>
Bản vẽ hiệu chỉnh/Revising:	
Bản vẽ hoàn công/As built:	

	PANEL NAME:	MDB-TF															
	Location:																
	Supply From:																
Circuit Number	Line Name	Type	Protection Current Ic [A]	Short Circuit Current Ics [kA]	Poles of CB	Control Type	Voltage	A	B	C	Load Name	Wire Type	WireSize	Installation Method			
1		MCB	32 A	10	1		220 V	4,598			DB-TF-P1	Cu/PVC	2 x 6.0mm2, CV + E_6.0mm2, CV	MÁNG CẤP			
2		MCB	32 A	10	1		220 V		2,173		DB-TF-CF	Cu/PVC	2 x 6.0mm2, CV + E_6.0mm2, CV	MÁNG CẤP			
3		MCB	20 A	6	1		220 V			1,200	Ố CĂM	Cu/PVC	2 x 2.5mm2, CV + E_2.5mm2, CV	PVC D20			
4		MCB	20 A	6	1		220 V	1,600			Ố CĂM	Cu/PVC	2 x 2.5mm2, CV + E_2.5mm2, CV	PVC D20			
5		MCB	20 A	6	1		220 V		1,600		Ố CĂM	Cu/PVC	2 x 2.5mm2, CV + E_2.5mm2, CV	PVC D20			
6		MCB	20 A	10	1		220 V			1,600	Ố CĂM	Cu/PVC	2 x 2.5mm2, CV + E_2.5mm2, CV	PVC D20			
7		MCB	20 A	6	1		220 V	1,600			Ố CĂM	Cu/PVC	2 x 2.5mm2, CV + E_2.5mm2, CV	PVC D20			
8		MCB	20 A	6	1		220 V		1,600		Ố CĂM	Cu/PVC	2 x 2.5mm2, CV + E_2.5mm2, CV	PVC D20			
9		MCB	10 A	6	1		220 V			468	CHIẾU SÁNG	Cu/PVC	2 x 1.5mm2, CV + E_1.5mm2, CV	PVC D20			
10		MCB	10 A	6	1		220 V	360			CHIẾU SÁNG	Cu/PVC	2 x 1.5mm2, CV + E_1.5mm2, CV	PVC D20			
11		MCB	10 A	6	1		220 V		252		CHIẾU SÁNG	Cu/PVC	2 x 1.5mm2, CV + E_1.5mm2, CV	PVC D20			
12		MCB	10 A	6	1		220 V			98	CHIẾU SÁNG	Cu/PVC	2 x 1.5mm2, CV + E_1.5mm2, CV	PVC D20			
13		MCB	10 A	6	1		220 V	378			CHIẾU SÁNG	Cu/PVC	2 x 1.5mm2, CV + E_1.5mm2, CV	PVC D20			
14		MCB	20 A	10	2		220 V		1,500		BƠM TĂNG ÁP	Cu/PVC	2 x 2.5mm2, CV + E_2.5mm2, CV	PVC D20			
15																	
16											Space						
17											Space						
18											Space						
				Total Load: [kVA]	8.4	7.1	3.3										
				Total Amps: [A]	41 A	35 A	15 A										
				Total Connected Load: [kA]	18.814472												
				Factor	0.8												
				Spare [%]	15												
				Calculation Total Load: [kA]	17.313513												
				Calculation Total Amps: [A]	26.226234												
Line In:	MCB-2P 50 A-10kA		Main Cable:	4x16mm2, CXV + E_16mm2, CV													
Legend:																	

Đơn vị thiết kế - Thi công:
**CÔNG TY
CỔ PHẦN KIẾN TRÚC
- XÂY DỰNG ĐỨC AN**

Địa chỉ:
60/10/2 Lâm Văn Bền - Phường
Tân Kiêng - Quận 7- TP.HCM

Công trình/ Project:
BINH DUONG HOTEL

Hạng mục/ Item:
**THIẾT KẾ
ĐIỆN NƯỚC**


Bản vẽ/ Drawing name:
**SƠ ĐỒ NGUYÊN LÝ-TỦ
ĐIỆN MDB-TF**

Chủ trì thiết kế/ Project manager:


KTS. Vũ Minh Lâm
Thiết kế/ Desginer:

KTS. Vũ Minh Lâm
Tỉ lệ/ Scale: 1/100 Ngày: 04/2025
Số bản vẽ: E1-105 No:

Mục đích phát hành/Release status:
Thiết kế sơ/Preliminary:
Bản vẽ trình duyệt/For approval:
Bản vẽ tham khảo/For reference:
Bản vẽ thi công/For construction:
Bản vẽ hiệu chỉnh/Revising:
Bản vẽ hoàn công/As built:

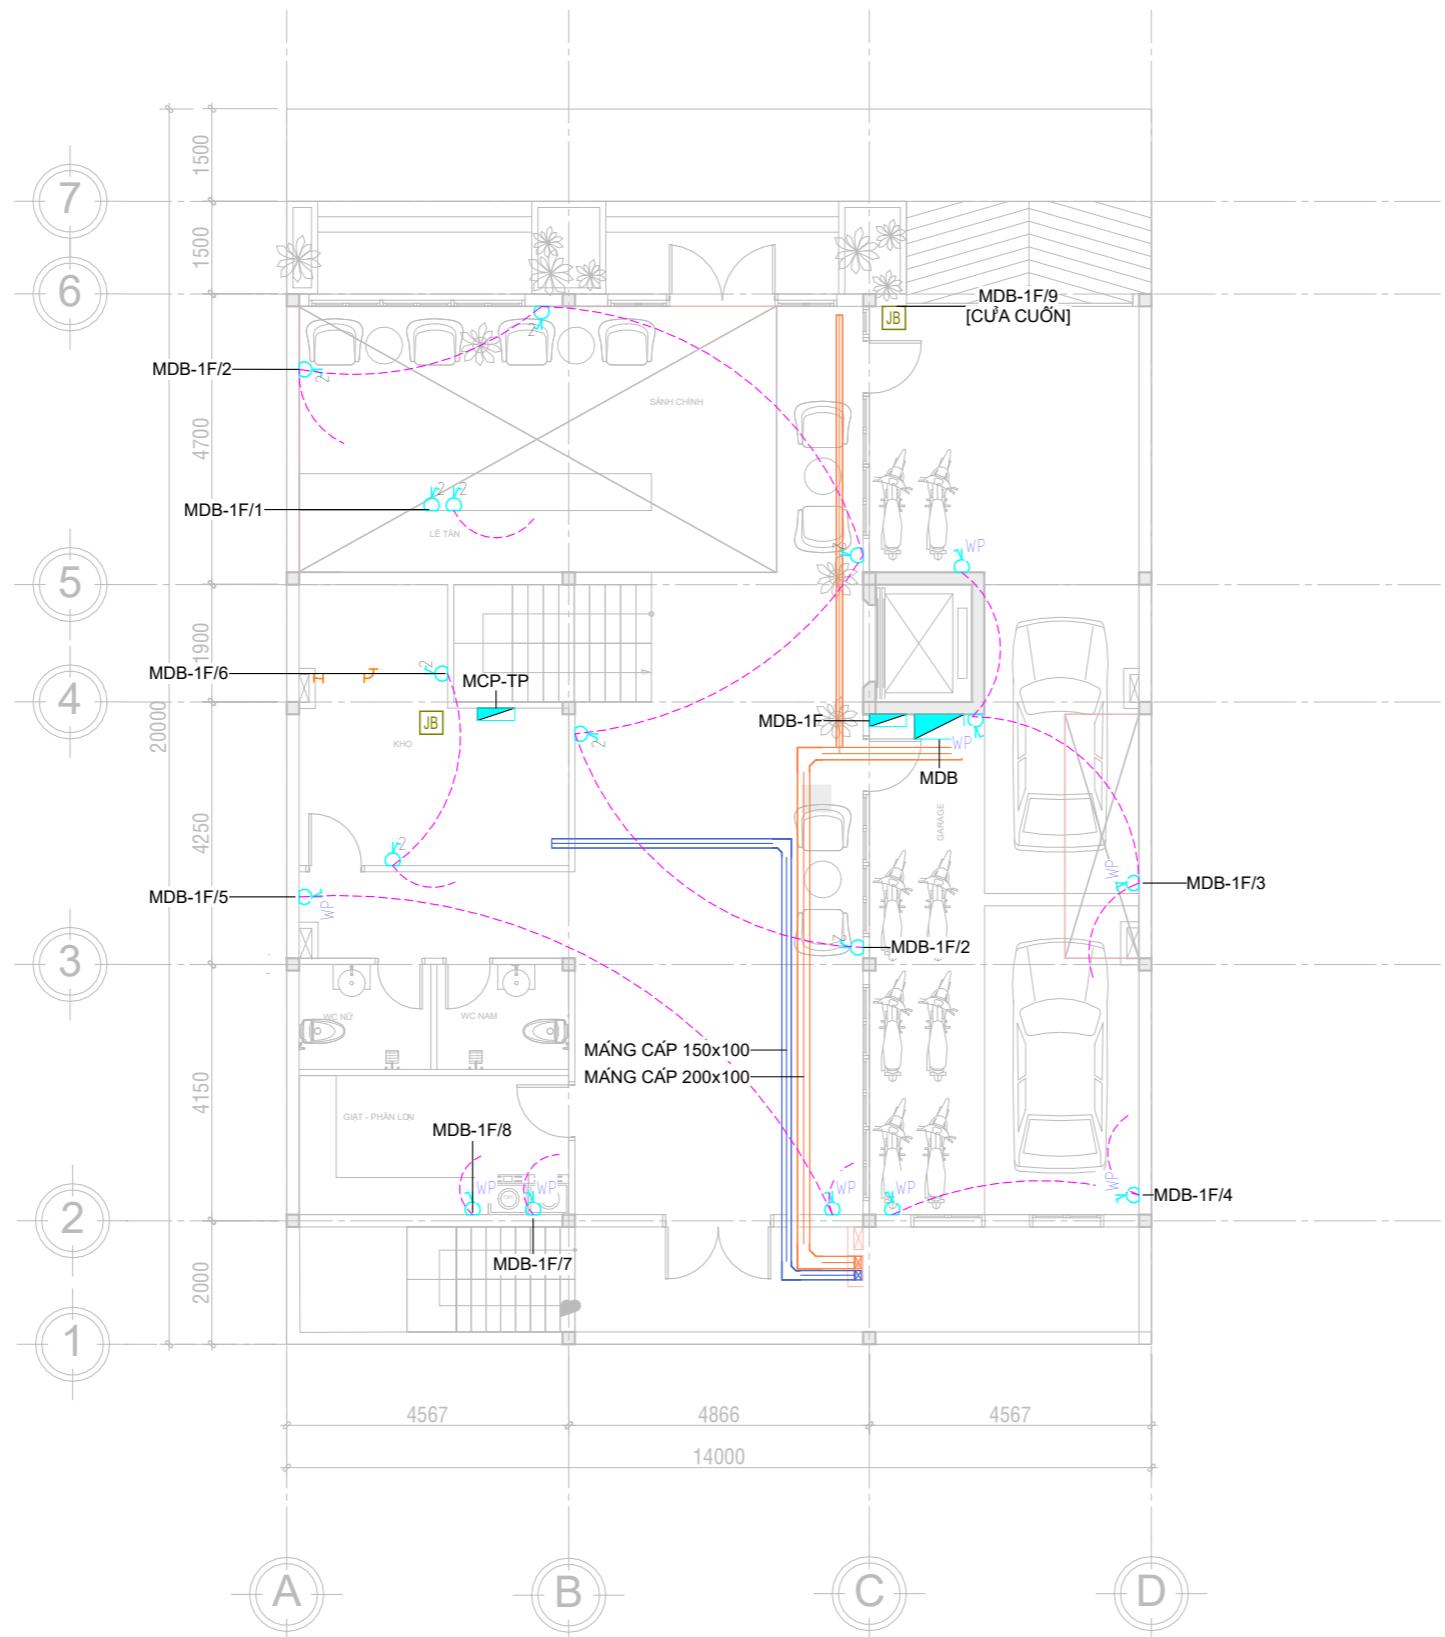

MẶT BẰNG TẦNG 1
TL:1/100

Đơn vị thiết kế - Thi công:

**CÔNG TY
CỔ PHẦN KIẾN TRÚC
- XÂY DỰNG ĐỨC AN**

Địa chỉ:
60/10/2 Lâm Văn Bền - Phường
Tân Kiểng - Quận 7- TP.HCM

Công trình/ Project:

BINH DUONG HOTEL

Hạng mục/ Item:

**THIẾT KẾ
ĐIỆN NƯỚC**

Bản vẽ/ Drawing name:

**HỆ THỐNG CẤP
NGUỒN, Ổ CẮM-TẦNG 1**

Chủ trì thiết kế/ Project manager:

KTS. Vũ Minh Lâm

Thiết kế/ Desginer:

KTS. Vũ Minh Lâm

Tỉ lệ/ Scale: 1/100 Ngày: 04/2025

Số bản vẽ: E1-201 No:

Mục đích phát hành/Release status:
Thiết kế sơ/Preliminary:
Bản vẽ trình duyệt/For approval:
Bản vẽ tham khảo/For reference:
Bản vẽ thi công/For construction:
Bản vẽ hiệu chỉnh/Revising:
Bản vẽ hoàn công/As built:

Đơn vị thiết kế - Thi công:

**CÔNG TY
CỔ PHẦN KIẾN TRÚC
- XÂY DỰNG ĐỨC AN**

Địa chỉ:
60/10/2 Lâm Văn Bền - Phường
Tân Kiểng - Quận 7- TP.HCM

Công trình/ Project:

BINH DUONG HOTEL

Hạng mục/ Item:

**THIẾT KẾ
ĐIỆN NƯỚC**

Bản vẽ/ Drawing name:

**HỆ THỐNG CẤP
NGUỒN, Ố CĂM-TẦNG
LỦNG**

Chủ trì thiết kế/ Project manager:


KTS. Vũ Minh Lâm

Thiết kế/ Desginer:

KTS. Vũ Minh Lâm

Tỉ lệ/ Scale: 1/100 Ngày: 04/2025


Số bản vẽ: E1-202 No:

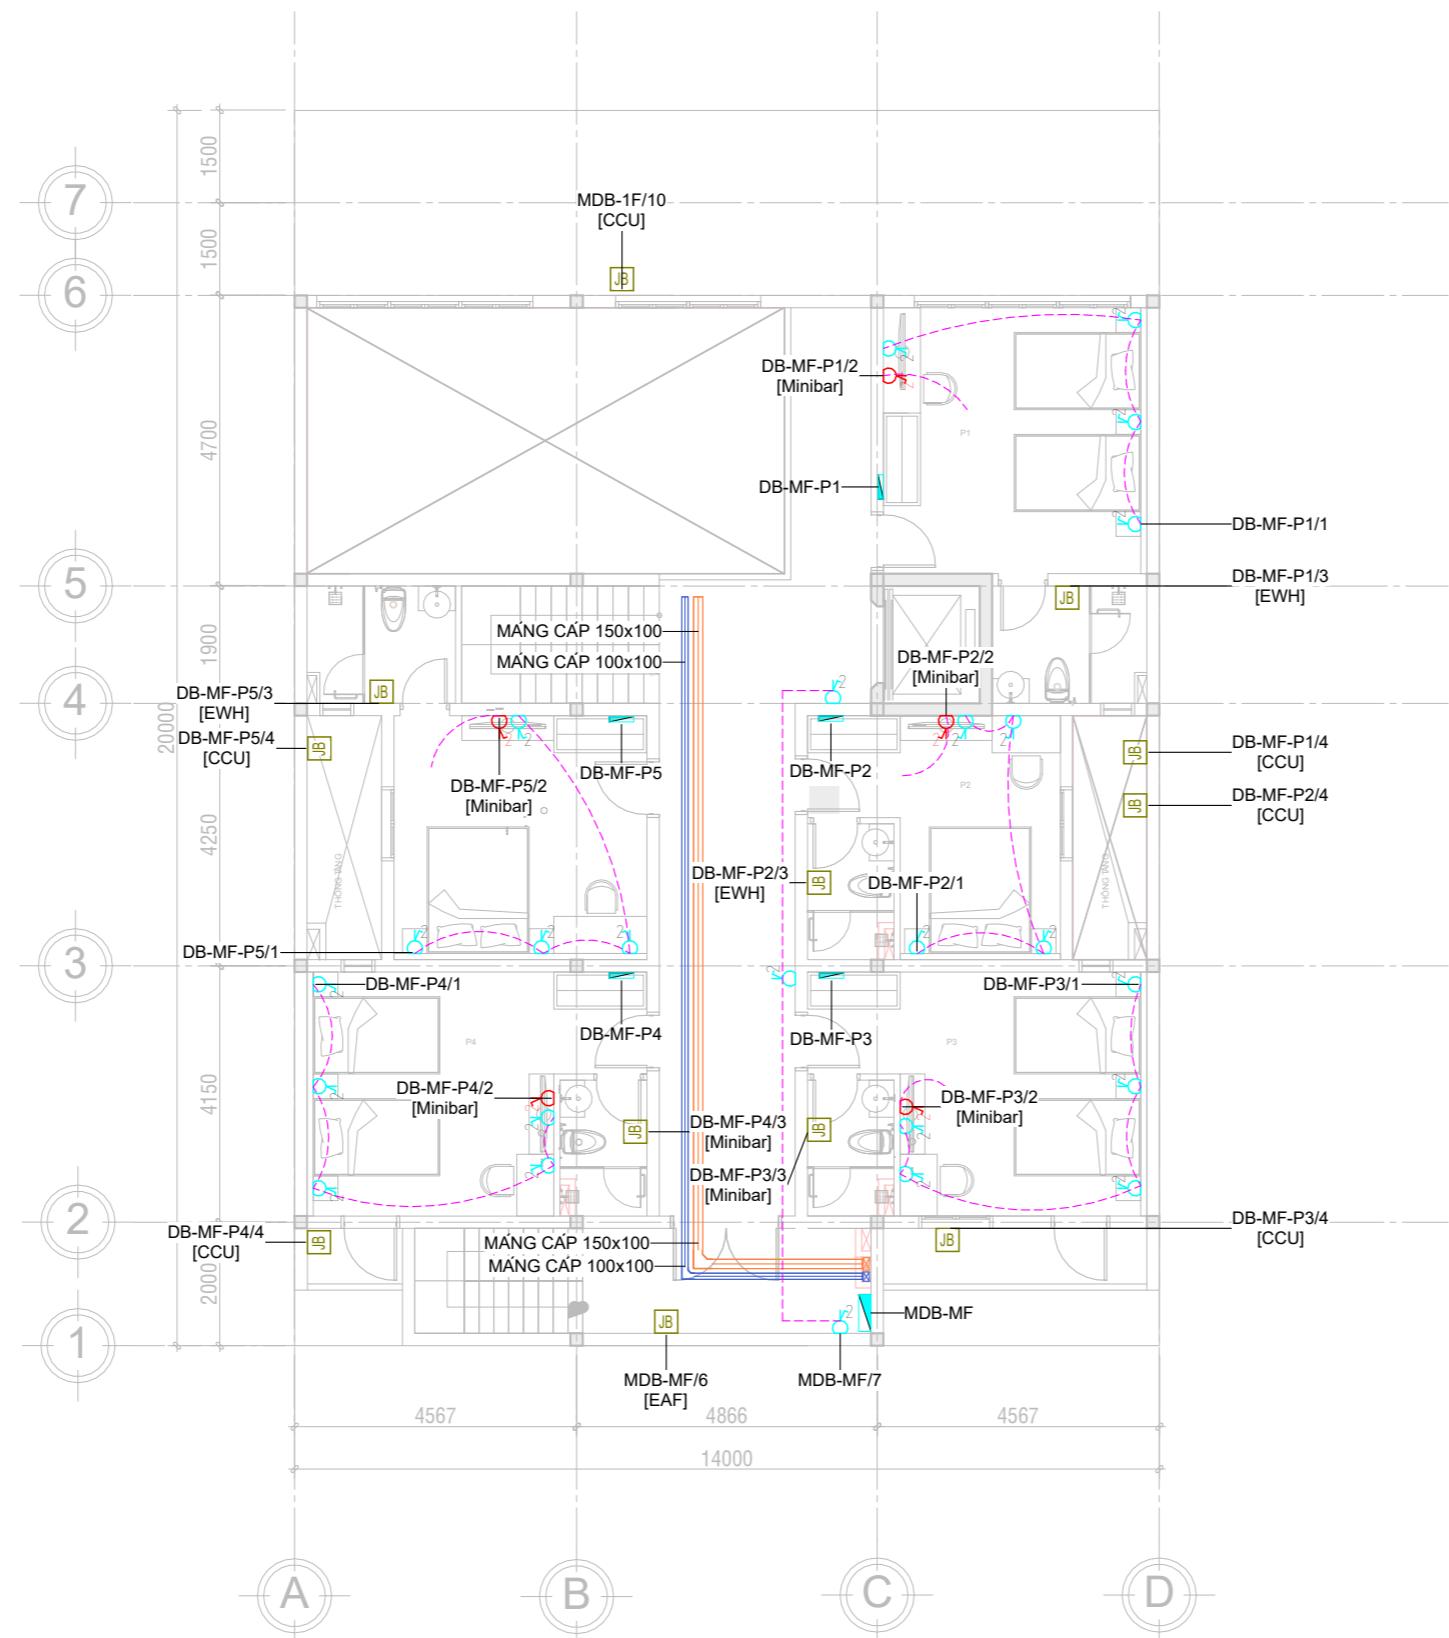

MẶT BẰNG TẦNG LỦNG

TL:1/100

Mục đích phát hành/Release status:
Thiết kế sơ/Preliminary:
Bản vẽ trình duyệt/For approval:
Bản vẽ tham khảo/For reference:
Bản vẽ thi công/For construction:
Bản vẽ hiệu chỉnh/Revising:
Bản vẽ hoàn công/As built:

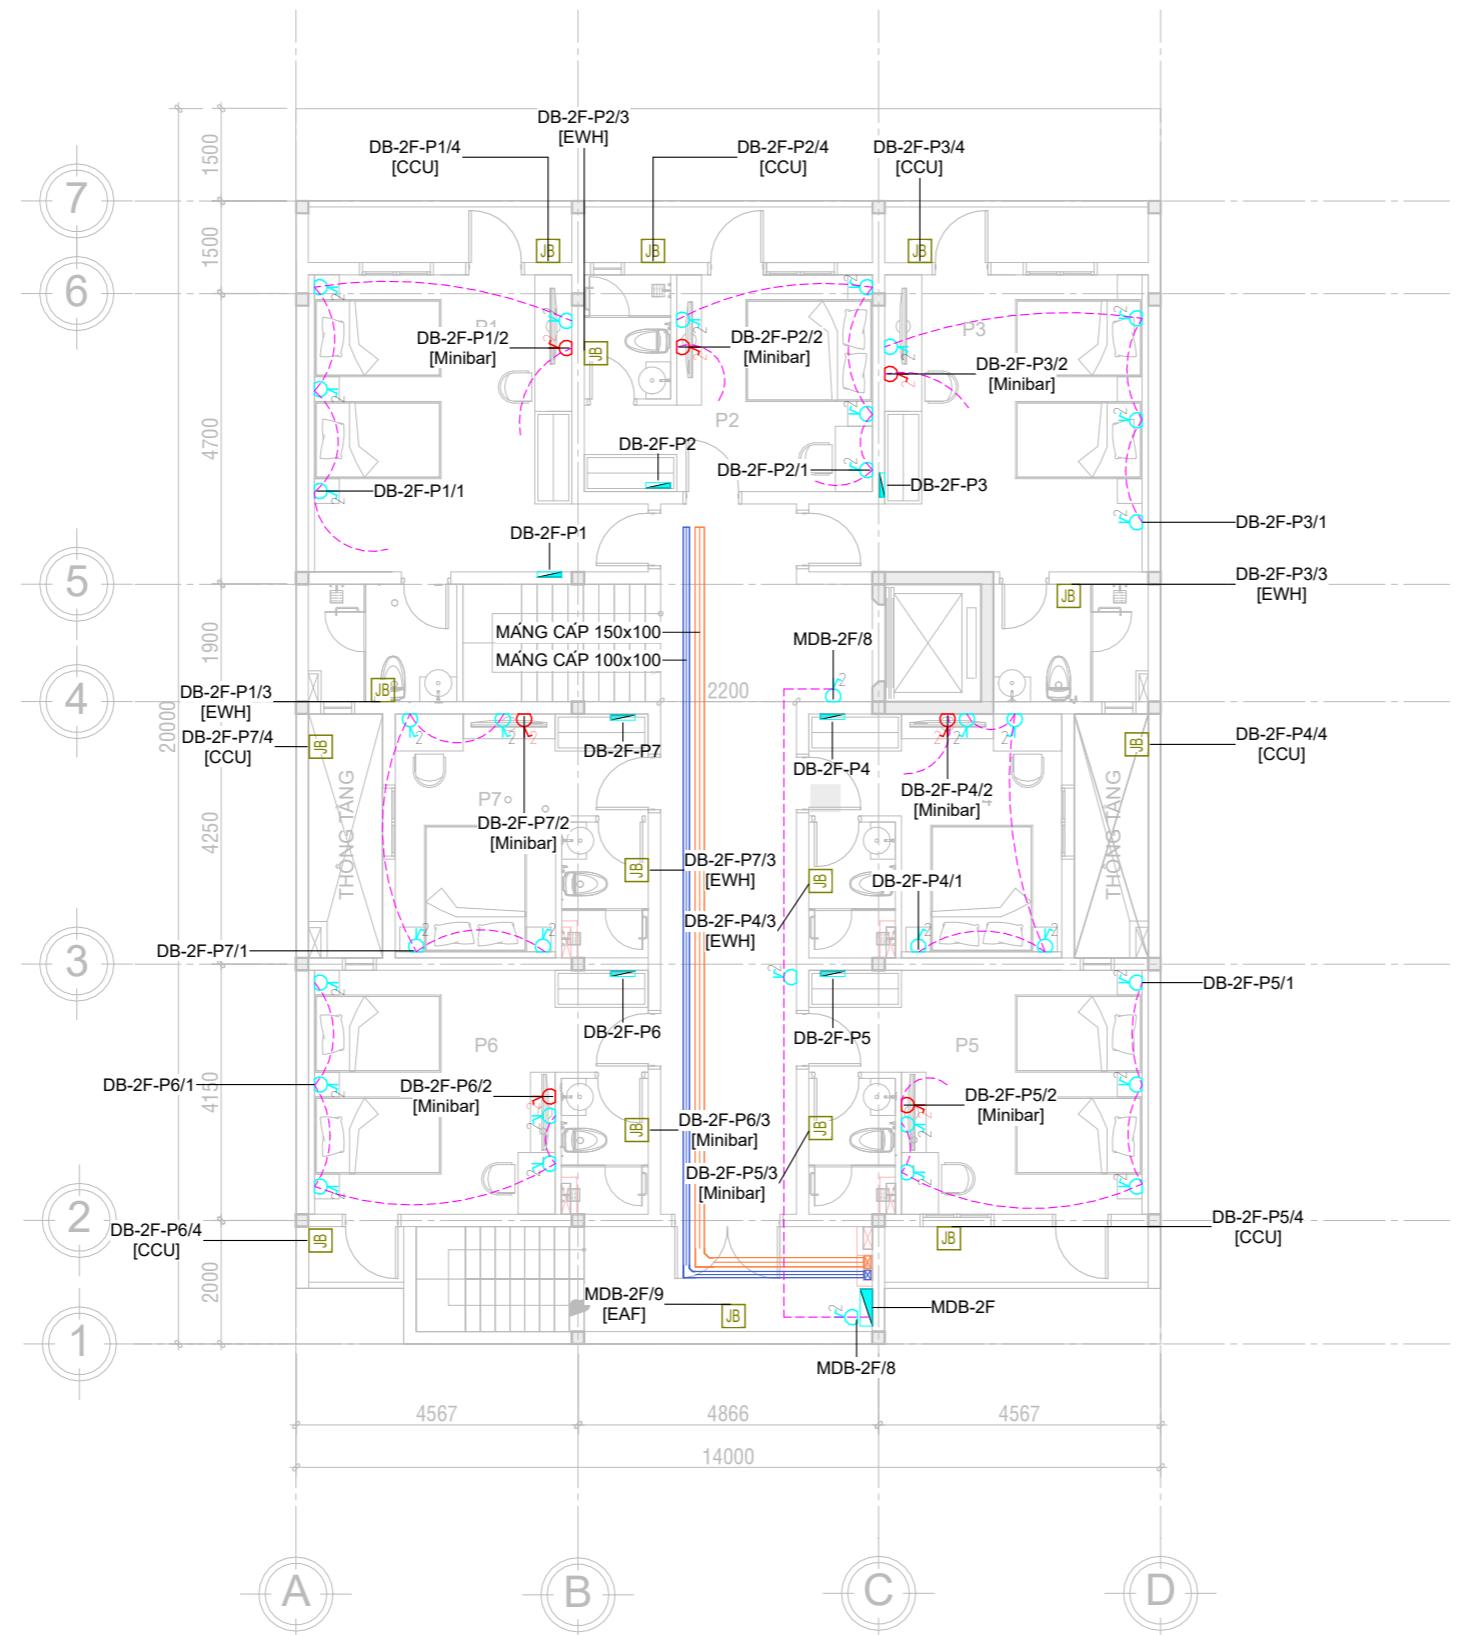

MẶT BẰNG TẦNG ĐIỆN HÌNH 2-6

TL:1/100

Đơn vị thiết kế - Thi công:

**CÔNG TY
CỔ PHẦN KIẾN TRÚC
- XÂY DỰNG ĐỨC AN**

Địa chỉ:
60/10/2 Lâm Văn Bền - Phường
Tân Kiểng - Quận 7- TP.HCM

Công trình/ Project:

BINH DUONG HOTEL

Hạng mục/ Item:

**THIẾT KẾ
ĐIỆN NƯỚC**

Bản vẽ/ Drawing name:

**HỆ THỐNG CẤP
NGUỒN, Ô CĂM-TẦNG
2-6**

Chủ trì thiết kế/ Project manager:

KTS. Vũ Minh Lâm

Thiết kế/ Desginer:

KTS. Vũ Minh Lâm

Tỉ lệ/ Scale: 1/100 Ngày: 04/2025

Số bản vẽ: E1-203 No:

Mục đích phát hành/Release status:
Thiết kế sơ/Preliminary:
Bản vẽ trình duyệt/For approval:
Bản vẽ tham khảo/For reference:
Bản vẽ thi công/For construction:
Bản vẽ hiệu chỉnh/Revising:
Bản vẽ hoàn công/As built:

Đơn vị thiết kế - Thi công:

**CÔNG TY
CỔ PHẦN KIẾN TRÚC
- XÂY DỰNG ĐỨC AN**

Địa chỉ:
60/10/2 Lâm Văn Bền - Phường
Tân Kiểng - Quận 7- TP.HCM

Công trình/ Project:

BINH DUONG HOTEL

Hạng mục/ Item:

**THIẾT KẾ
ĐIỆN NƯỚC**

Bản vẽ/ Drawing name:

**HỆ THỐNG CẤP
NGUỒN, Ô CĂM-TĀNG
SÂN THƯỢNG**

Chủ trì thiết kế/ Project manager:


KTS. Vũ Minh Lâm

Thiết kế/ Desginer:

KTS. Vũ Minh Lâm

Tỉ lệ/ Scale: 1/100 Ngày: 04/2025

Số bản vẽ: E1-204 No:

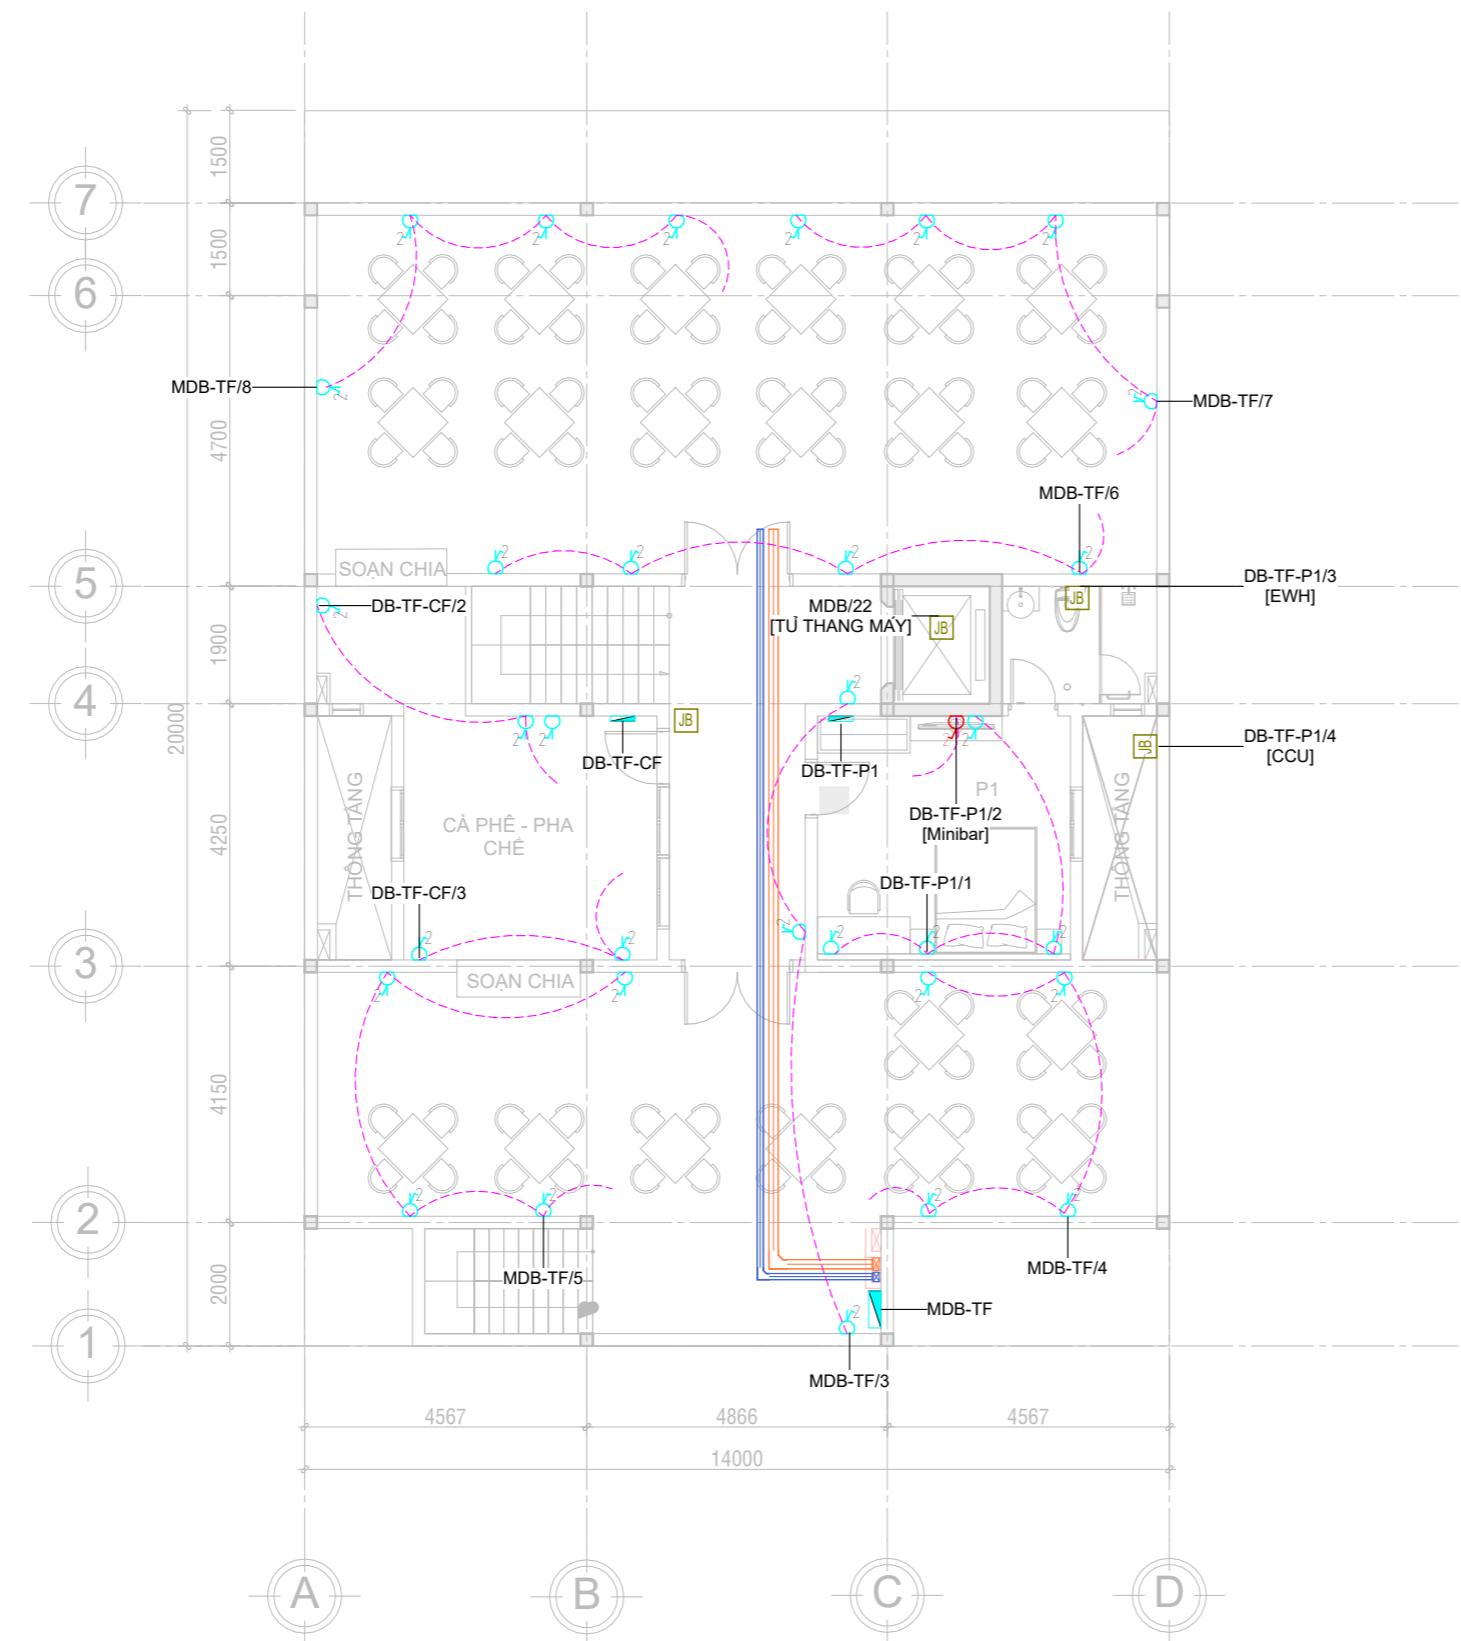

MẶT BẰNG TẦNG SÂN THƯỢNG

TL:1/100

Mục đích phát hành/Release status:
Thiết kế sơ/Preliminary:
Bản vẽ trình duyệt/For approval:
Bản vẽ tham khảo/For reference:
Bản vẽ thi công/For construction:
Bản vẽ hiệu chỉnh/Revising:
Bản vẽ hoàn công/As built:

Đơn vị thiết kế - Thi công:

**CÔNG TY
CỔ PHẦN KIẾN TRÚC
- XÂY DỰNG ĐỨC AN**

Địa chỉ:
60/10/2 Lâm Văn Bền - Phường
Tân Kiểng - Quận 7 - TP.HCM

Công trình/ Project:

BINH DUONG HOTEL

Hạng mục/ Item:

**THIẾT KẾ
ĐIỆN NƯỚC**

Bản vẽ/ Drawing name:

**HỆ THỐNG CHIẾU
SÁNG-TẦNG 1**

Chủ trì thiết kế/ Project manager:


KTS. Vũ Minh Lâm

Thiết kế/ Desginer:

KTS. Vũ Minh Lâm

Tỉ lệ/ Scale: 1/100 Ngày: 04/2025

Số bản vẽ: E2-201 No:

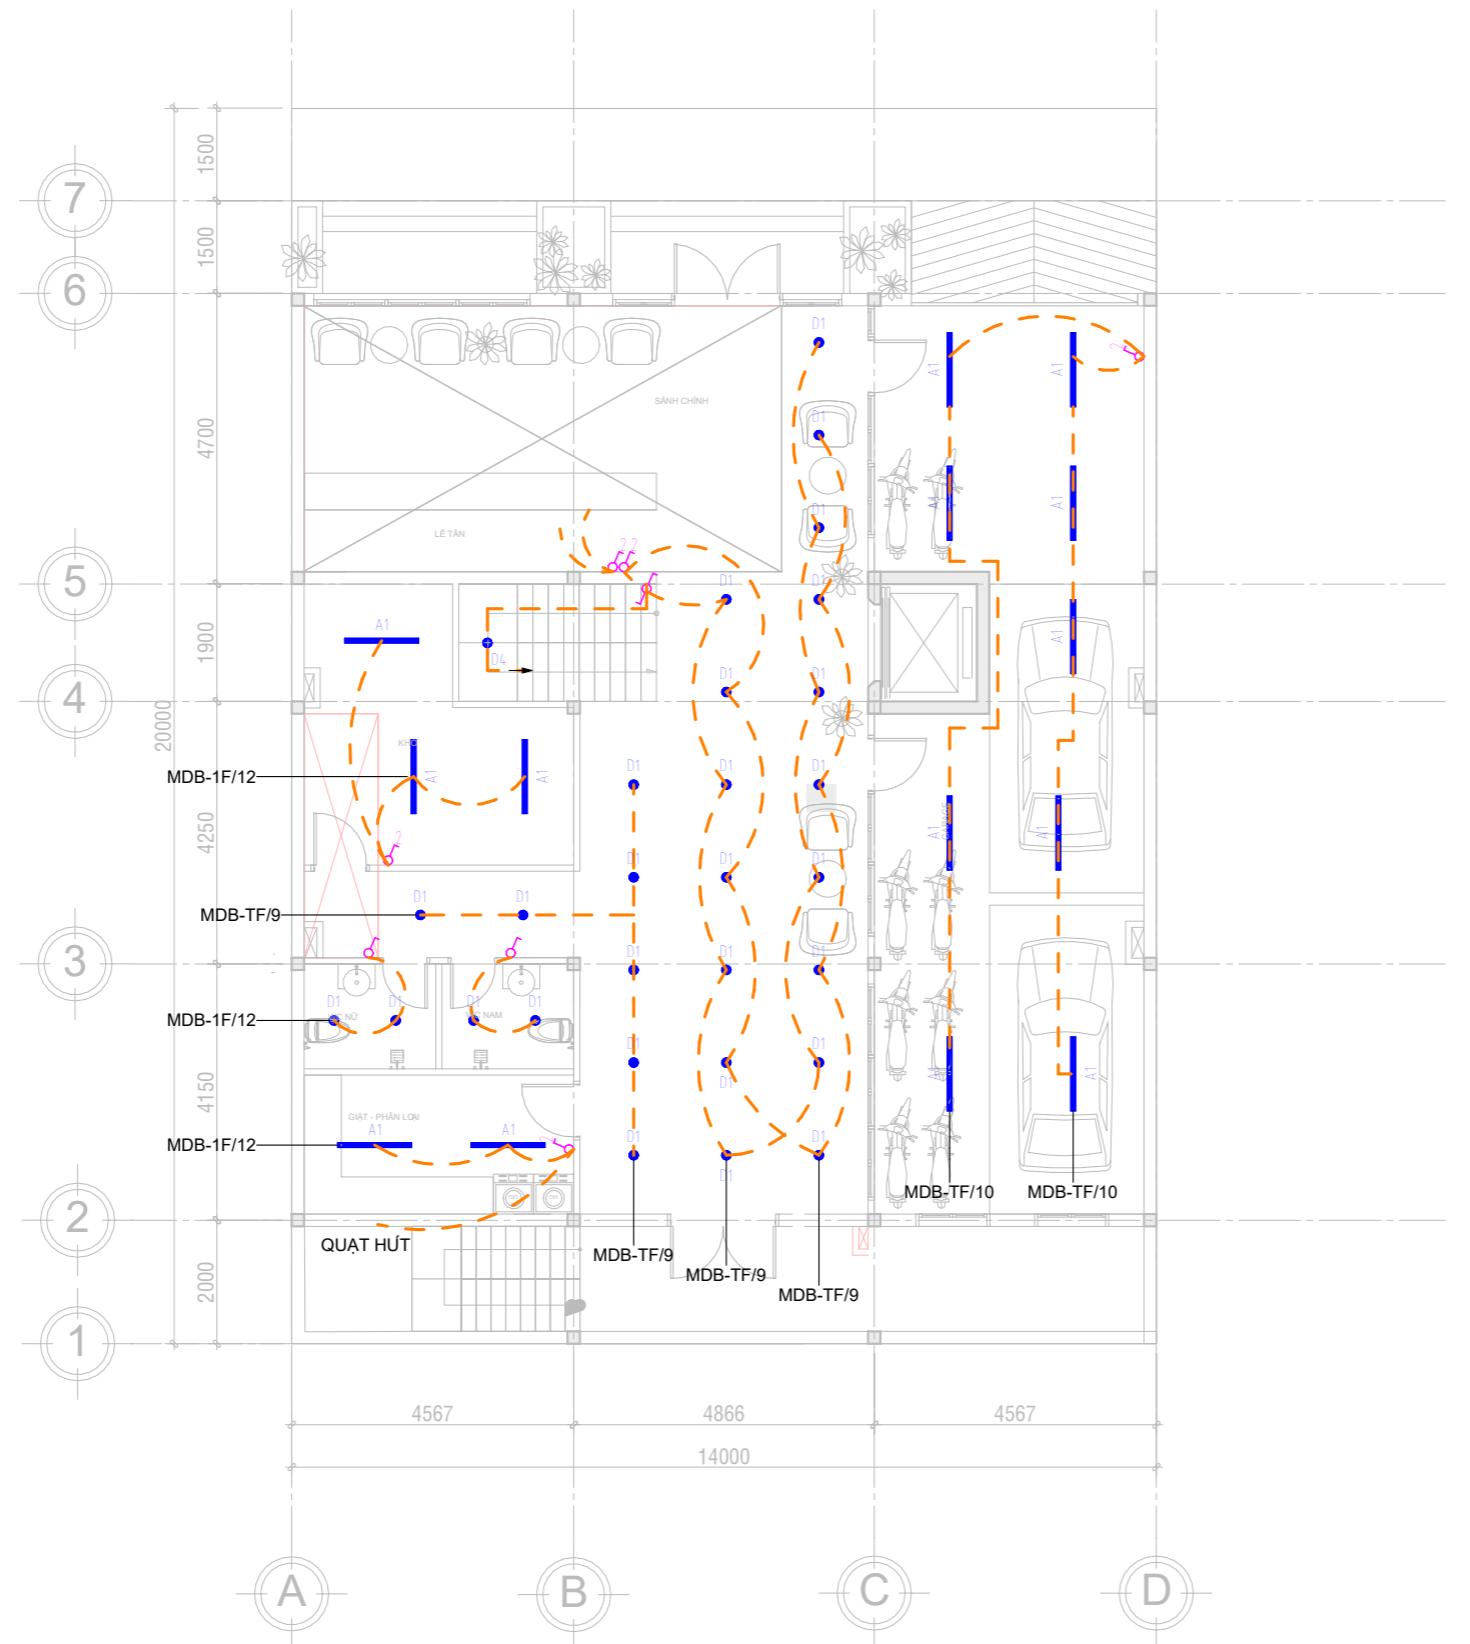

MẶT BẰNG TẦNG 1

TL:1/100

Mục đích phát hành/Release status:
Thiết kế sơ/Preliminary:
Bản vẽ trình duyệt/For approval:
Bản vẽ tham khảo/For reference:
Bản vẽ thi công/For construction:
Bản vẽ hiệu chỉnh/Revising:
Bản vẽ hoàn công/As built:

Đơn vị thiết kế - Thi công:

**CÔNG TY
CỔ PHẦN KIẾN TRÚC
- XÂY DỰNG ĐỨC AN**

Địa chỉ:
60/10/2 Lâm Văn Bền - Phường
Tân Kiểng - Quận 7- TP.HCM

Công trình/ Project:

BINH DUONG HOTEL

Hạng mục/ Item:

**THIẾT KẾ
ĐIỆN NƯỚC**

Bản vẽ/ Drawing name:

**HỆ THỐNG CHIẾU
SÁNG-TẦNG LƯNG**

Chủ trì thiết kế/ Project manager:


KTS. Vũ Minh Lâm

Thiết kế/ Desginer:

KTS. Vũ Minh Lâm


Tỉ lệ/ Scale: 1/100 Ngày: 04/2025

Số bản vẽ: E2-202 No:

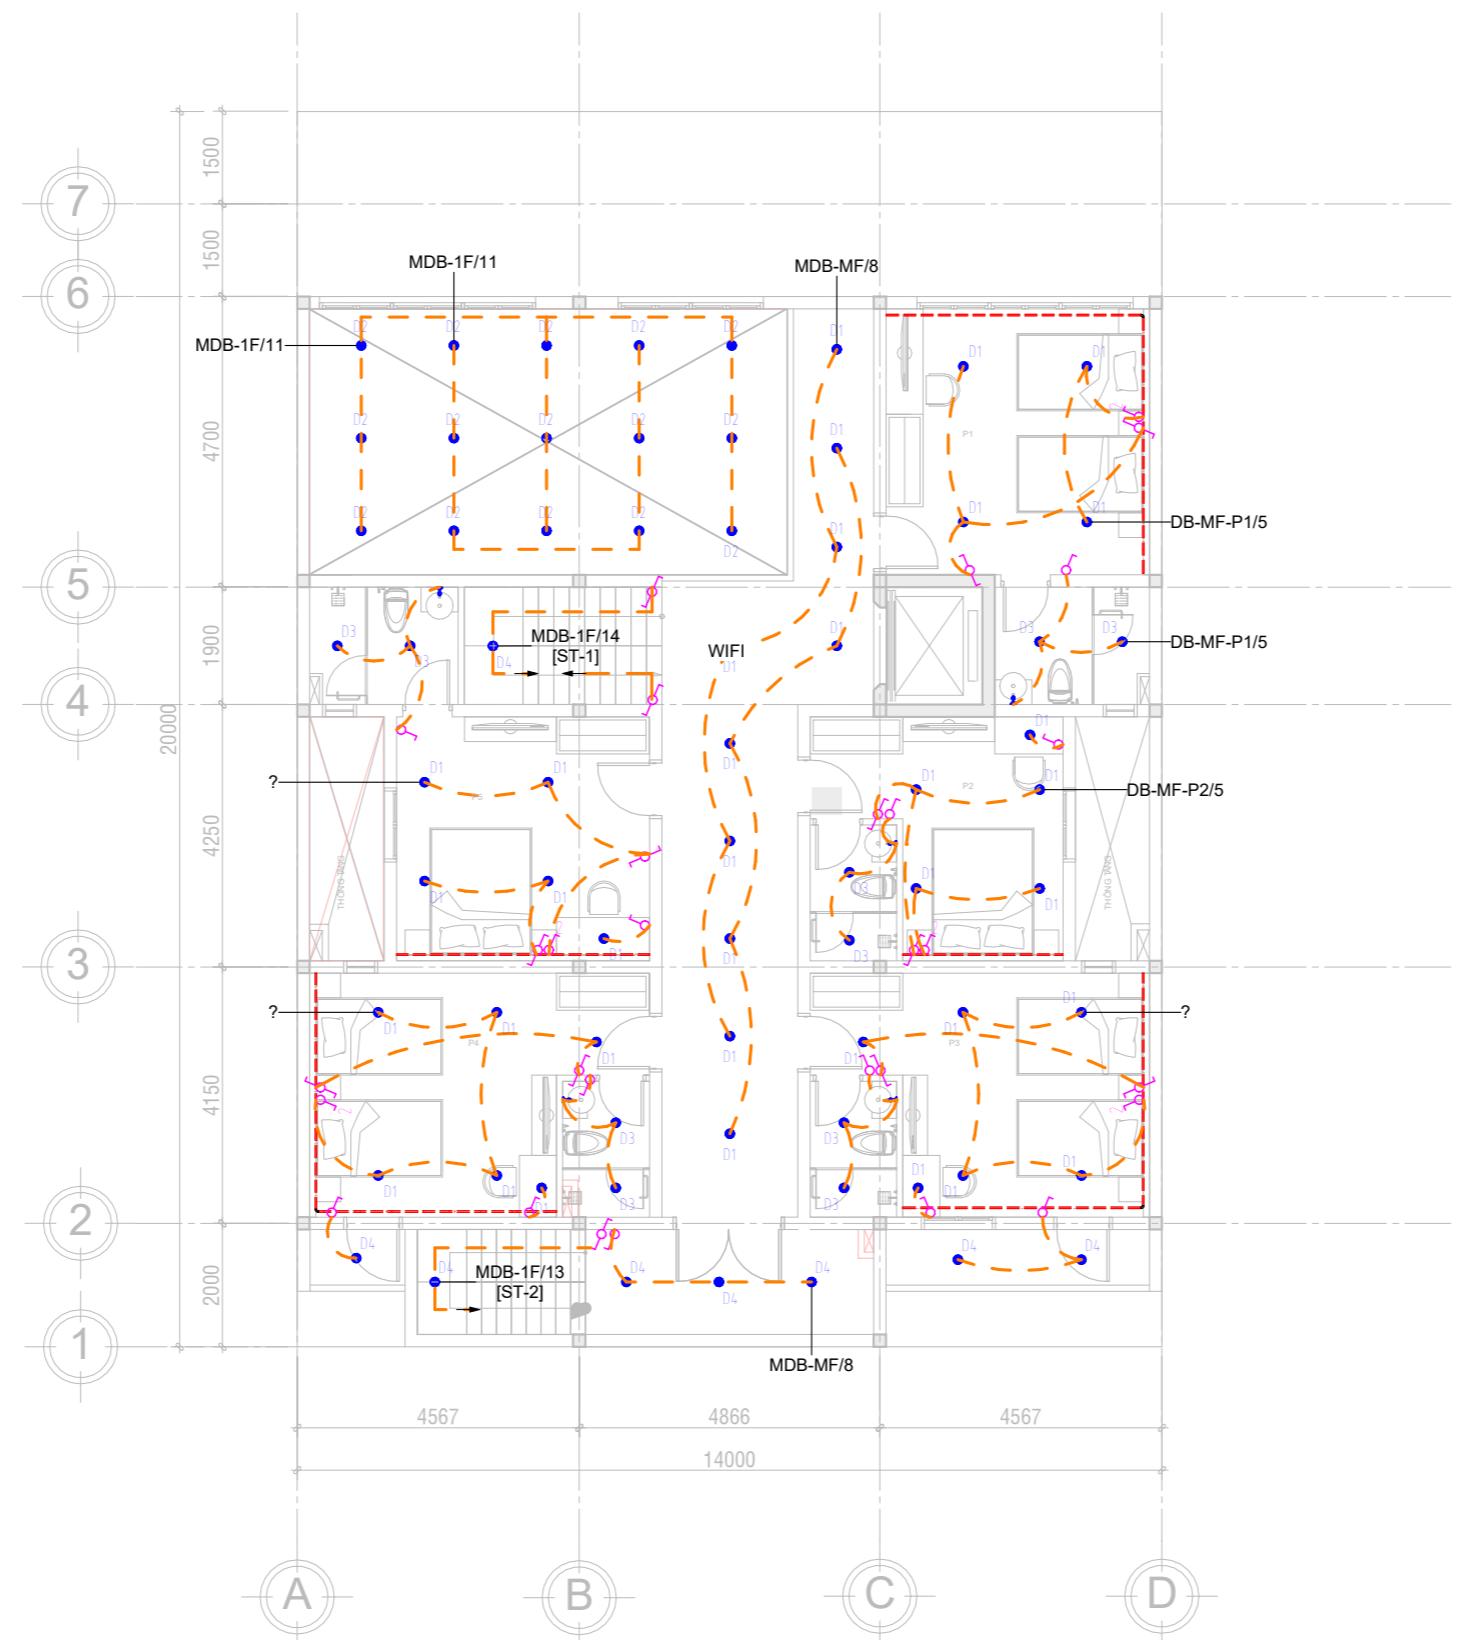

MẶT BẰNG TẦNG LƯNG
TL:1/100

Mục đích phát hành/Release status:
Thiết kế sơ/Preliminary:
Bản vẽ trình duyệt/For approval:
Bản vẽ tham khảo/For reference:
Bản vẽ thi công/For construction:
Bản vẽ hiệu chỉnh/Revising:
Bản vẽ hoàn công/As built:

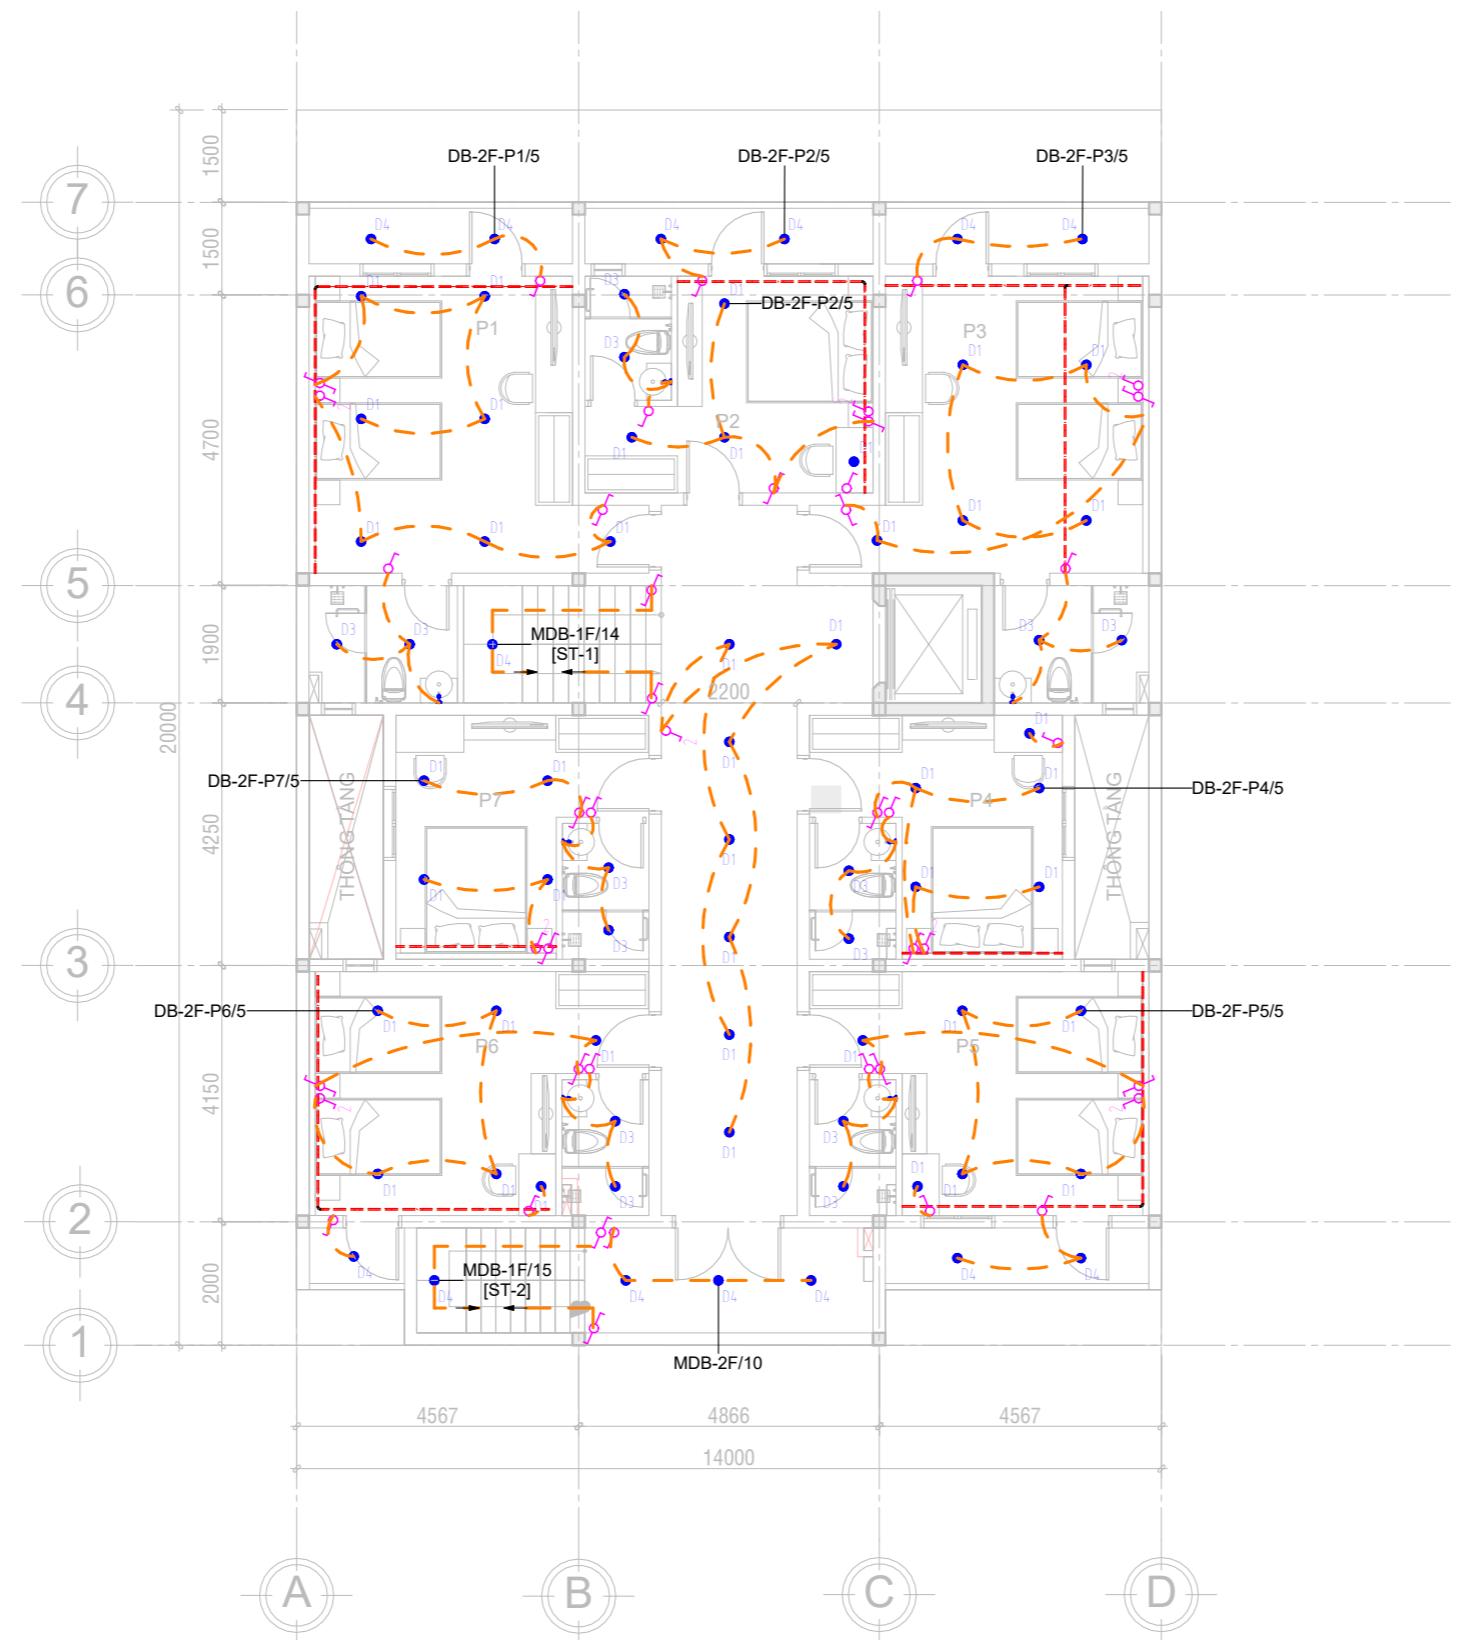

MẶT BẰNG TẦNG ĐIỆN HÌNH 2-6

TL:1/100

Đơn vị thiết kế - Thi công:

**CÔNG TY
CỔ PHẦN KIẾN TRÚC
- XÂY DỰNG ĐỨC AN**

Địa chỉ:
60/10/2 Lâm Văn Bền - Phường
Tân Kiểng - Quận 7- TP.HCM

Công trình/ Project:

BINH DUONG HOTEL

Hạng mục/ Item:

**THIẾT KẾ
ĐIỆN NƯỚC**

Bản vẽ/ Drawing name:

**HỆ THỐNG CHIẾU
SÁNG-TẦNG 2-6**

Chủ trì thiết kế/ Project manager:

KTS. Vũ Minh Lâm

Thiết kế/ Desginer:

KTS. Vũ Minh Lâm

Tỉ lệ/ Scale: 1/100 Ngày: 04/2025

Số bản vẽ: E2-203 No:

Mục đích phát hành/Release status:
Thiết kế sơ/Preliminary:
Bản vẽ trình duyệt/For approval:
Bản vẽ tham khảo/For reference:
Bản vẽ thi công/For construction:
Bản vẽ hiệu chỉnh/Revising:
Bản vẽ hoàn công/As built:

Đơn vị thiết kế - Thi công:

**CÔNG TY
CỔ PHẦN KIẾN TRÚC
- XÂY DỰNG ĐỨC AN**

Địa chỉ:
60/10/2 Lâm Văn Bền - Phường
Tân Kiểng - Quận 7 - TP.HCM

Công trình/ Project:

BINH DUONG HOTEL

Hạng mục/ Item:

**THIẾT KẾ
ĐIỆN NƯỚC**

Bản vẽ/ Drawing name:

**HỆ THỐNG CHIẾU
SÁNG-TẦNG SÂN
THƯỢNG**

Chủ trì thiết kế/ Project manager:


KTS. Vũ Minh Lâm

Thiết kế/ Desginer:

KTS. Vũ Minh Lâm

Tỉ lệ/ Scale: 1/100 Ngày: 04/2025

Số bản vẽ: E2-204 №:

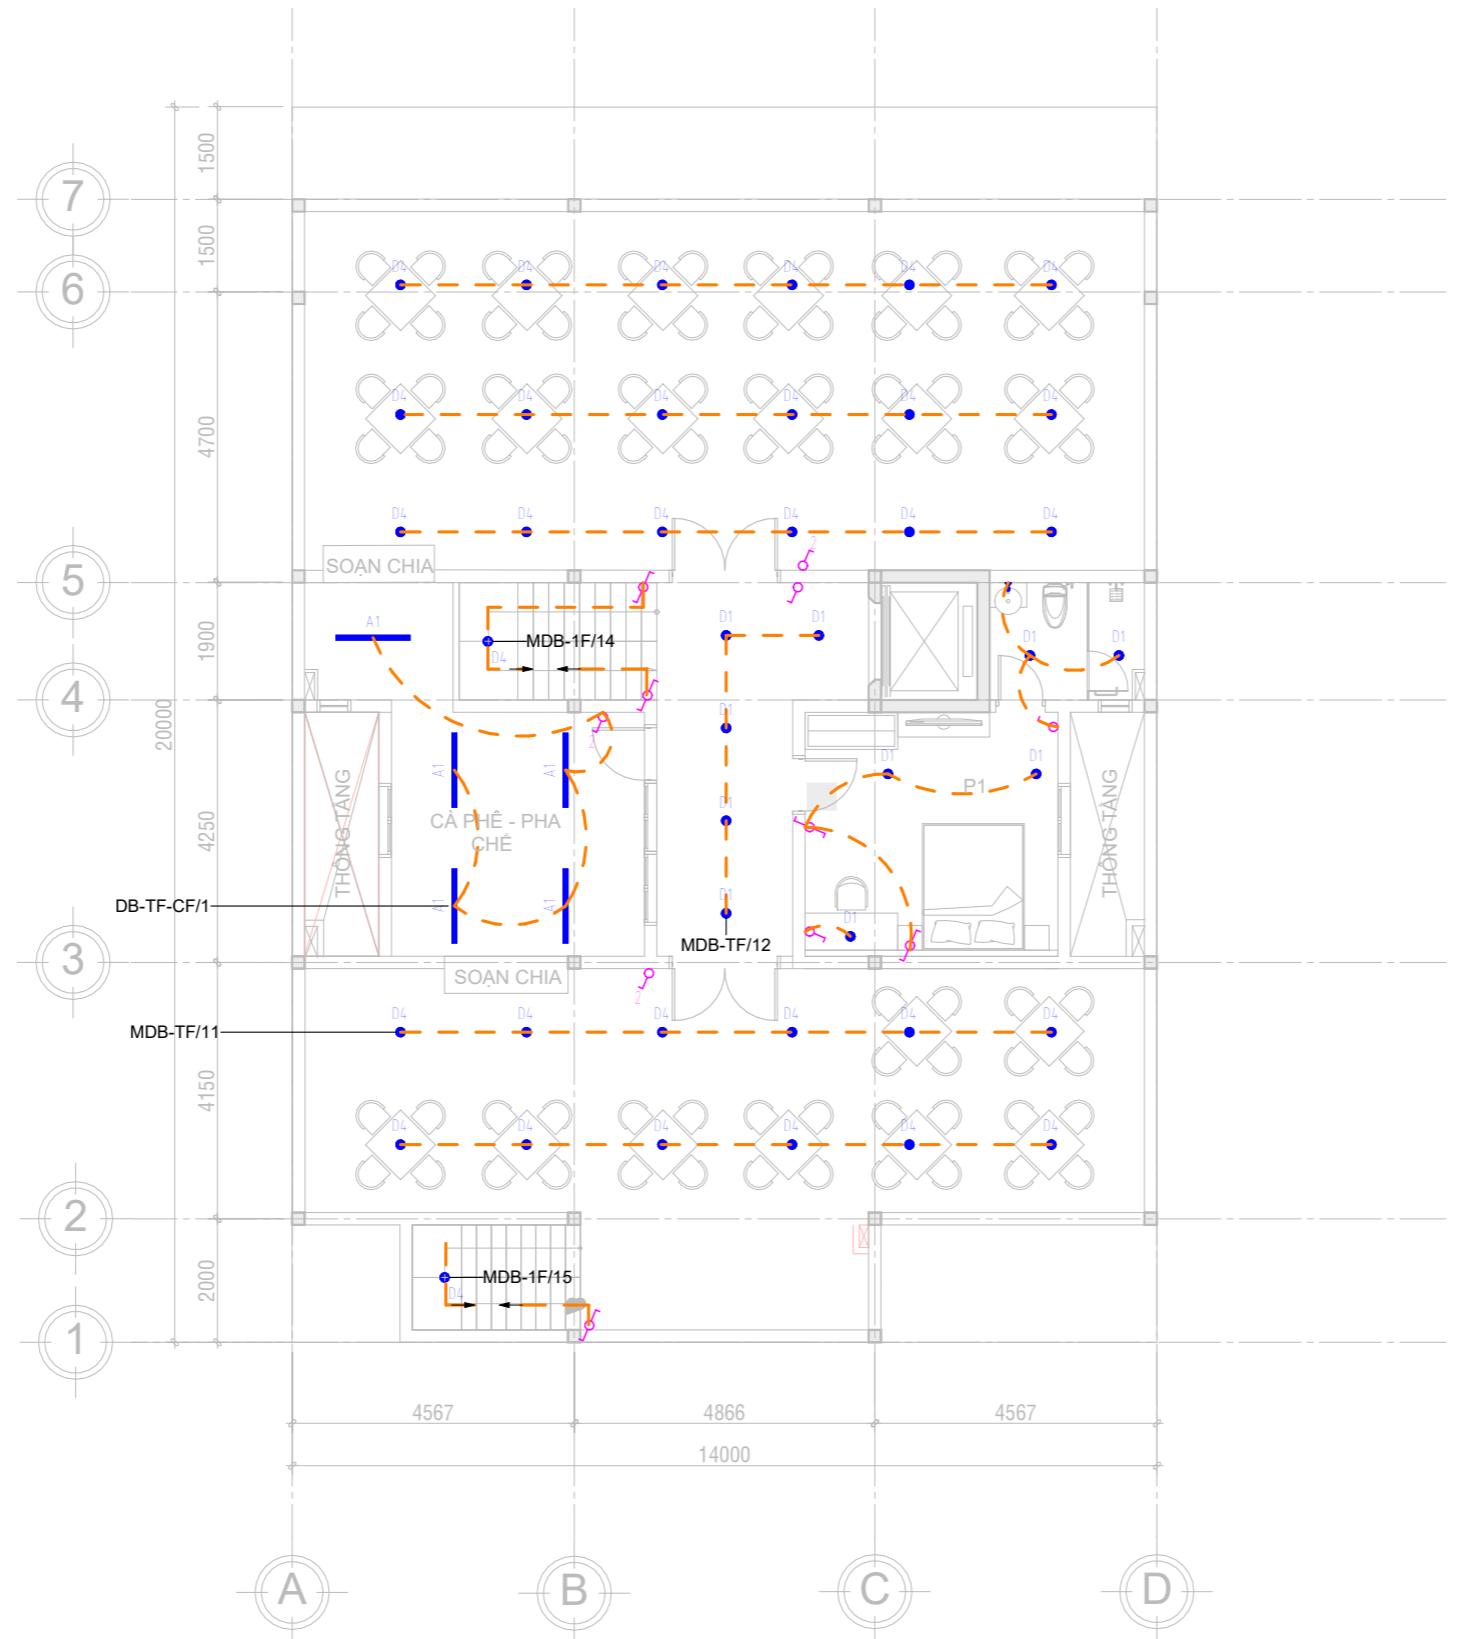

MẶT BẰNG TẦNG SÂN THƯỢNG

TL:1/100

Mục đích phát hành/Release status:	
Thiết kế sơ/Preliminary:	
Bản vẽ trình duyệt/For approval:	
Bản vẽ tham khảo/For reference:	
Bản vẽ thi công/For construction:	<input checked="" type="checkbox"/>
Bản vẽ hiệu chỉnh/Revising:	
Bản vẽ hoàn công/As built:	

Đơn vị thiết kế - Thi công:

**CÔNG TY
CỔ PHẦN KIẾN TRÚC
- XÂY DỰNG ĐỨC AN**

Địa chỉ:
60/10/2 Lâm Văn Bền - Phường
Tân Kiểng - Quận 7- TP.HCM

Công trình/ Project:

BINH DUONG HOTEL

Hạng mục/ Item:

**THIẾT KẾ
ĐIỆN NƯỚC**

Bản vẽ/ Drawing name:

**HỆ THỐNG MẠNG,
CAMERA-TẦNG 1**

Chủ trì thiết kế/ Project manager:

KTS. Vũ Minh Lâm

Thiết kế/ Desginer:

KTS. Vũ Minh Lâm

Tỉ lệ/ Scale: 1/100 Ngày: 04/2025

Số bản vẽ: E3-201 No:



MẶT BẰNG TẦNG 1

TL-1/100

Mục đích phát hành/Release status:
Thiết kế sơ/Preliminary:
Bản vẽ trình duyệt/For approval:
Bản vẽ tham khảo/For reference:
Bản vẽ thi công/For construction:
Bản vẽ hiệu chỉnh/Revising:
Bản vẽ hoàn công/As built:

Đơn vị thiết kế - Thi công:

**CÔNG TY
CỔ PHẦN KIẾN TRÚC
- XÂY DỰNG ĐỨC AN**

Địa chỉ:
60/10/2 Lâm Văn Bền - Phường
Tân Kiểng - Quận 7- TP.HCM

Công trình/ Project:

BINH DUONG HOTEL

Hạng mục/ Item:

**THIẾT KẾ
ĐIỆN NƯỚC**

Bản vẽ/ Drawing name:

**HỆ THỐNG MẠNG,
CAMERA-TẦNG LƯNG**

Chủ trì thiết kế/ Project manager:


KTS. Vũ Minh Lâm

Thiết kế/ Desginer:

KTS. Vũ Minh Lâm

Tỉ lệ/ Scale: 1/100 Ngày: 04/2025

Số bản vẽ: E3-202 No:

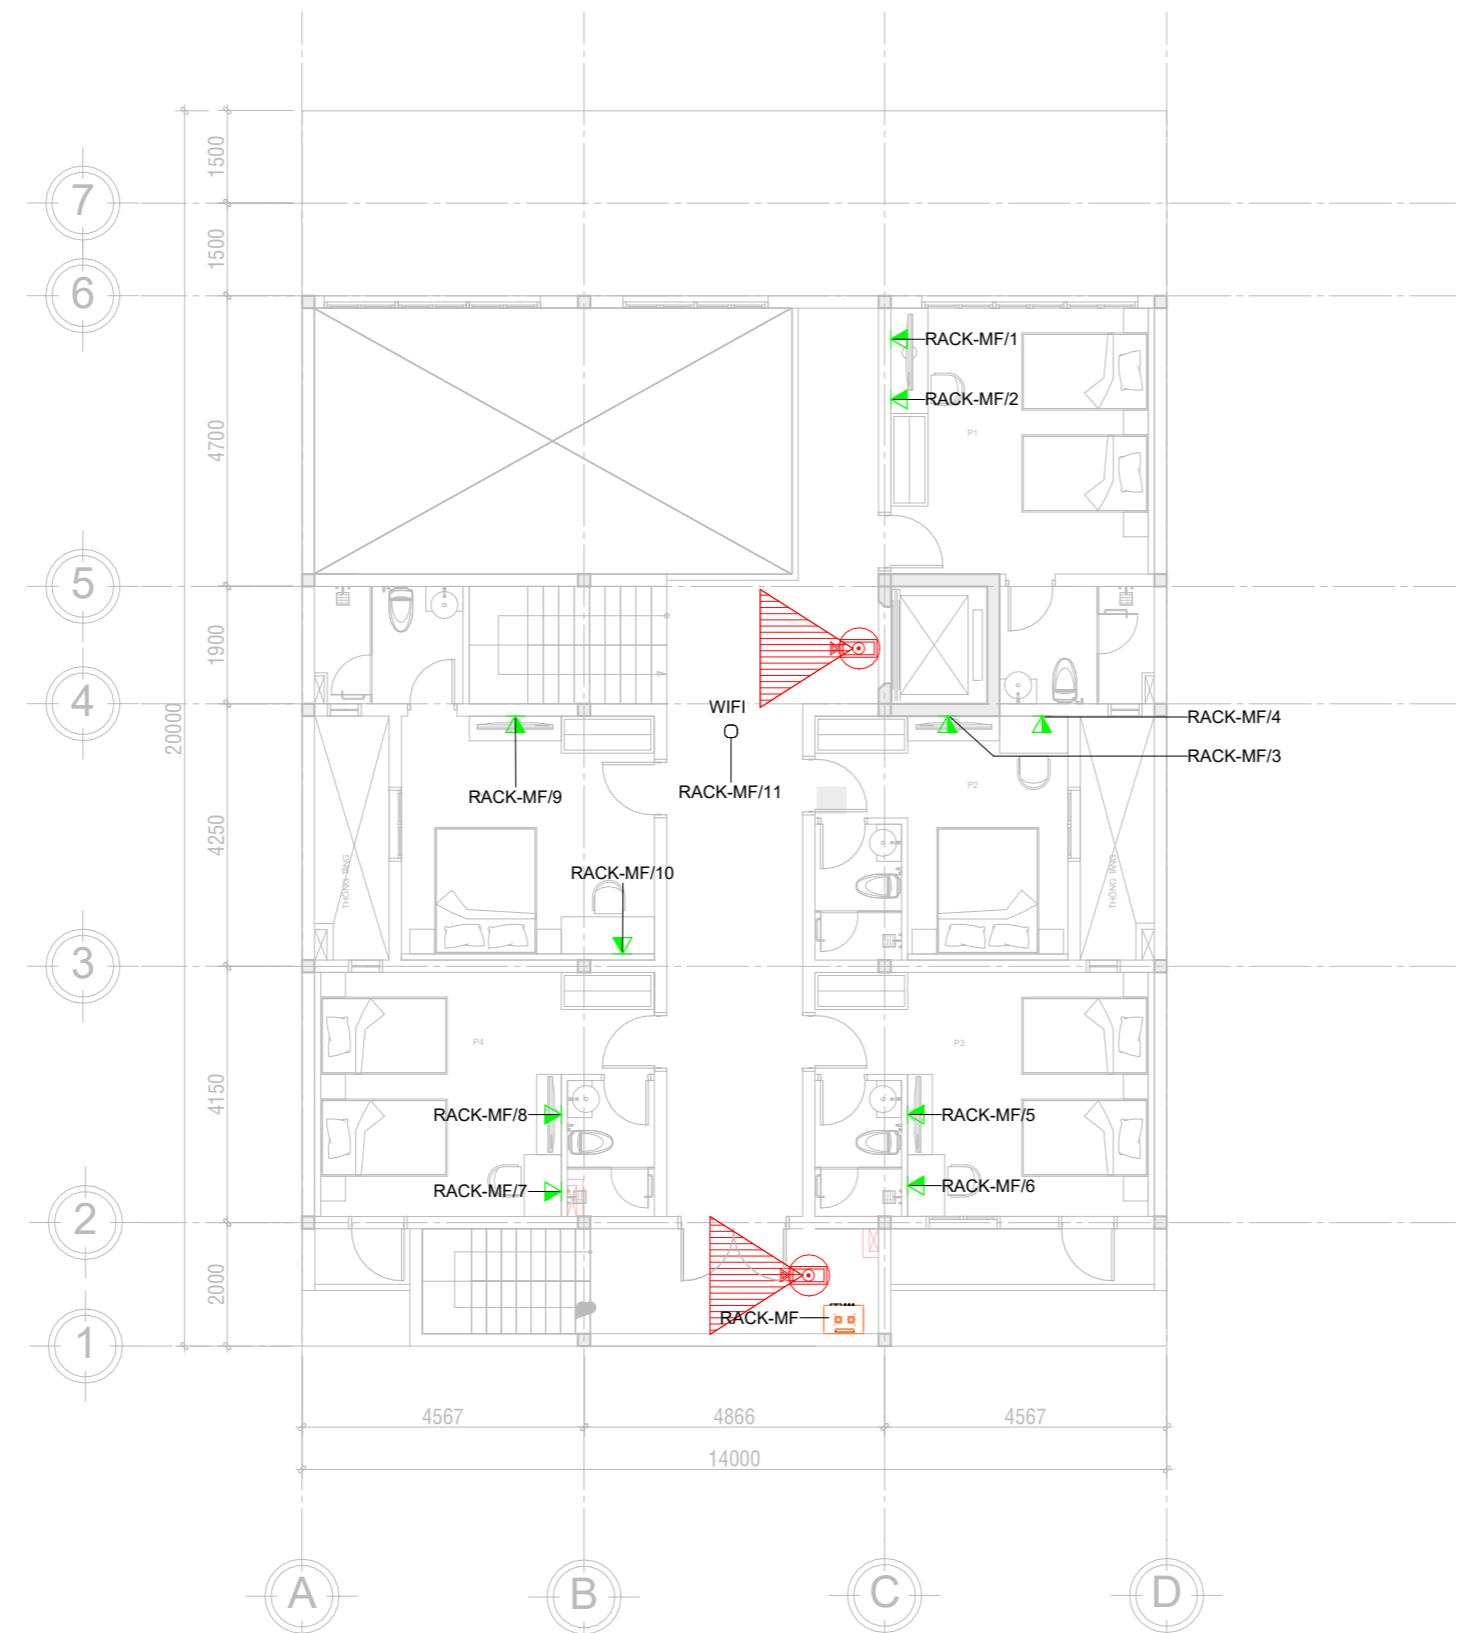

MẶT BẰNG TẦNG LƯNG

TL:1/100

Mục đích phát hành/Release status:
Thiết kế sơ/Preliminary:
Bản vẽ trình duyệt/For approval:
Bản vẽ tham khảo/For reference:
Bản vẽ thi công/For construction:
Bản vẽ hiệu chỉnh/Revising:
Bản vẽ hoàn công/As built:

Đơn vị thiết kế - Thi công:

**CÔNG TY
CỔ PHẦN KIẾN TRÚC
- XÂY DỰNG ĐỨC AN**

Địa chỉ:

60/10/2 Lâm Văn Bền - Phường
Tân Kiểng - Quận 7- TP.HCM

Công trình/ Project:

BINH DUONG HOTEL

Hạng mục/ Item:

**THIẾT KẾ
ĐIỆN NƯỚC**

Bản vẽ/ Drawing name:

**HỆ THỐNG MẠNG,
CAMERA-TẦNG 2-6**

Chủ trì thiết kế/ Project manager:

KTS. Vũ Minh Lâm

Thiết kế/ Desginer:

KTS. Vũ Minh Lâm

Tỉ lệ/ Scale: 1/100 Ngày: 04/2025

Số bản vẽ: E3-203 No:



MẶT BẰNG TẦNG ĐIỆN HÌNH 2-6

TL:1/100

Mục đích phát hành/Release status:
Thiết kế sơ/Preliminary:
Bản vẽ trình duyệt/For approval:
Bản vẽ tham khảo/For reference:
Bản vẽ thi công/For construction:
Bản vẽ hiệu chỉnh/Revising:
Bản vẽ hoàn công/As built:

Đơn vị thiết kế - Thi công:

**CÔNG TY
CỔ PHẦN KIẾN TRÚC
- XÂY DỰNG ĐỨC AN**

Địa chỉ:

60/10/2 Lâm Văn Bền - Phường
Tân Kiểng - Quận 7- TP.HCM

Công trình/ Project:

BINH DUONG HOTEL

Hạng mục/ Item:

**THIẾT KẾ
ĐIỆN NƯỚC**

Bản vẽ/ Drawing name:

**HỆ THỐNG MẠNG,
CAMERA-TẦNG SÂN
THƯỢNG**

Chủ trì thiết kế/ Project manager:


KTS. Vũ Minh Lâm

Thiết kế/ Desginer:

KTS. Vũ Minh Lâm

Tỉ lệ/ Scale: 1/100 Ngày: 04/2025


Số bản vẽ: E3-204 No:

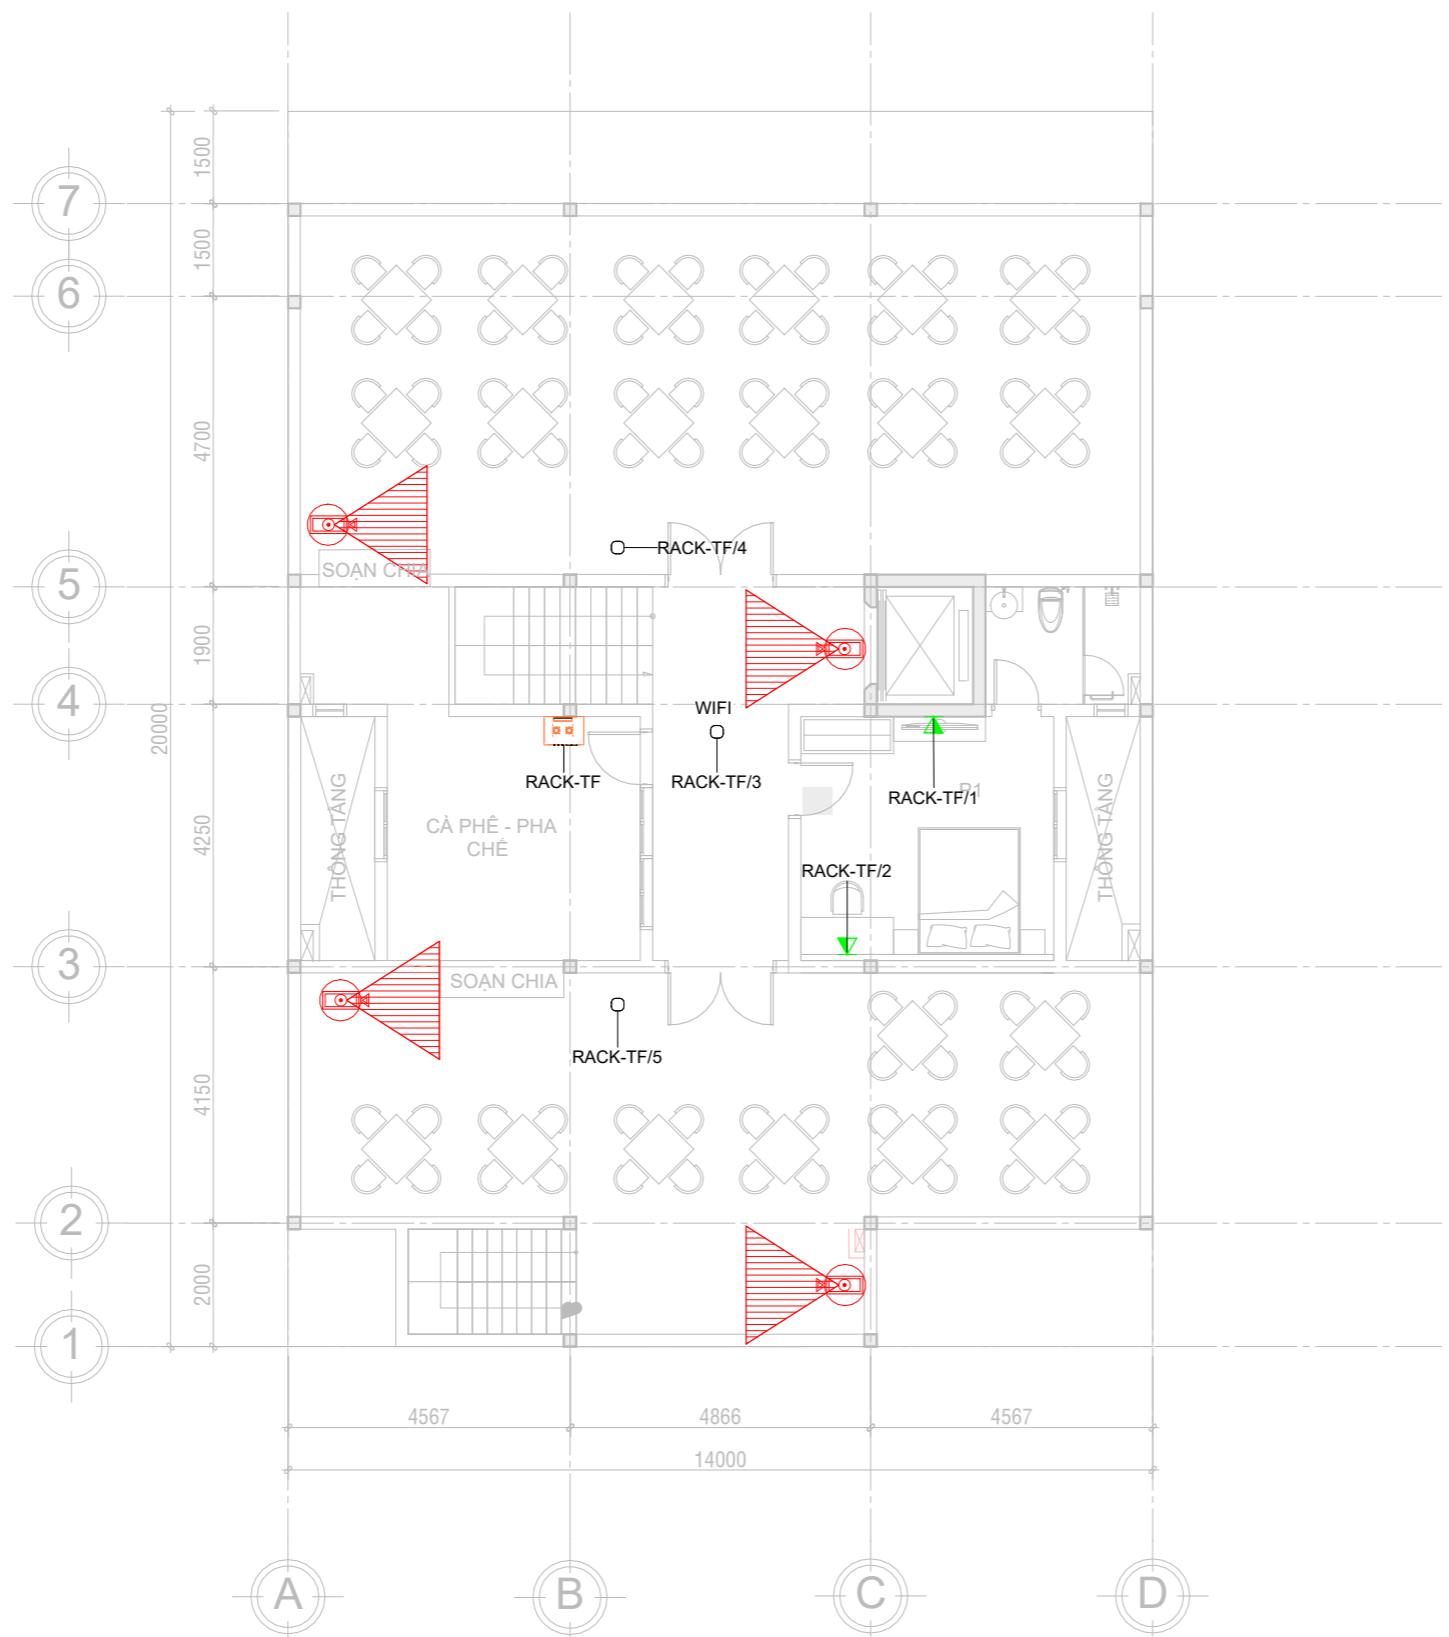

MẶT BẰNG TẦNG SÂN THƯỢNG

TL:1/100

Mục đích phát hành/Release status:
Thiết kế sơ/Preliminary:
Bản vẽ trình duyệt/For approval:
Bản vẽ tham khảo/For reference:
Bản vẽ thi công/For construction:
Bản vẽ hiệu chỉnh/Revising:
Bản vẽ hoàn công/As built:

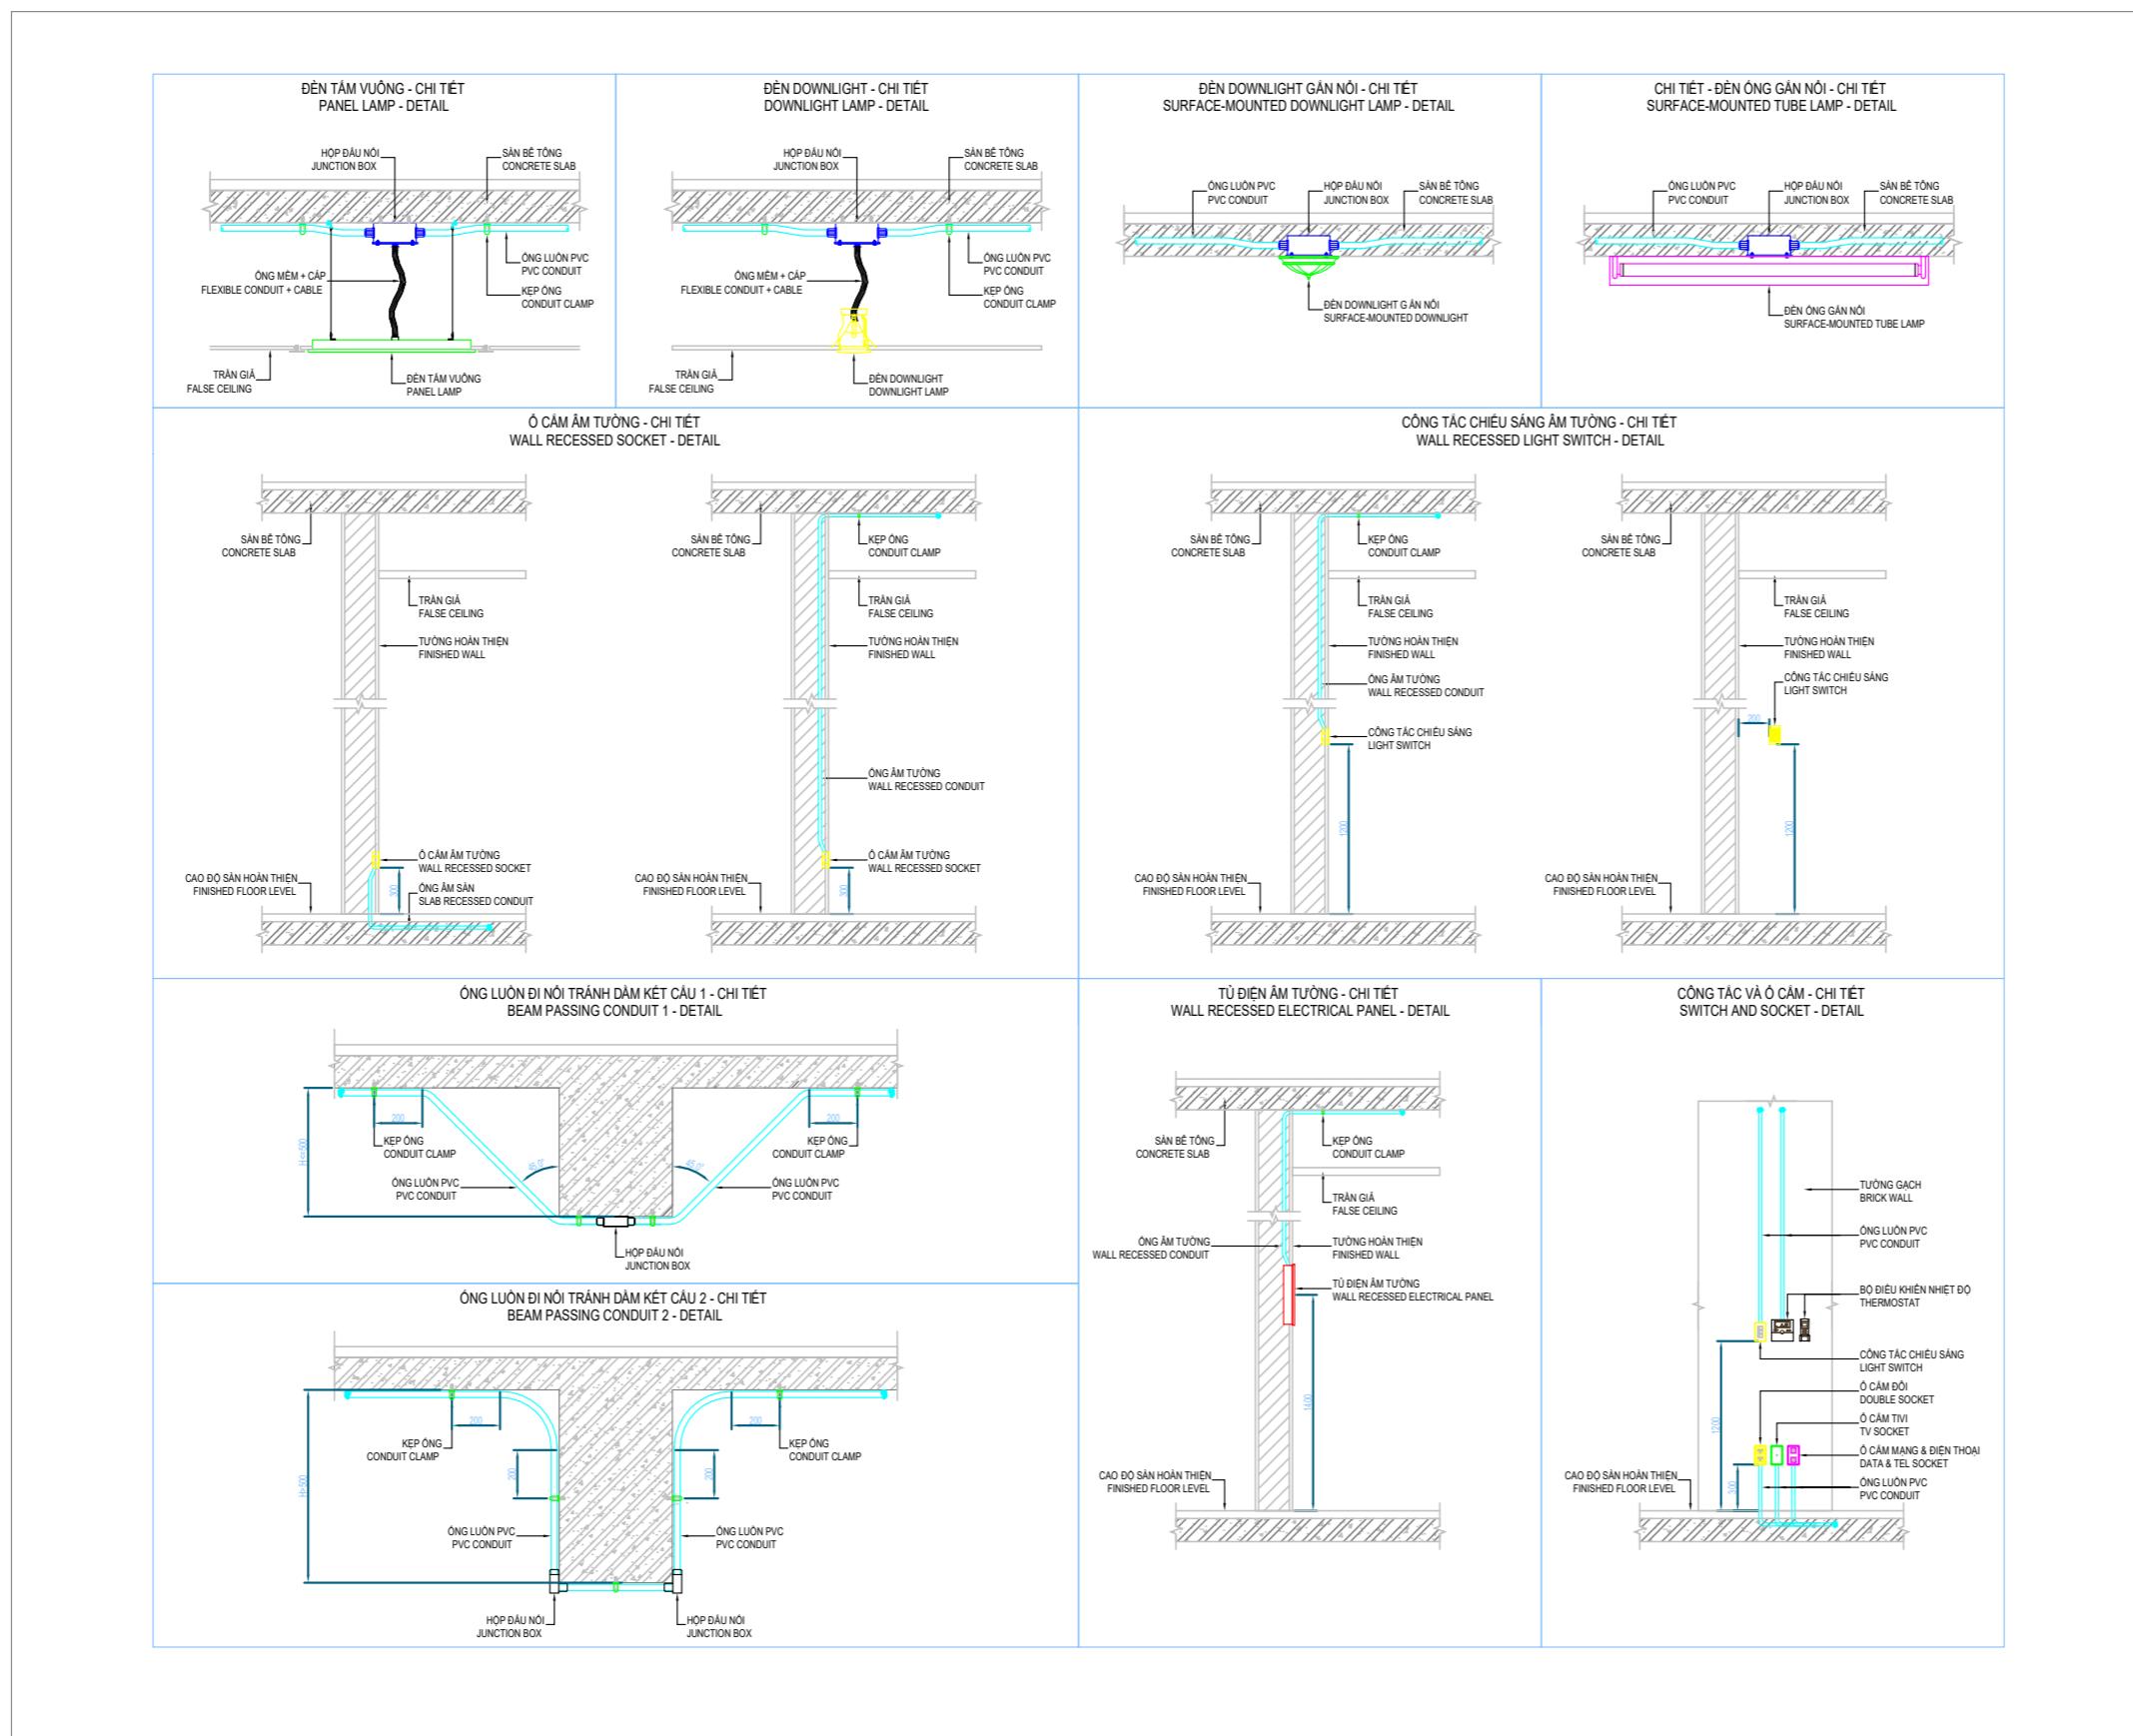

Đơn vị thiết kế - Thi công:

**CÔNG TY
CỔ PHẦN KIẾN TRÚC
- XÂY DỰNG ĐỨC AN**

Địa chỉ:
60/10/2 Lâm Văn Bền - Phường
Tân Kiểng - Quận 7 - TP.HCM

Công trình/ Project:

BINH DUONG HOTEL

Hạng mục/ Item:

**THIẾT KẾ
ĐIỆN NƯỚC**

Bản vẽ/ Drawing name:

**CHI TIẾP LẮP ĐẶT ĐIỆN
1**

Chủ trì thiết kế/ Project manager:

KTS. Vũ Minh Lâm


Thiết kế/ Desginer:

KTS. Vũ Minh Lâm

Tỉ lệ/ Scale: 1/100 Ngày: 04/2025

Số bản vẽ: E4-401 No:

Mục đích phát hành/Release status:
Thiết kế sơ/Preliminary:
Bản vẽ trình duyệt/For approval:
Bản vẽ tham khảo/For reference:
Bản vẽ thi công/For construction:
Bản vẽ hiệu chỉnh/Revising:
Bản vẽ hoàn công/As built:

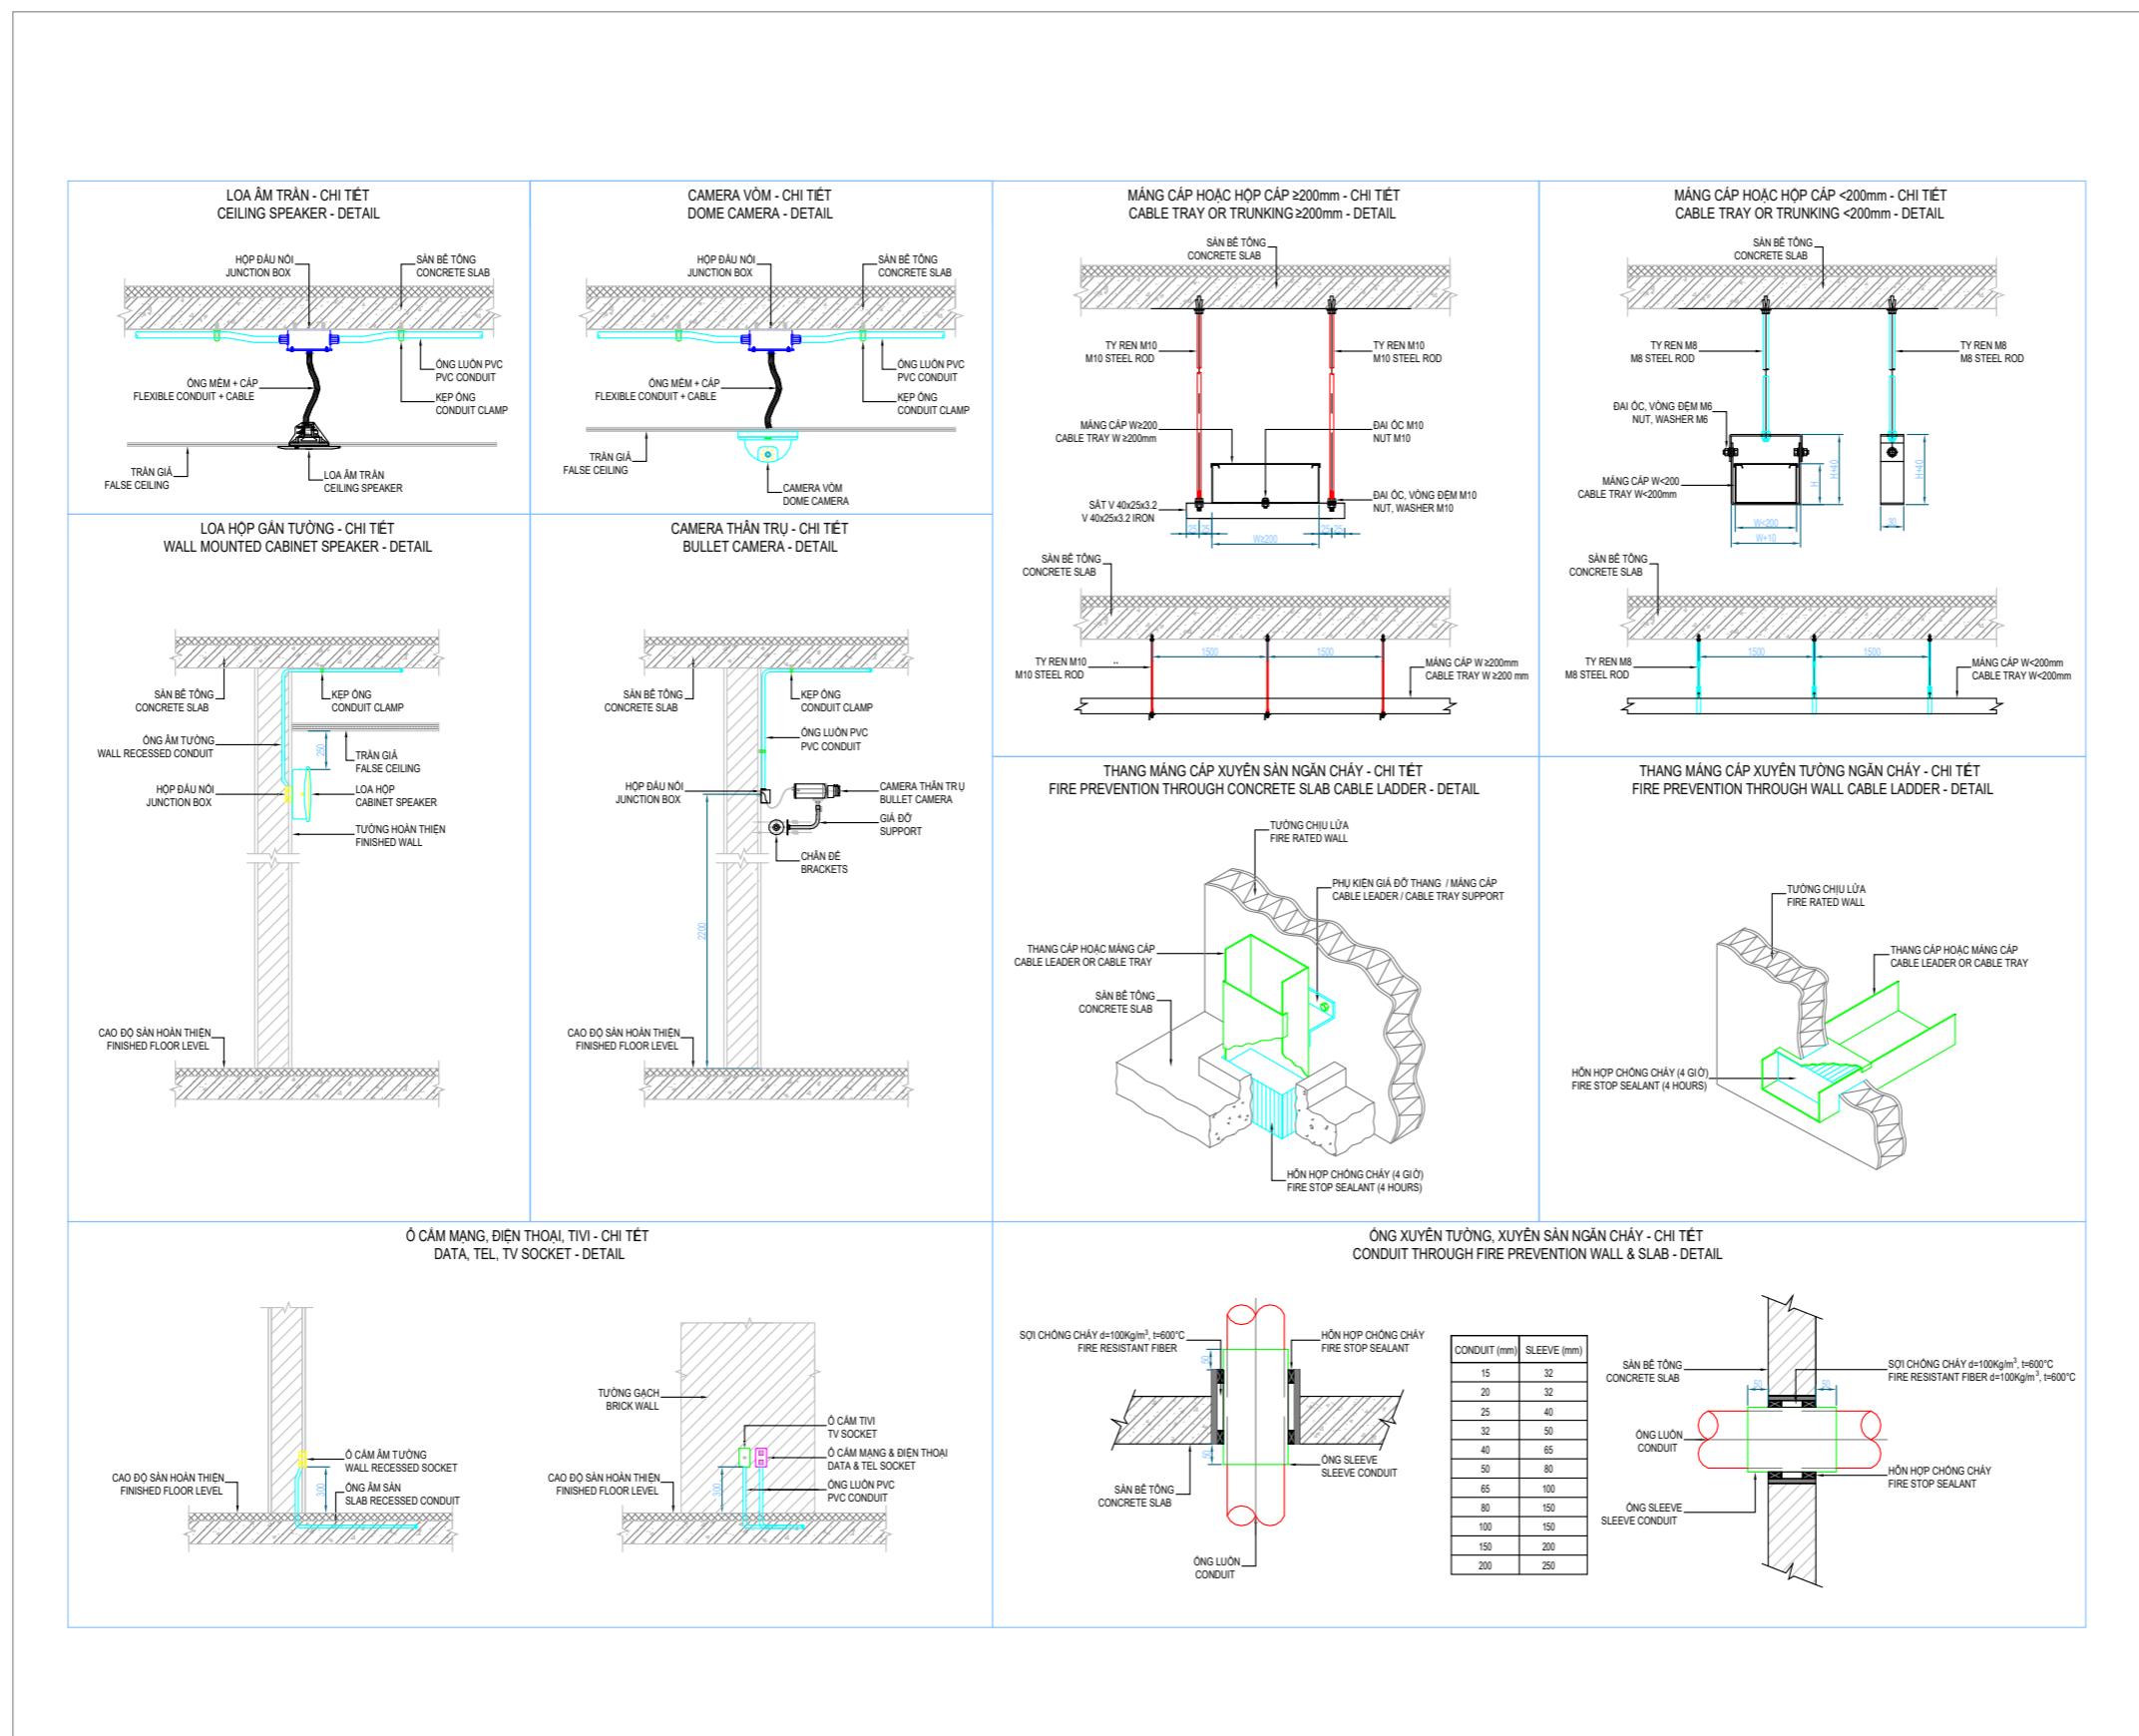

Đơn vị thiết kế - Thi công:

**CÔNG TY
CỔ PHẦN KIẾN TRÚC
- XÂY DỰNG ĐỨC AN**

Địa chỉ:
60/10/2 Lâm Văn Bền - Phường
Tân Kiểng - Quận 7- TP.HCM

Công trình/ Project:

BINH DUONG HOTEL

Hạng mục/ Item:

**THIẾT KẾ
ĐIỆN NƯỚC**

Bản vẽ/ Drawing name:

**CHI TIẾT LẮP ĐẶT ĐIỆN
2**

Chủ trì thiết kế/ Project manager:

KTS. Vũ Minh Lâm

Thiết kế/ Desginer:

KTS. Vũ Minh Lâm

Tỉ lệ/ Scale: 1/100	Ngày: 04/2025
Số bản vẽ: E4-402	No:

Mục đích phát hành/Release status:
Thiết kế sơ/Preliminary:
Bản vẽ trình duyệt/For approval:
Bản vẽ tham khảo/For reference:
Bản vẽ thi công/For construction:
Bản vẽ hiệu chỉnh/Revising:
Bản vẽ hoàn công/As built:

Đơn vị thiết kế - Thi công:

**CÔNG TY
CỔ PHẦN KIẾN TRÚC
- XÂY DỰNG ĐỨC AN**

Địa chỉ:

60/10/2 Lâm Văn Bền - Phường
Tân Kiểng - Quận 7- TP.HCM

Công trình/ Project:

BINH DUONG HOTEL

Hạng mục/ Item:

**THIẾT KẾ
ĐIỆN NƯỚC**

Bản vẽ/ Drawing name:

**HỆ THỐNG ĐHKK-TẦNG
1**

Chủ trì thiết kế/ Project manager:


KTS. Vũ Minh Lâm

Thiết kế/ Desginer:

KTS. Vũ Minh Lâm

Tỉ lệ/ Scale: 1/100 Ngày: 04/2025

Số bản vẽ: M-201 No:

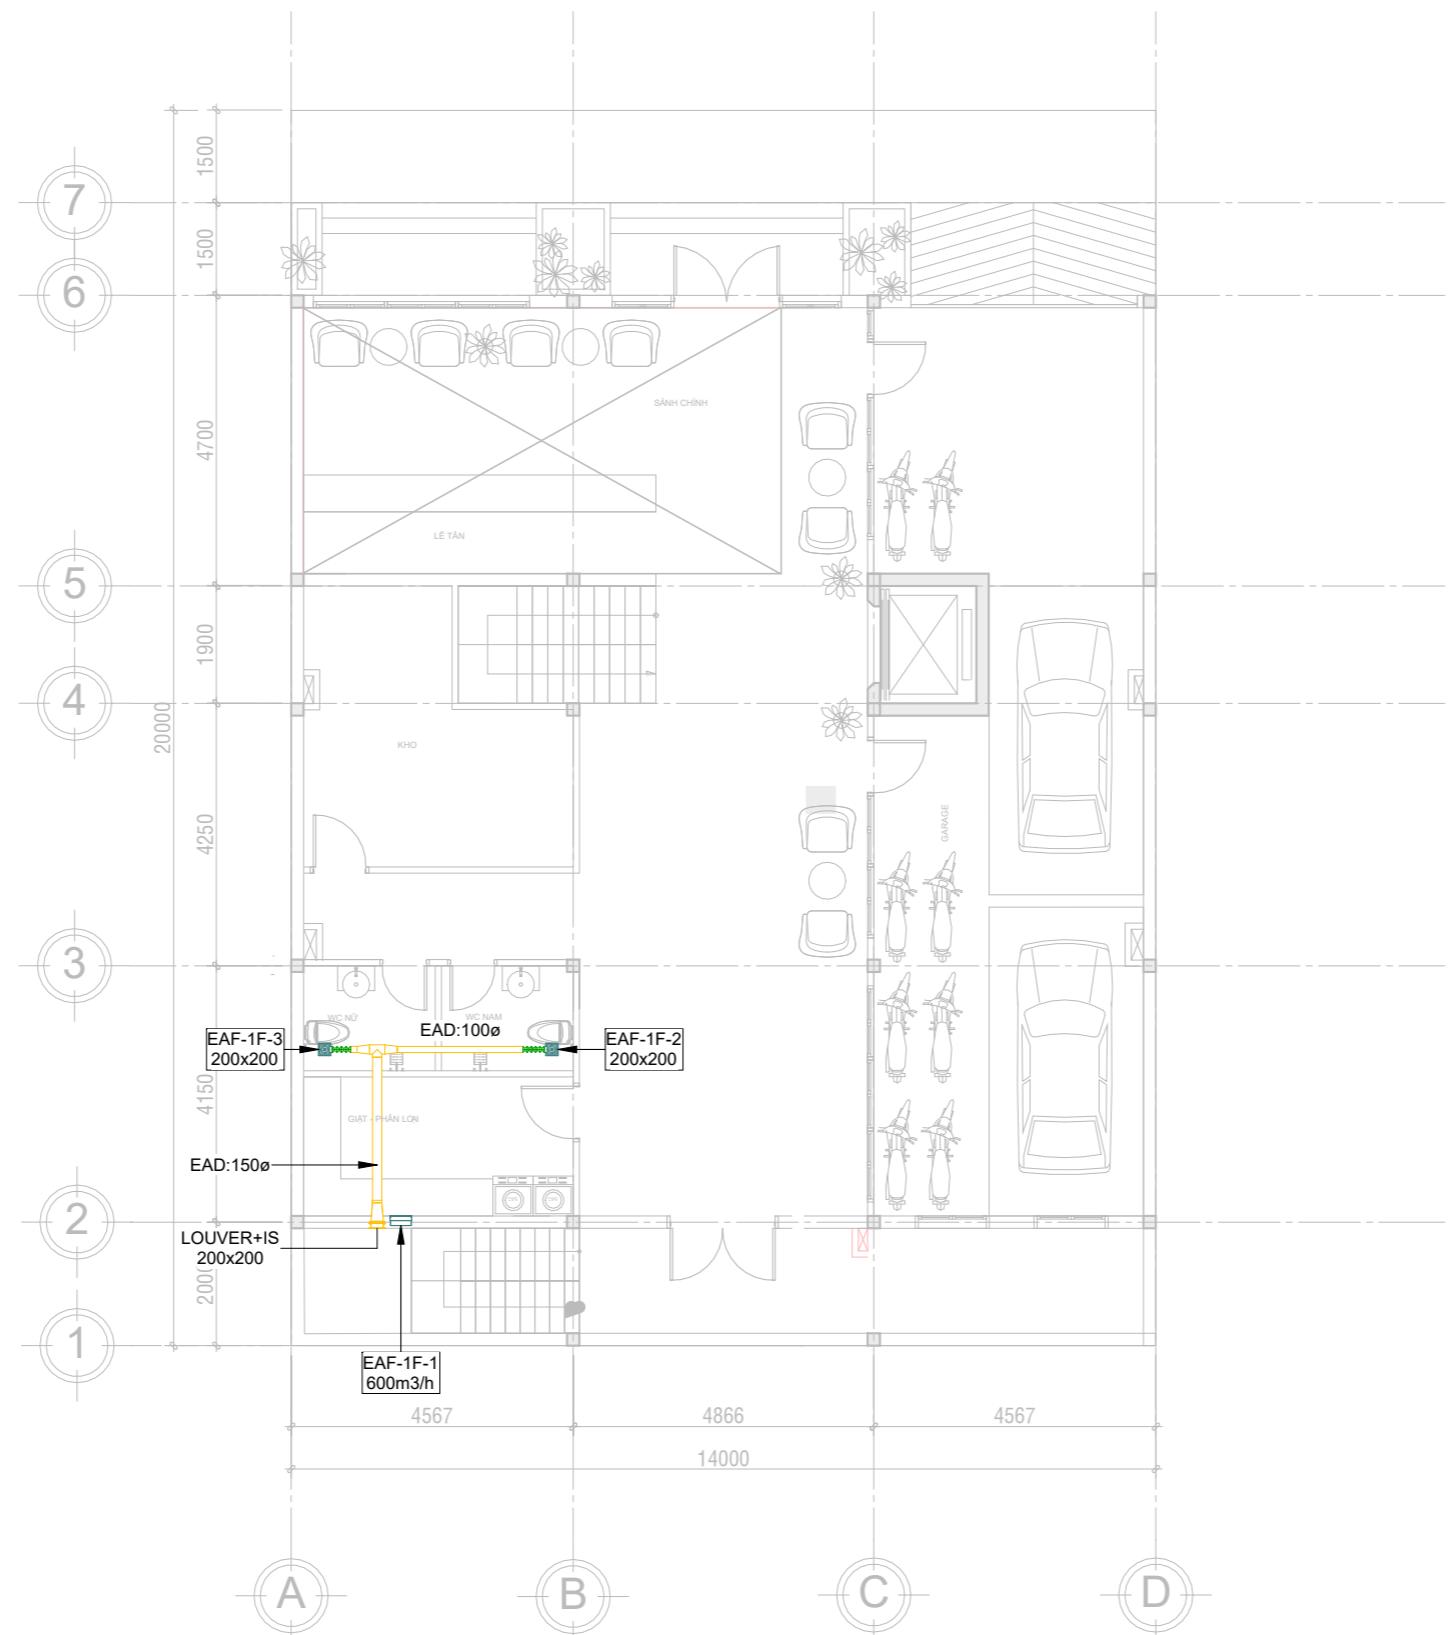

MẶT BẰNG TẦNG 1

Tl:1/100

Mục đích phát hành/Release status:
Thiết kế sơ/Preliminary:
Bản vẽ trình duyệt/For approval:
Bản vẽ tham khảo/For reference:
Bản vẽ thi công/For construction:
Bản vẽ hiệu chỉnh/Revising:
Bản vẽ hoàn công/As built:

Đơn vị thiết kế - Thi công:

**CÔNG TY
CỔ PHẦN KIẾN TRÚC
- XÂY DỰNG ĐỨC AN**

Địa chỉ:
60/10/2 Lâm Văn Bền - Phường
Tân Kiểng - Quận 7- TP.HCM

Công trình/ Project:

BINH DUONG HOTEL

Hạng mục/ Item:

**THIẾT KẾ
ĐIỆN NƯỚC**

Bản vẽ/ Drawing name:

**HỆ THỐNG ĐHKK-TẦNG
LƯNG**

Chủ trì thiết kế/ Project manager:


KTS. Vũ Minh Lâm

Thiết kế/ Desginer:

KTS. Vũ Minh Lâm

Tỉ lệ/ Scale: 1/100 Ngày: 04/2025

Số bản vẽ: M-202 No:

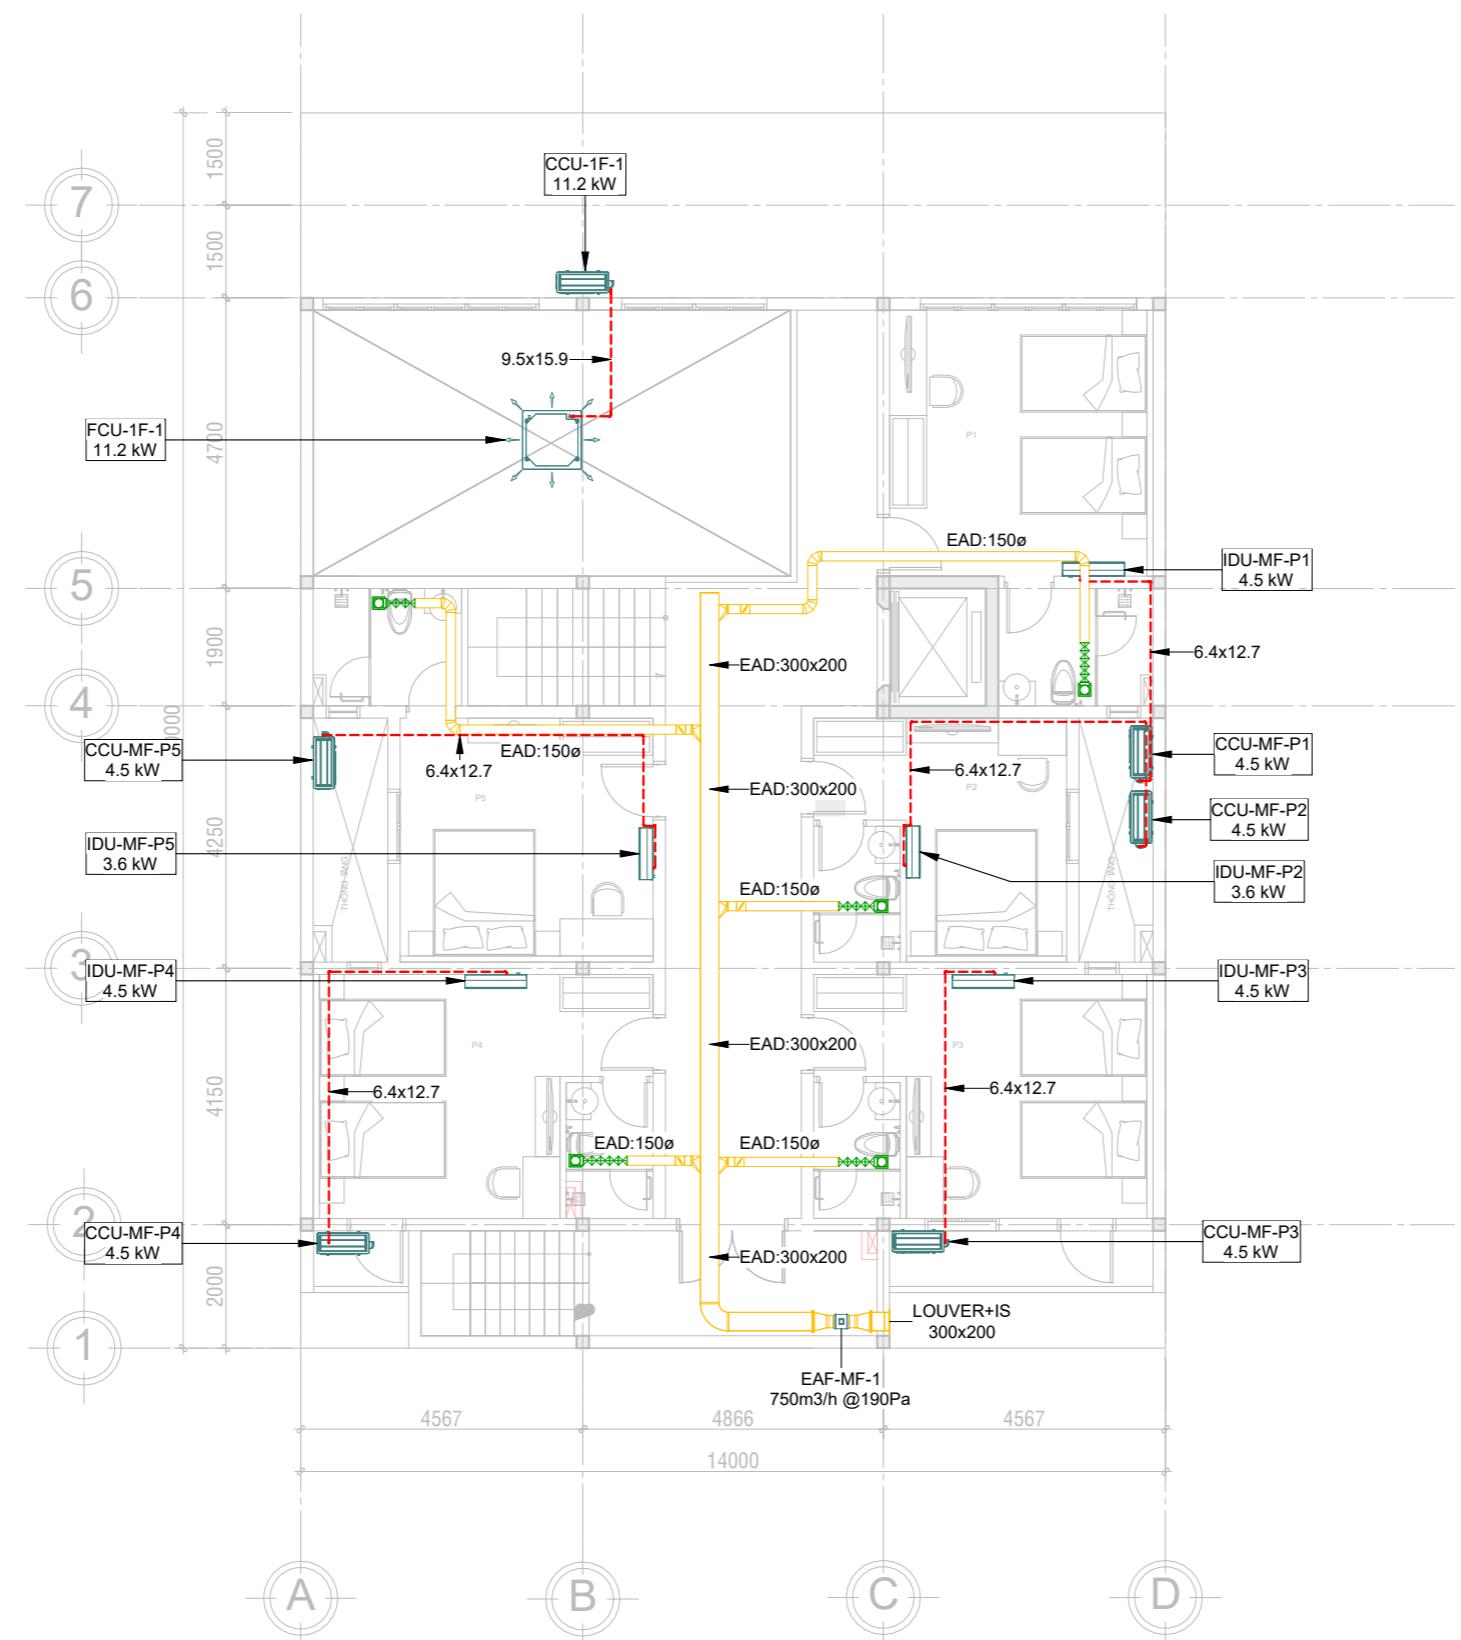

MẶT BẰNG TẦNG LƯNG

TL:1/100

Mục đích phát hành/Release status:
Thiết kế sơ/Preliminary:
Bản vẽ trình duyệt/For approval:
Bản vẽ tham khảo/For reference:
Bản vẽ thi công/For construction:
Bản vẽ hiệu chỉnh/Revising:
Bản vẽ hoàn công/As built:

Đơn vị thiết kế - Thi công:

**CÔNG TY
CỔ PHẦN KIẾN TRÚC
- XÂY DỰNG ĐỨC AN**

Địa chỉ:
60/10/2 Lâm Văn Bền - Phường
Tân Kiểng - Quận 7 - TP.HCM

Công trình/ Project:

BINH DUONG HOTEL

Hạng mục/ Item:

**THIẾT KẾ
ĐIỆN NƯỚC**

Bản vẽ/ Drawing name:

**HỆ THỐNG ĐHKK-TẦNG
2-6**

Chủ trì thiết kế/ Project manager:


KTS. Vũ Minh Lâm

Thiết kế/ Desginer:

KTS. Vũ Minh Lâm

Tỉ lệ/ Scale: 1/100 Ngày: 04/2025

Số bản vẽ: M-203 No:

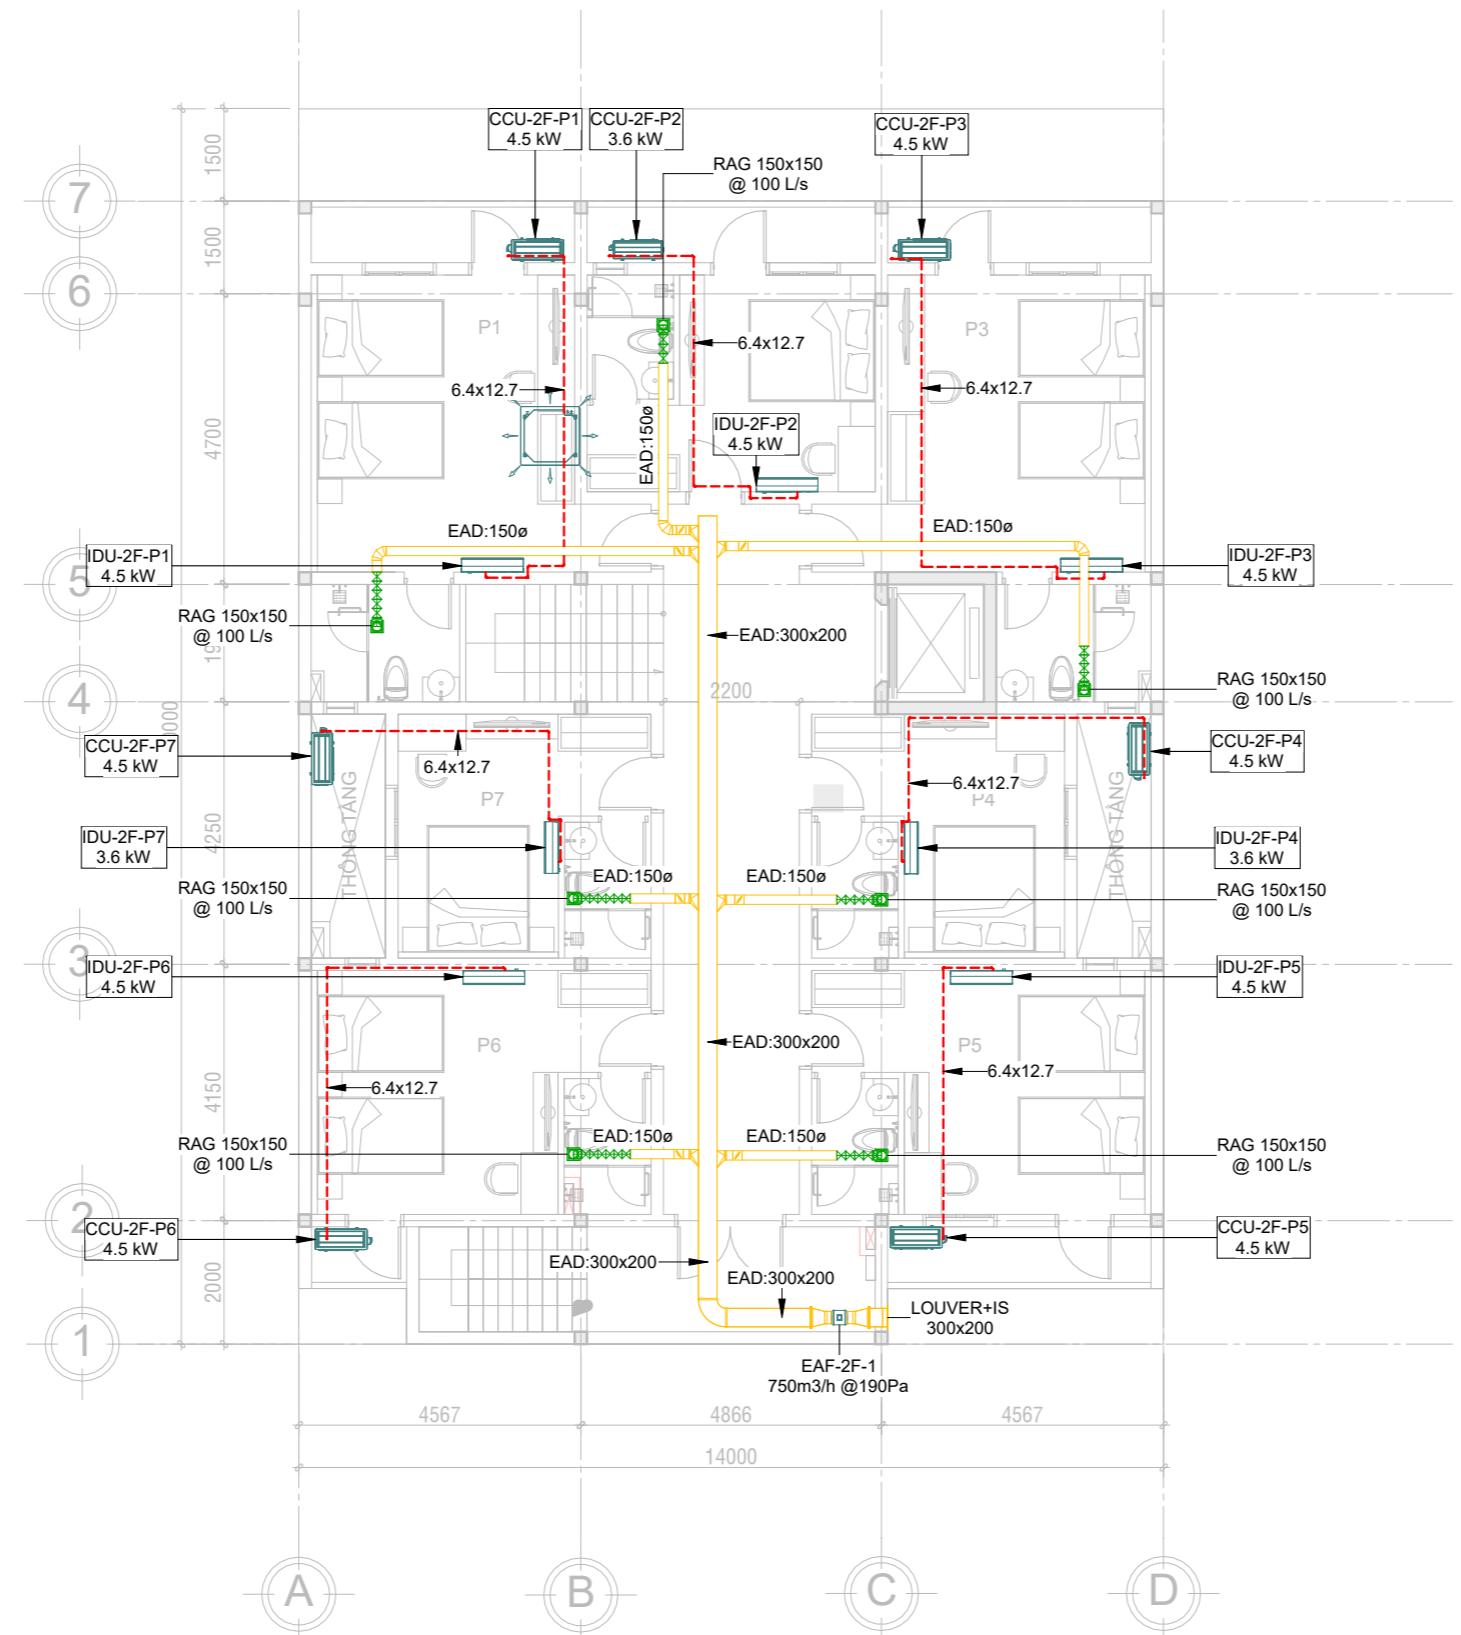

MẶT BẰNG TẦNG ĐIỂN HÌNH 2-6

TL:1/100

Mục đích phát hành/Release status:	
Thiết kế sơ/Preliminary:	
Bản vẽ trình duyệt/For approval:	
Bản vẽ tham khảo/For reference:	
Bản vẽ thi công/For construction:	<input checked="" type="checkbox"/>
Bản vẽ hiệu chỉnh/Revising:	
Bản vẽ hoàn công/As built:	

Đơn vị thiết kế - Thi công:

**CÔNG TY
CỔ PHẦN KIẾN TRÚC
- XÂY DỰNG ĐỨC AN**

Địa chỉ:
60/10/2 Lâm Văn Bền - Phường
Tân Kiểng - Quận 7- TP.HCM

Công trình/ Project:

BINH DUONG HOTEL

Hạng mục/ Item:

**THIẾT KẾ
ĐIỆN NƯỚC**

Bản vẽ/ Drawing name:

**HỆ THỐNG ĐHKK-TẦNG
SÂN THƯƠNG**

Chủ trì thiết kế/ Project manager:


KTS. Vũ Minh Lâm

Thiết kế/ Desginer:

KTS. Vũ Minh Lâm

Tỉ lệ/ Scale: 1/100 Ngày: 04/2025

Số bản vẽ: M-204 No:

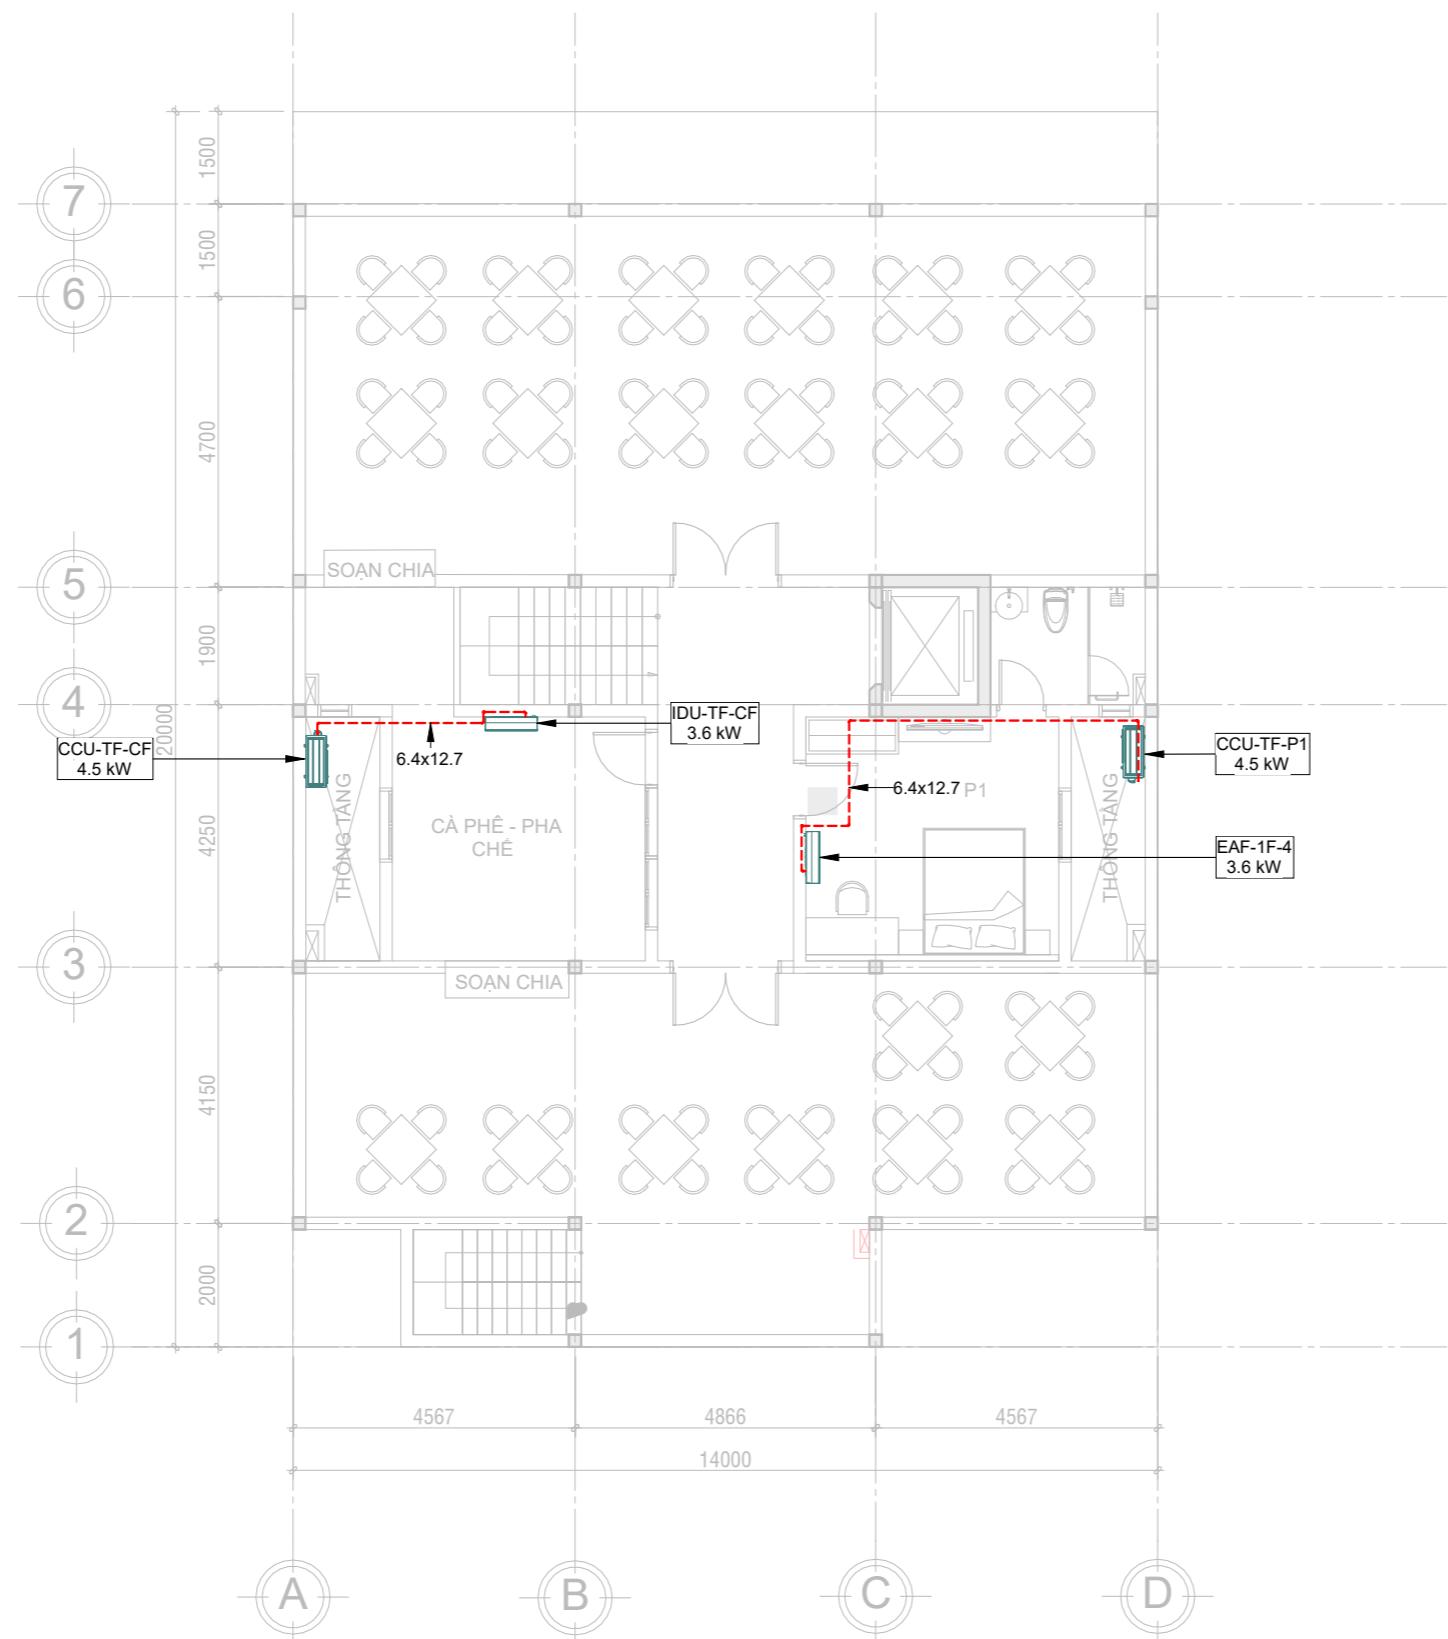

MẶT BẰNG TẦNG SÂN THƯƠNG
TL:1/100

Mục đích phát hành/Release status:
Thiết kế sơ/Preliminary:
Bản vẽ trình duyệt/For approval:
Bản vẽ tham khảo/For reference:
Bản vẽ thi công/For construction:
Bản vẽ hiệu chỉnh/Revising:
Bản vẽ hoàn công/As built:

Đơn vị thiết kế - Thi công:

**CÔNG TY
CỔ PHẦN KIẾN TRÚC
- XÂY DỰNG ĐỨC AN**

Địa chỉ:
60/10/2 Lâm Văn Bền - Phường
Tân Kiểng - Quận 7- TP.HCM

Công trình/ Project:

BINH DUONG HOTEL

Hạng mục/ Item:

**THIẾT KẾ
ĐIỆN NƯỚC**

Bản vẽ/ Drawing name:

**HỆ THỐNG CẤP
NƯỚC-TẦNG 1**

Chủ trì thiết kế/ Project manager:


KTS. Vũ Minh Lâm

Thiết kế/ Desginer:

KTS. Vũ Minh Lâm

Tỉ lệ/ Scale: 1/100 Ngày: 04/2025

Số bản vẽ: P1-201 No:

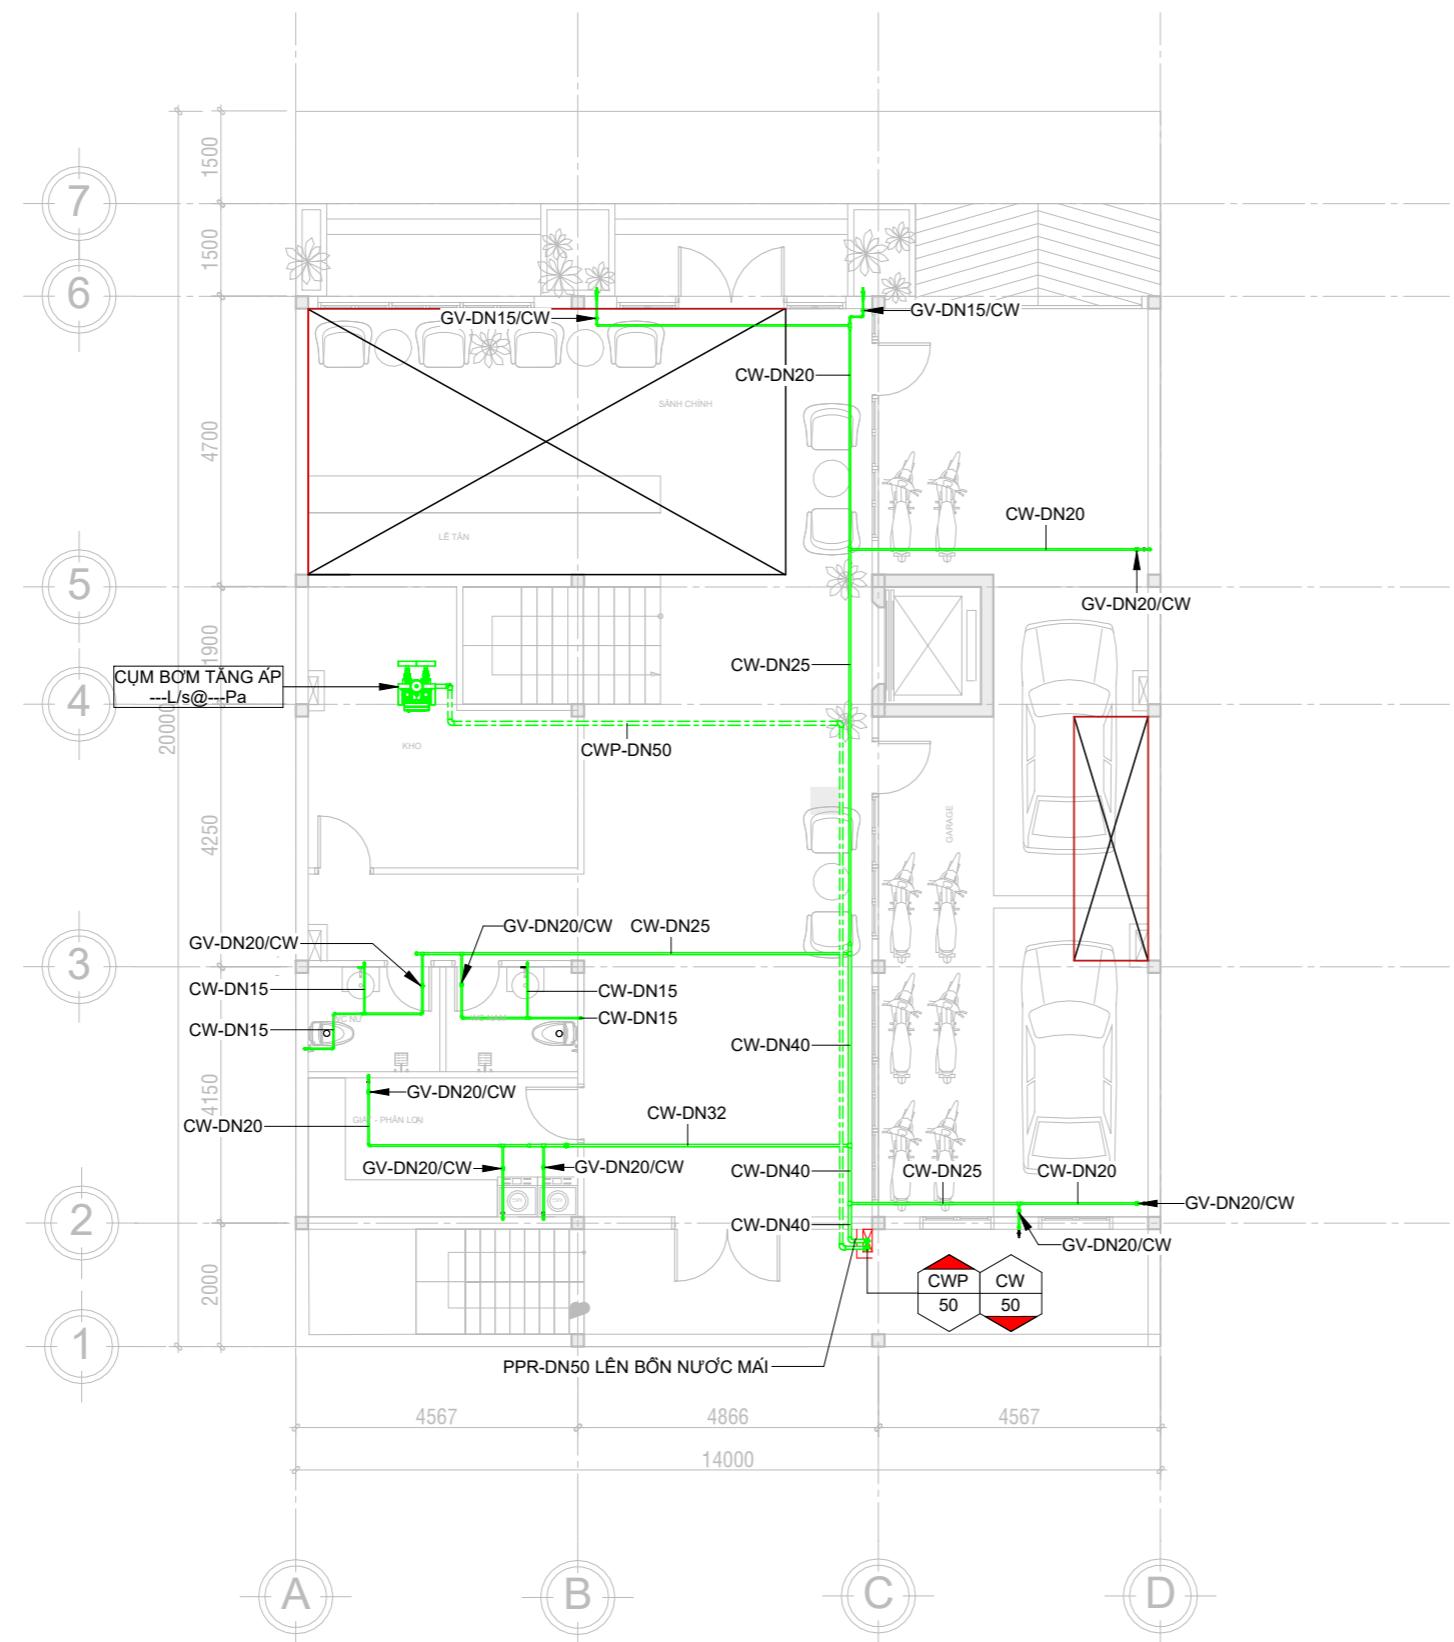

MẶT BẰNG TẦNG 1

TL:1/100

No:

Mục đích phát hành/Release status:
Thiết kế sơ/Preliminary:
Bản vẽ trình duyệt/For approval:
Bản vẽ tham khảo/For reference:
Bản vẽ thi công/For construction:
Bản vẽ hiệu chỉnh/Revising:
Bản vẽ hoàn công/As built:

Đơn vị thiết kế - Thi công:

**CÔNG TY
CỔ PHẦN KIẾN TRÚC
- XÂY DỰNG ĐỨC AN**

Địa chỉ:
60/10/2 Lâm Văn Bền - Phường
Tân Kiểng - Quận 7- TP.HCM

Công trình/ Project:

BINH DUONG HOTEL

Hạng mục/ Item:

**THIẾT KẾ
ĐIỆN NƯỚC**

Bản vẽ/ Drawing name:

**HỆ THỐNG CẤP
NƯỚC-TẦNG LƯNG**

Chủ trì thiết kế/ Project manager:


KTS. Vũ Minh Lâm

Thiết kế/ Desginer:

KTS. Vũ Minh Lâm

Tỉ lệ/ Scale: 1/100 Ngày: 04/2025

Số bản vẽ: P1-202 No:

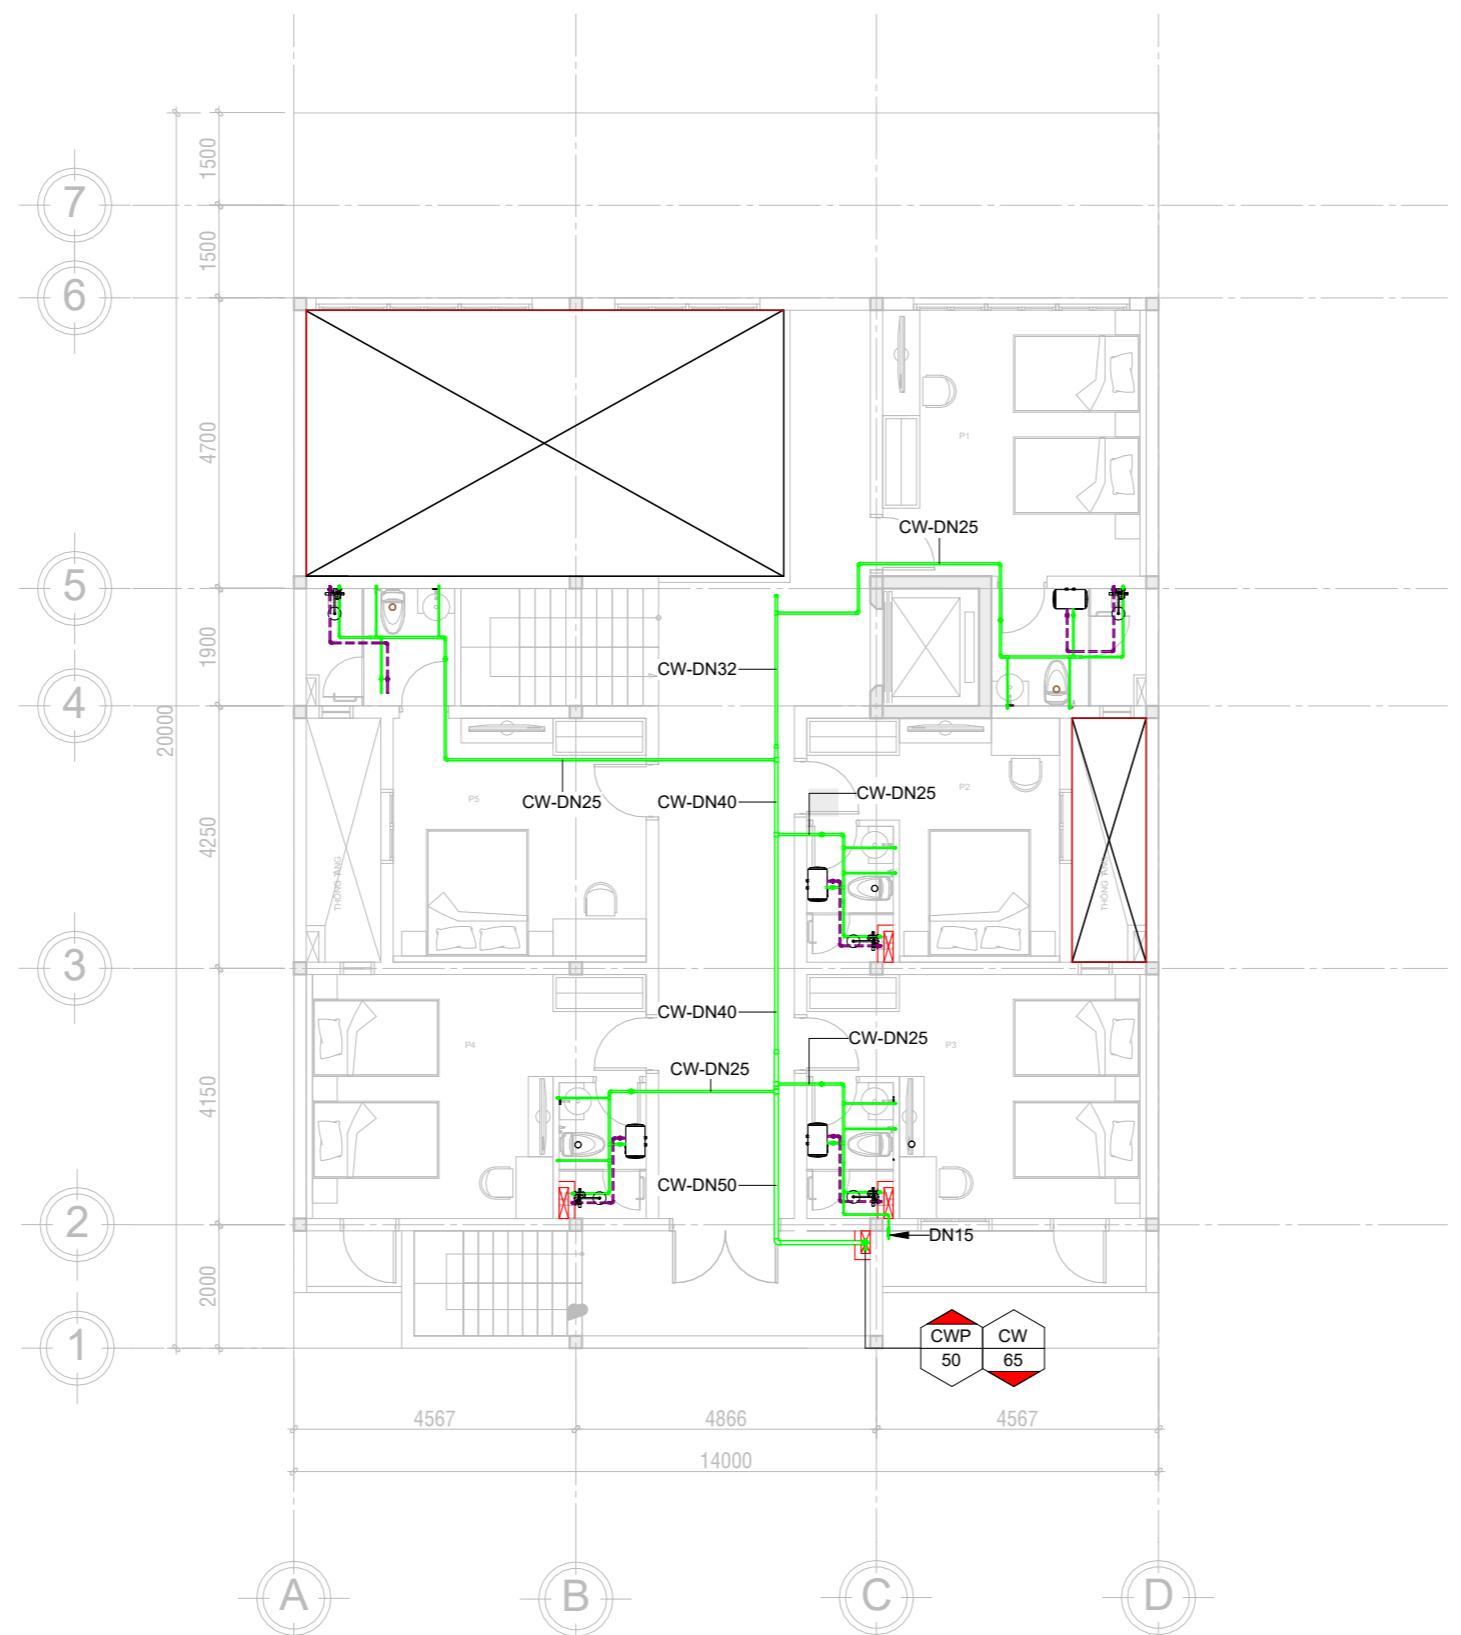

MẶT BẰNG TẦNG LƯNG

TL:1/100

Mục đích phát hành/Release status:
Thiết kế sơ/Preliminary:
Bản vẽ trình duyệt/For approval:
Bản vẽ tham khảo/For reference:
Bản vẽ thi công/For construction:
Bản vẽ hiệu chỉnh/Revising:
Bản vẽ hoàn công/As built:

Đơn vị thiết kế - Thi công:

**CÔNG TY
CỔ PHẦN KIẾN TRÚC
- XÂY DỰNG ĐỨC AN**

Địa chỉ:
60/10/2 Lâm Văn Bền - Phường
Tân Kiểng - Quận 7 - TP.HCM

Công trình/ Project:

BINH DUONG HOTEL

Hạng mục/ Item:

**THIẾT KẾ
ĐIỆN NƯỚC**

Bản vẽ/ Drawing name:

**HỆ THỐNG CẤP
NƯỚC-TẦNG 2-4**

Chủ trì thiết kế/ Project manager:


KTS. Vũ Minh Lâm

Thiết kế/ Desginer:

KTS. Vũ Minh Lâm

Tỉ lệ/ Scale: 1/100 Ngày: 04/2025

Số bản vẽ: P1-203 No:

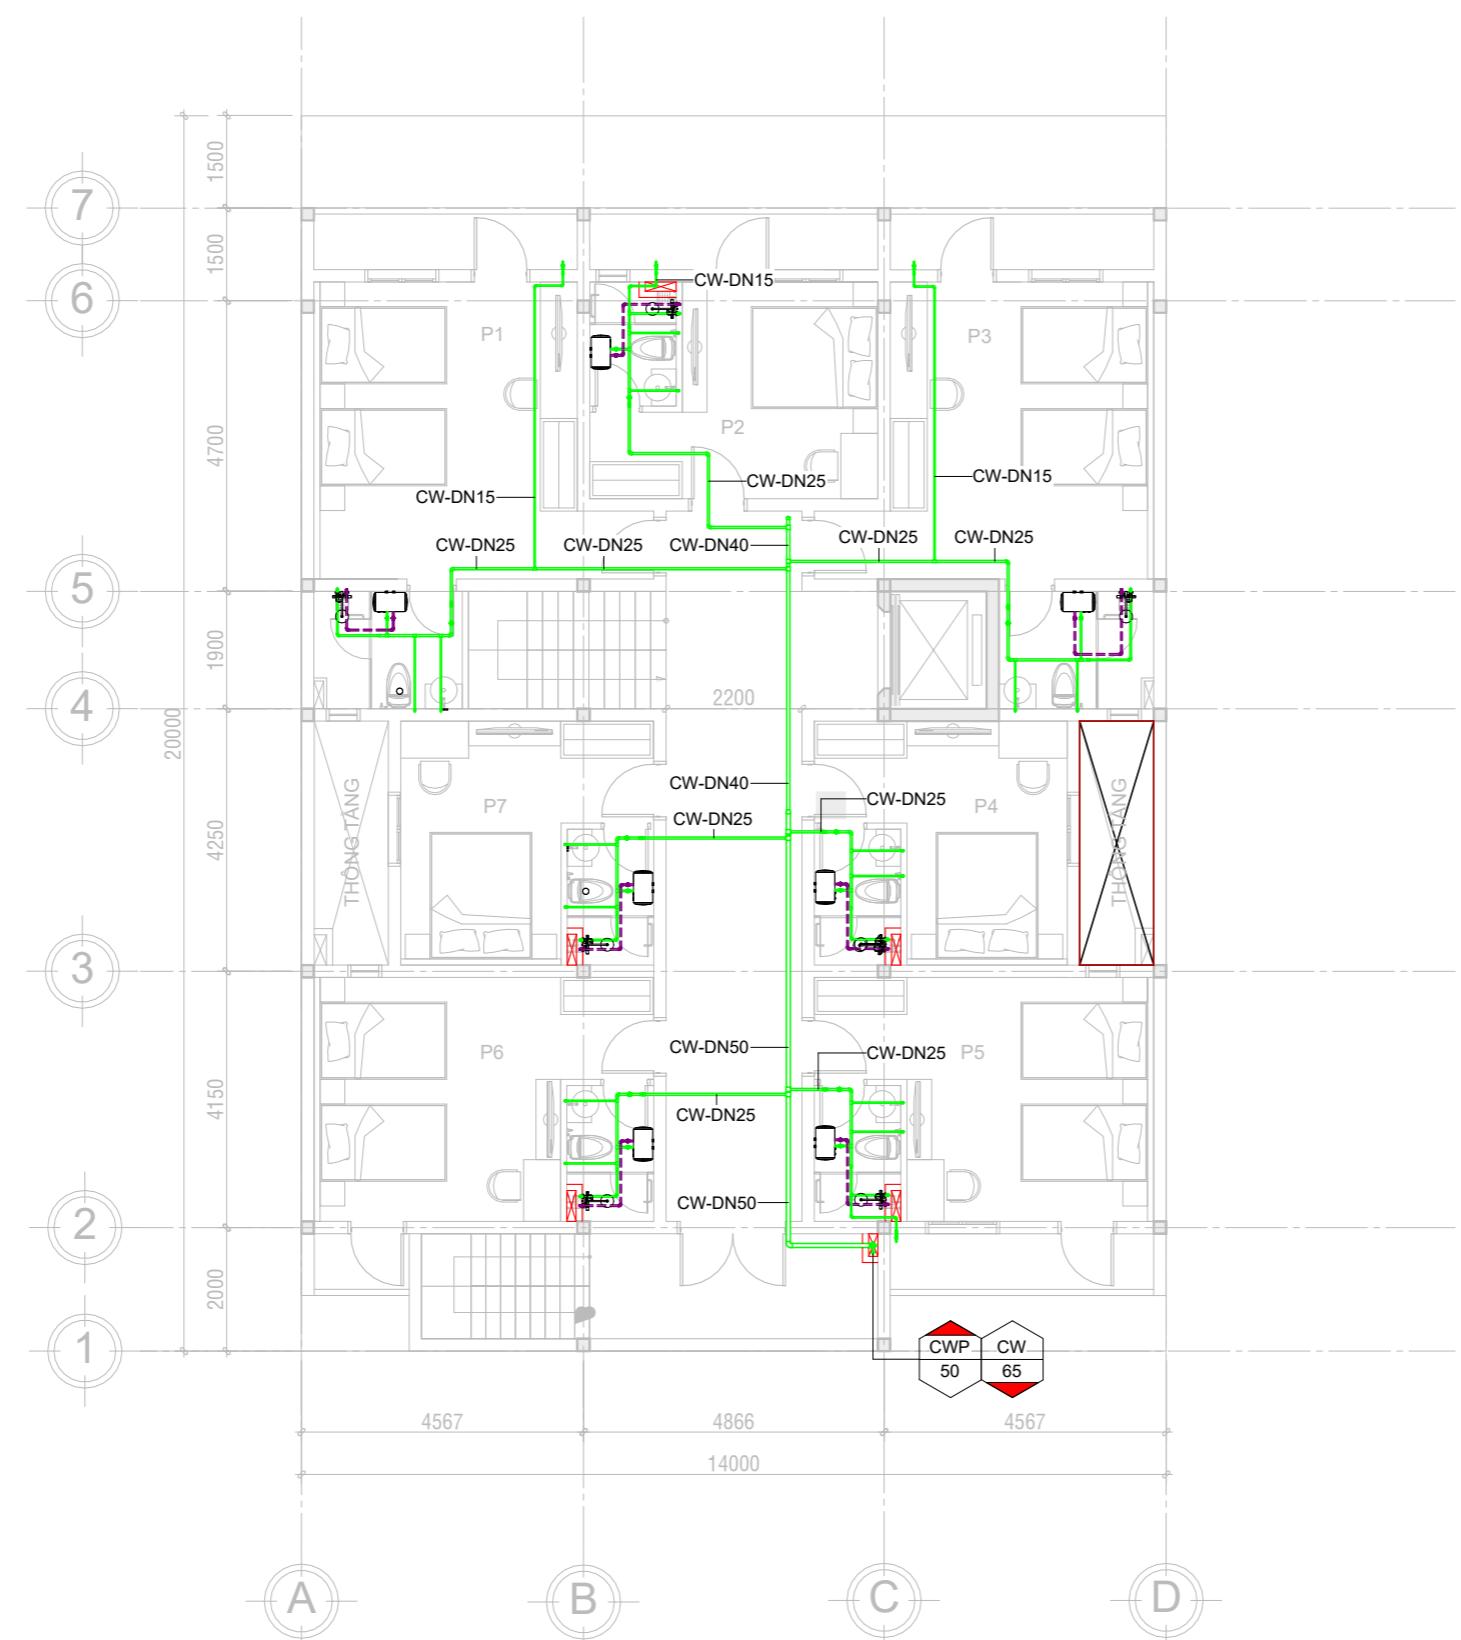

MẶT BẰNG TẦNG ĐIỆN HÌNH 2-6

TL:1/100

Mục đích phát hành/Release status:
Thiết kế sơ/Preliminary:
Bản vẽ trình duyệt/For approval:
Bản vẽ tham khảo/For reference:
Bản vẽ thi công/For construction:
Bản vẽ hiệu chỉnh/Revising:
Bản vẽ hoàn công/As built:

Đơn vị thiết kế - Thi công:

**CÔNG TY
CỔ PHẦN KIẾN TRÚC
- XÂY DỰNG ĐỨC AN**

Địa chỉ:
60/10/2 Lâm Văn Bền - Phường
Tân Kiểng - Quận 7- TP.HCM

Công trình/ Project:

BINH DUONG HOTEL

Hạng mục/ Item:

**THIẾT KẾ
ĐIỆN NƯỚC**

Bản vẽ/ Drawing name:

**HỆ THỐNG CẤP
NƯỚC-TẦNG 5, 6**

Chủ trì thiết kế/ Project manager:

KTS. Vũ Minh Lâm

Thiết kế/ Desginer:

KTS. Vũ Minh Lâm

Tỉ lệ/ Scale: 1/100 Ngày: 04/2025

Số bản vẽ: P1-204 No:



MẶT BẰNG TẦNG ĐIỆN HÌNH 2-6

TL:1/100

Mục đích phát hành/Release status:
Thiết kế sơ/Preliminary:
Bản vẽ trình duyệt/For approval:
Bản vẽ tham khảo/For reference:
Bản vẽ thi công/For construction:
Bản vẽ hiệu chỉnh/Revising:
Bản vẽ hoàn công/As built:

Đơn vị thiết kế - Thi công:

**CÔNG TY
CỔ PHẦN KIẾN TRÚC
- XÂY DỰNG ĐỨC AN**

Địa chỉ:
60/10/2 Lâm Văn Bền - Phường
Tân Kiểng - Quận 7- TP.HCM

Công trình/ Project:

BINH DUONG HOTEL

Hạng mục/ Item:

**THIẾT KẾ
ĐIỆN NƯỚC**

Bản vẽ/ Drawing name:

**HỆ THỐNG CẤP
NƯỚC-TẦNG SÂN
THƯỢNG**

Chủ trì thiết kế/ Project manager:


KTS. Vũ Minh Lâm

Thiết kế/ Desginer:

KTS. Vũ Minh Lâm

Tỉ lệ/ Scale: 1/100 Ngày: 04/2025

Số bản vẽ: P1-205 No:

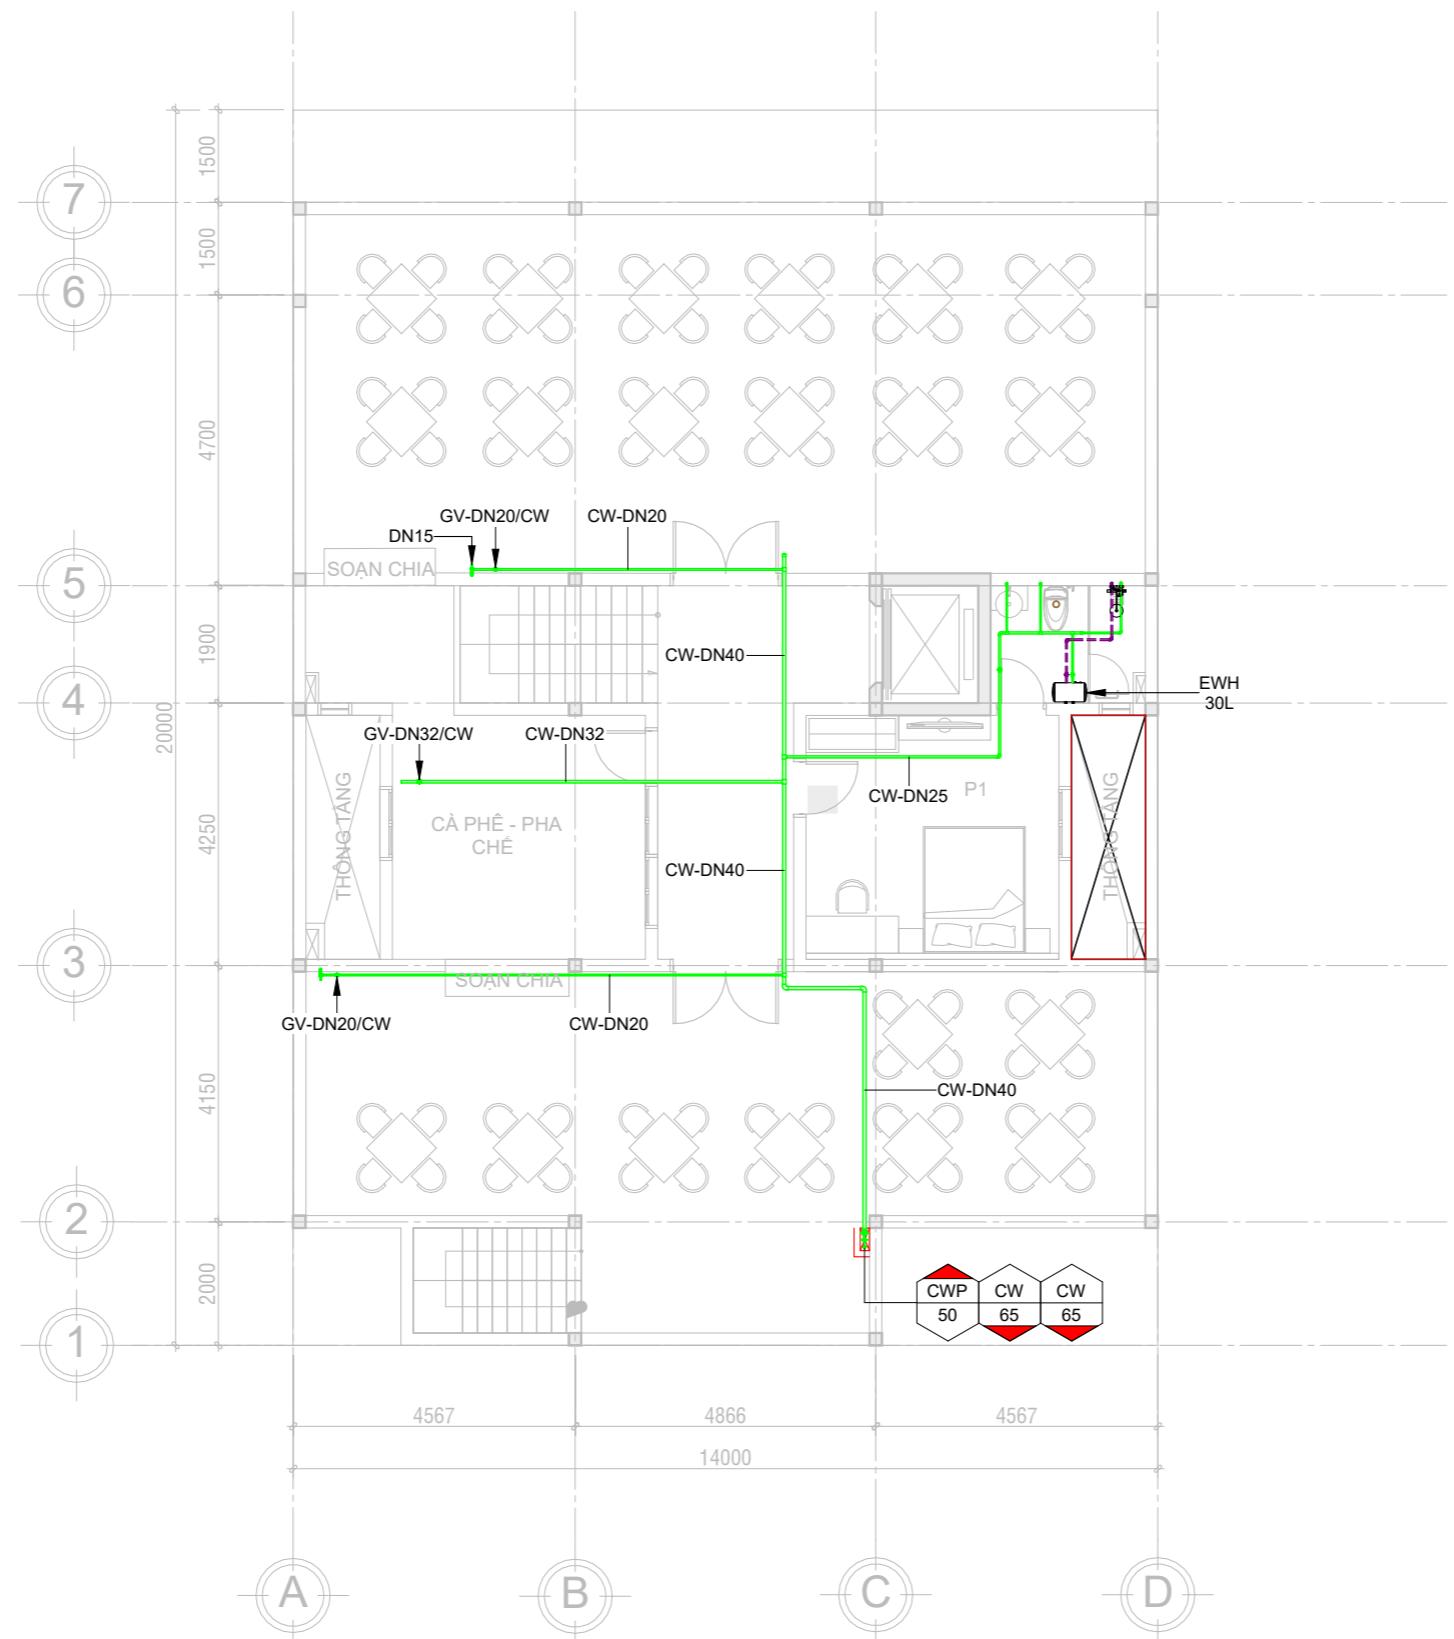

MẶT BẰNG TẦNG SÂN THƯỢNG

TL:1/100

Mục đích phát hành/Release status:
Thiết kế sơ/Preliminary:
Bản vẽ trình duyệt/For approval:
Bản vẽ tham khảo/For reference:
Bản vẽ thi công/For construction:
Bản vẽ hiệu chỉnh/Revising:
Bản vẽ hoàn công/As built:

Đơn vị thiết kế - Thi công:

**CÔNG TY
CỔ PHẦN KIẾN TRÚC
- XÂY DỰNG ĐỨC AN**

Địa chỉ:

60/10/2 Lâm Văn Bền - Phường
Tân Kiểng - Quận 7- TP.HCM

Công trình/ Project:

BINH DUONG HOTEL

Hạng mục/ Item:

**THIẾT KẾ
ĐIỆN NƯỚC**

Bản vẽ/ Drawing name:

**HỆ THỐNG CẤP
NƯỚC-MÁI**

Chủ trì thiết kế/ Project manager:


KTS. Vũ Minh Lâm

Thiết kế/ Desginer:

KTS. Vũ Minh Lâm


Tỉ lệ/ Scale: 1/100 Ngày: 04/2025

Số bản vẽ: P1-206 No:

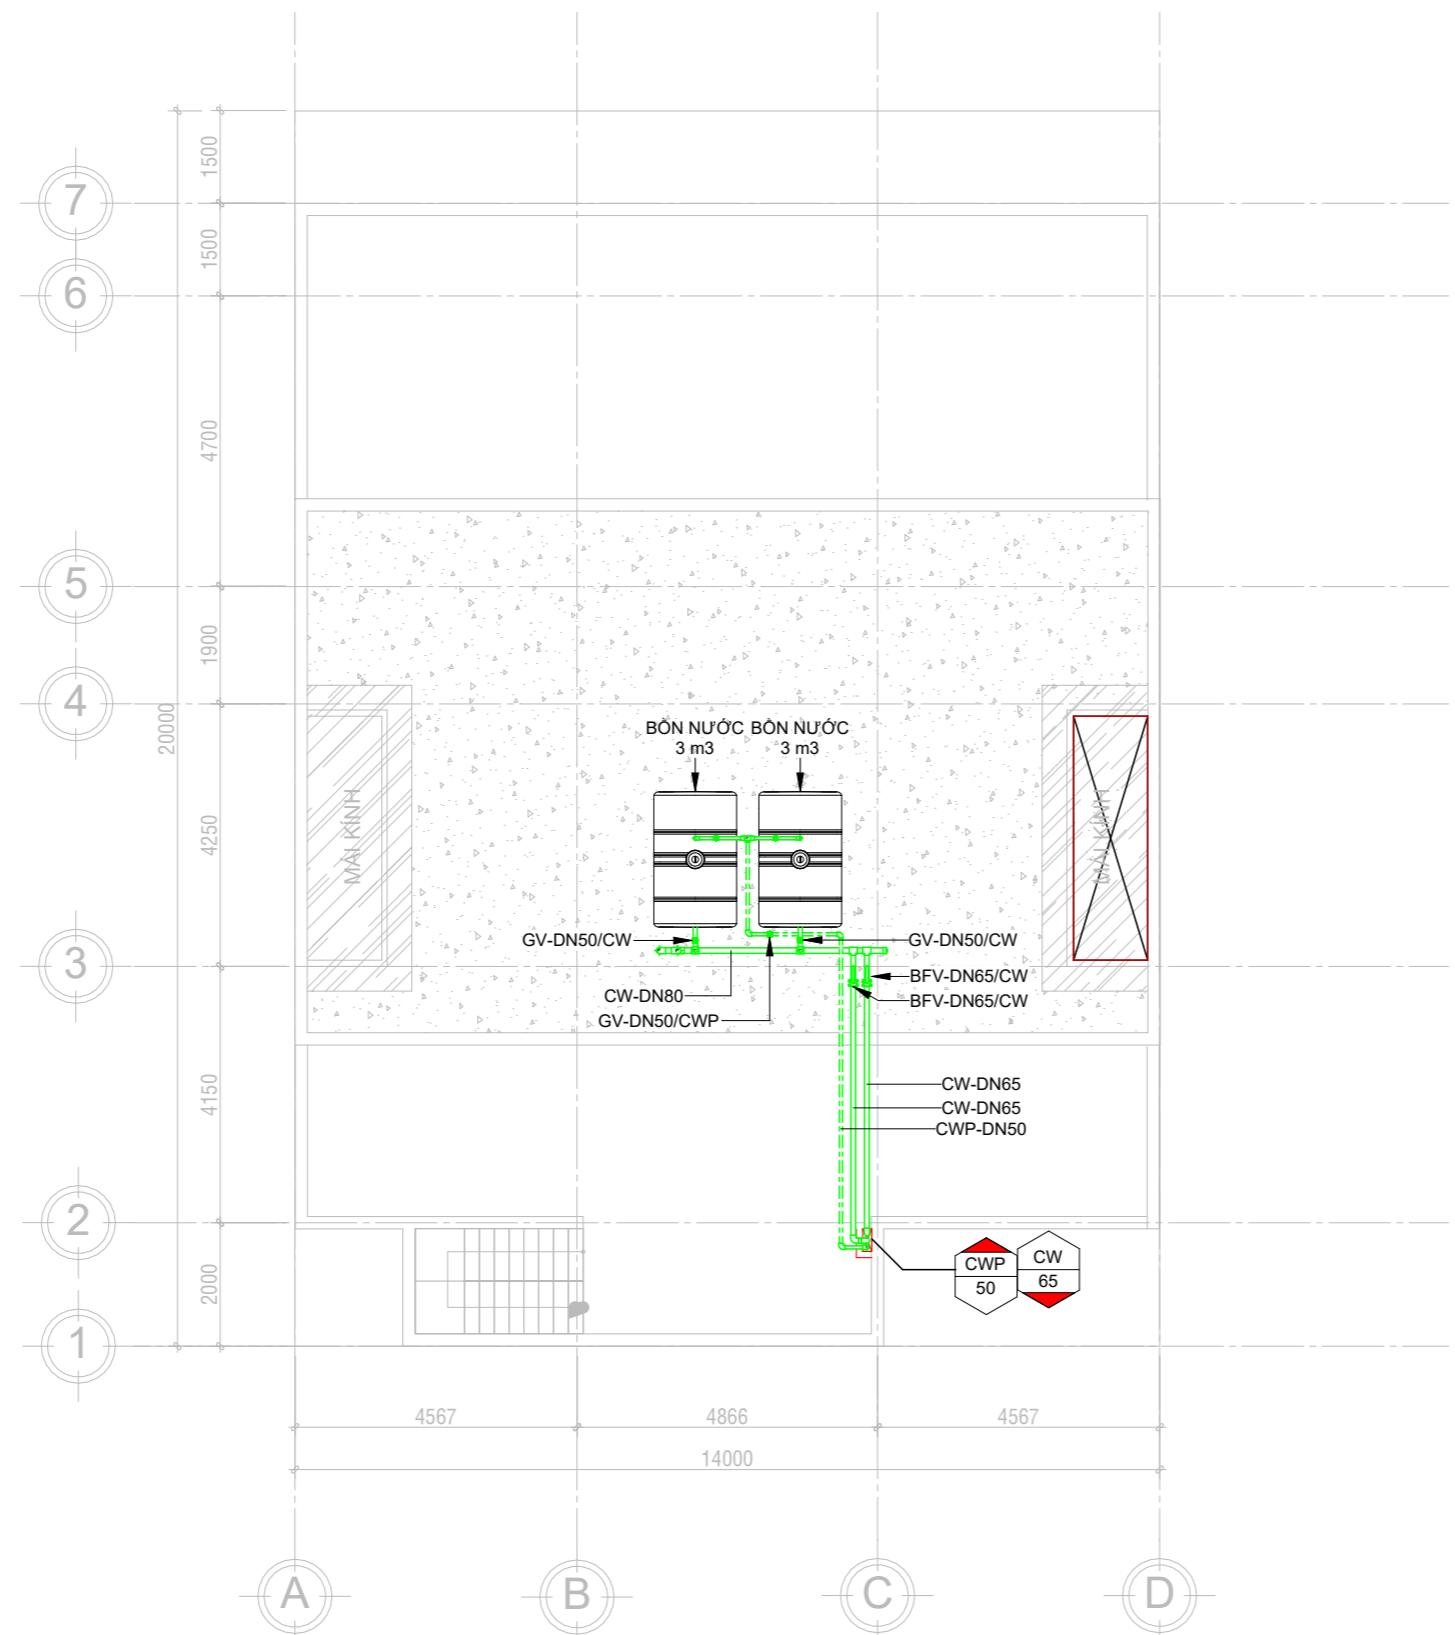

MẶT BẰNG MÁI

TL:1/100

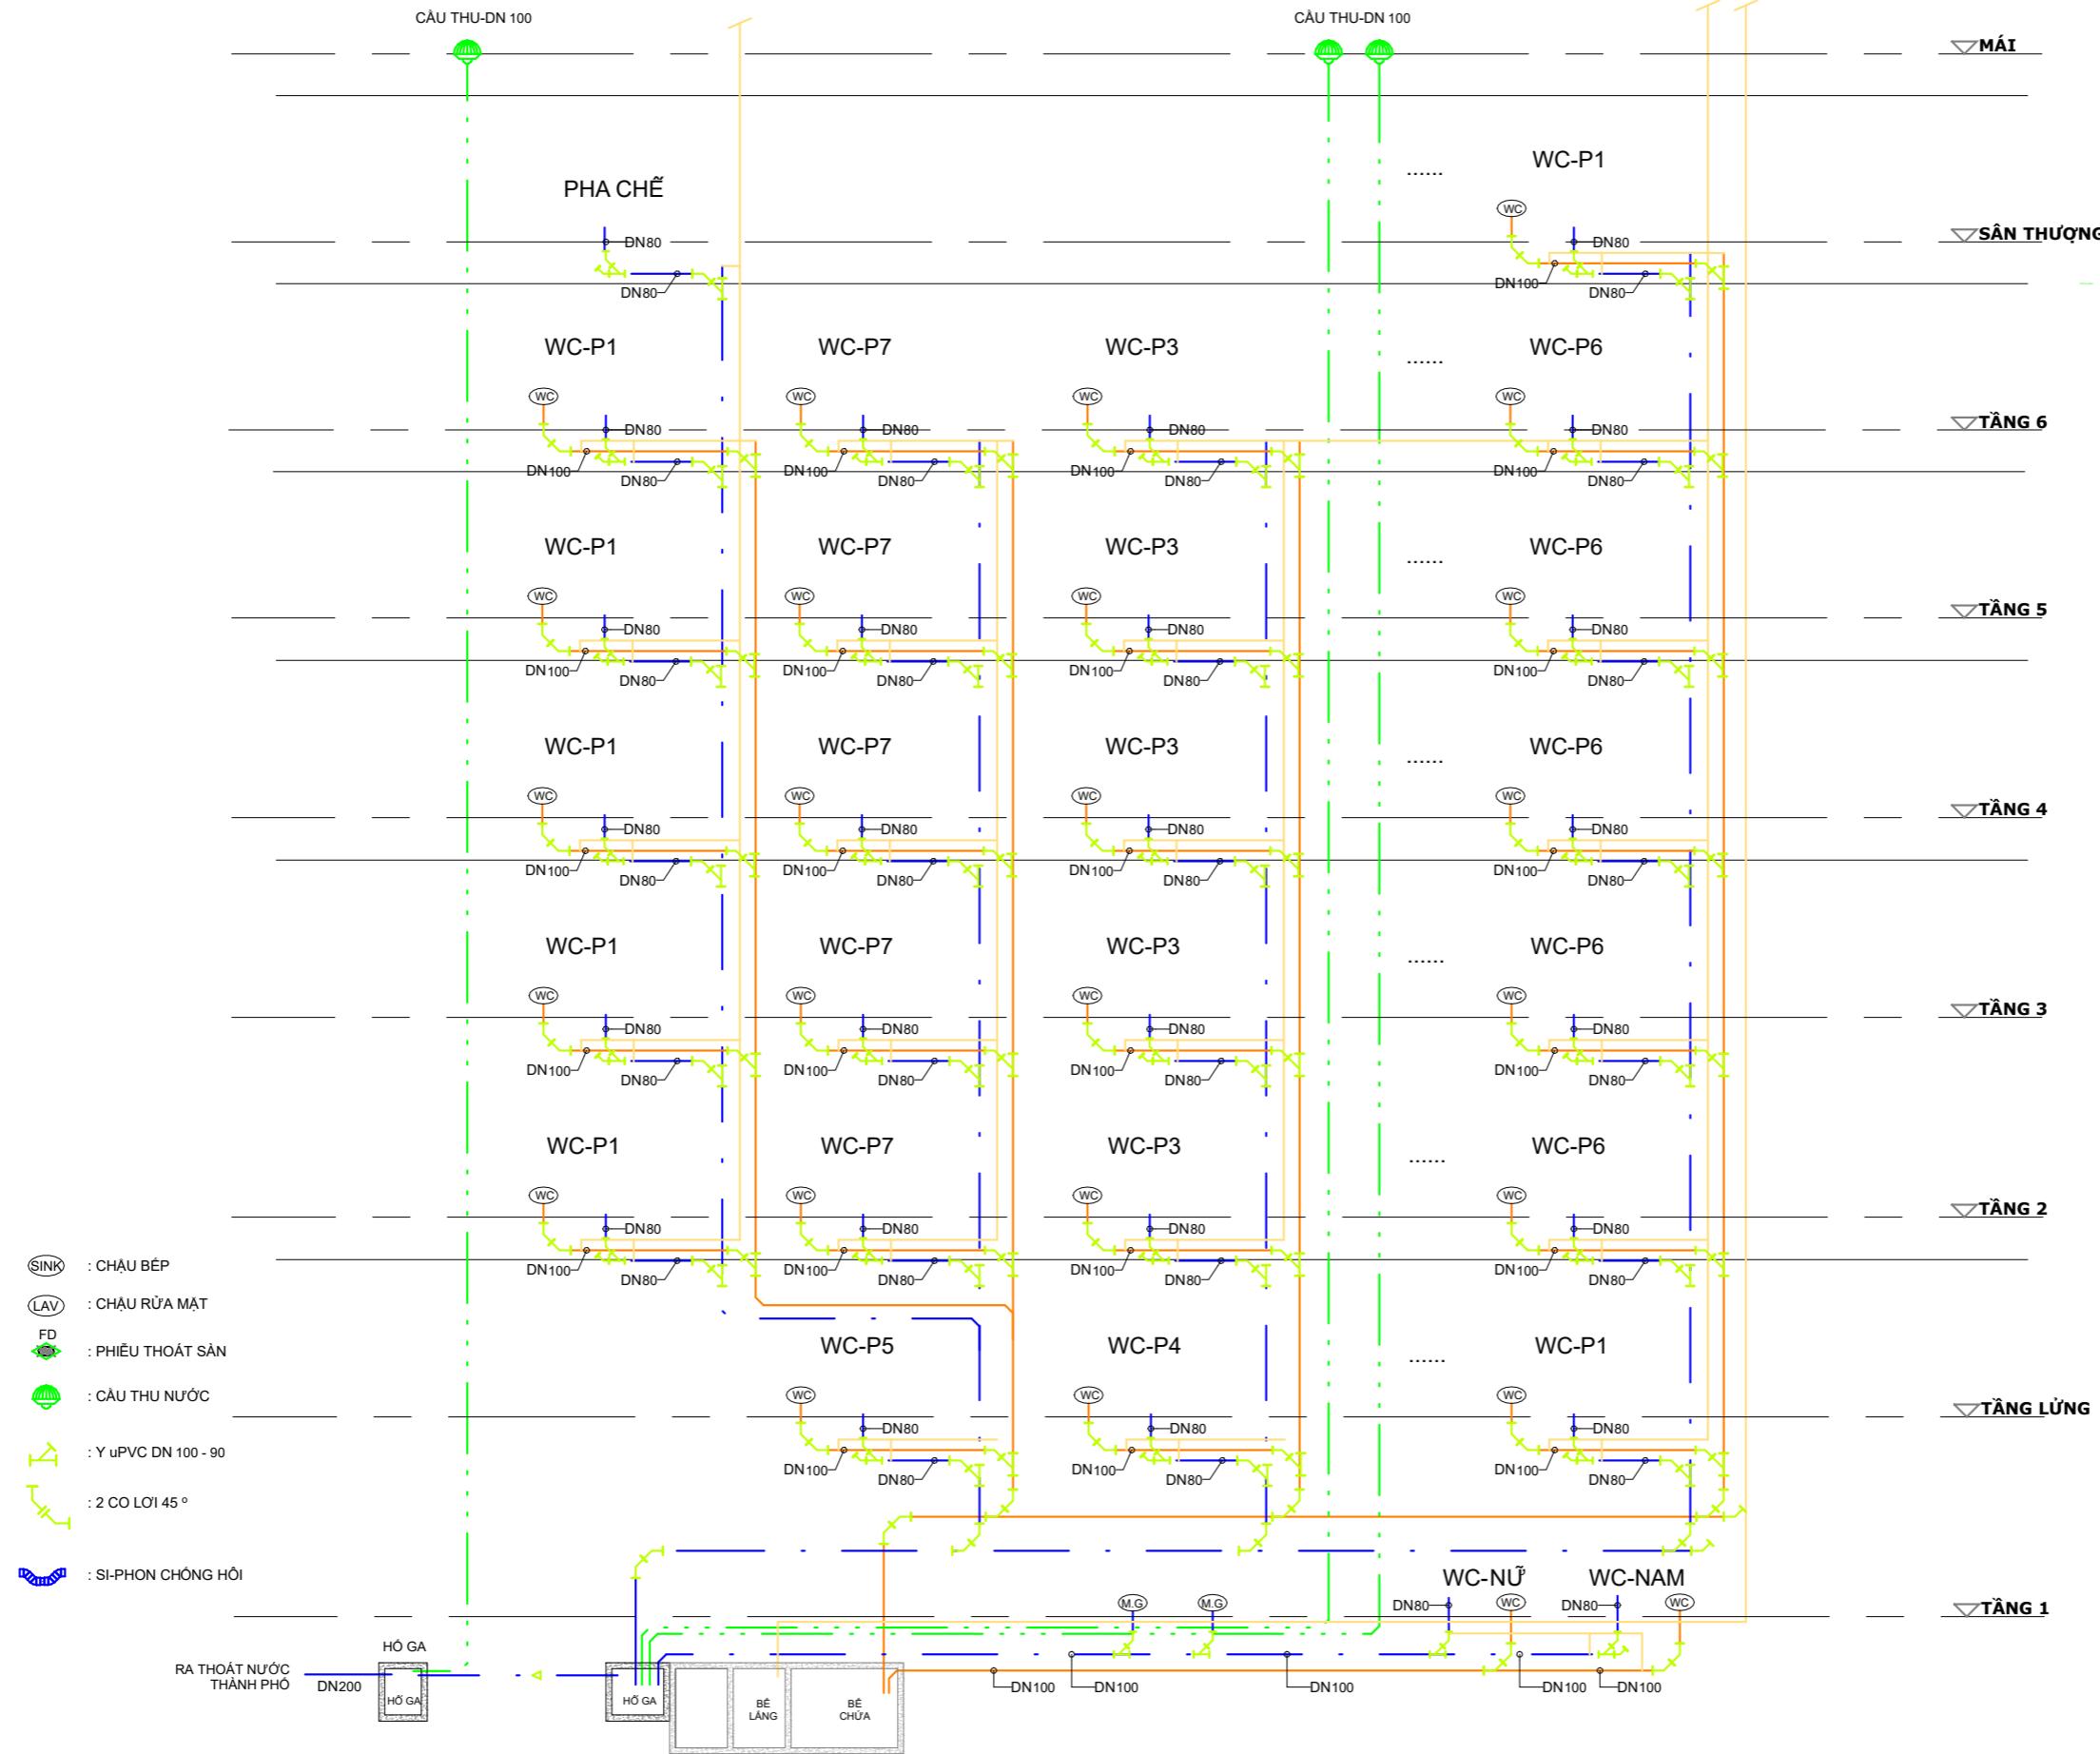

Mục đích phát hành/Release status:	
Thiết kế sơ/Preliminary:	
Bản vẽ trình duyệt/For approval:	
Bản vẽ tham khảo/For reference:	
Bản vẽ thi công/For construction:	X
Bản vẽ hiệu chỉnh/Revising:	
Bản vẽ hoàn công/As built:	

Đơn vị thiết kế - Thi công:

CÔNG TY
CỔ PHẦN KIẾN TRÚC
- XÂY DỰNG ĐỨC AN

Địa chỉ:
60/10/2 Lâm Văn Bền - Phường
Tân Kiêng - Quận 7- TP.HCM

Công trình/ Project:

BINH DUONG HOTEL

Hàng mục/ Item

THIẾT KẾ
ĐIỆN NƯỚC

Bản vẽ/ Drawing name:

SƠ ĐỒ NGUYỄN LÝ-HỆ THÔNG CẤP NƯỚC

Chủ trì thiết kế/ Project manager:



KTS. Vũ Minh Lâm

Thiết kế/ Desginer:



KTS. Vũ Minh Lâm

Tỉ lệ/ Scale: 1/100 Ngày: 04/2025

Số bản vẽ: B2.101

30 ball ve. **FZ-101** NO.

Mục đích phát hành/Release status:
Thiết kế sơ/Preliminary:
Bản vẽ trình duyệt/For approval:
Bản vẽ tham khảo/For reference:
Bản vẽ thi công/For construction:
Bản vẽ hiệu chỉnh/Revising:
Bản vẽ hoàn công/As built:

Đơn vị thiết kế - Thi công:

**CÔNG TY
CỔ PHẦN KIẾN TRÚC
- XÂY DỰNG ĐỨC AN**

Địa chỉ:
60/10/2 Lâm Văn Bền - Phường
Tân Kiểng - Quận 7- TP.HCM

Công trình/ Project:

BINH DUONG HOTEL

Hạng mục/ Item:

**THIẾT KẾ
ĐIỆN NƯỚC**

Bản vẽ/ Drawing name:

**HỆ THỐNG THOÁT
NƯỚC-TẦNG 1**

Chủ trì thiết kế/ Project manager:


KTS. Vũ Minh Lâm

Thiết kế/ Desginer:

KTS. Vũ Minh Lâm

Tỉ lệ/ Scale: 1/100 Ngày: 04/2025

Số bản vẽ: P2-201 No:

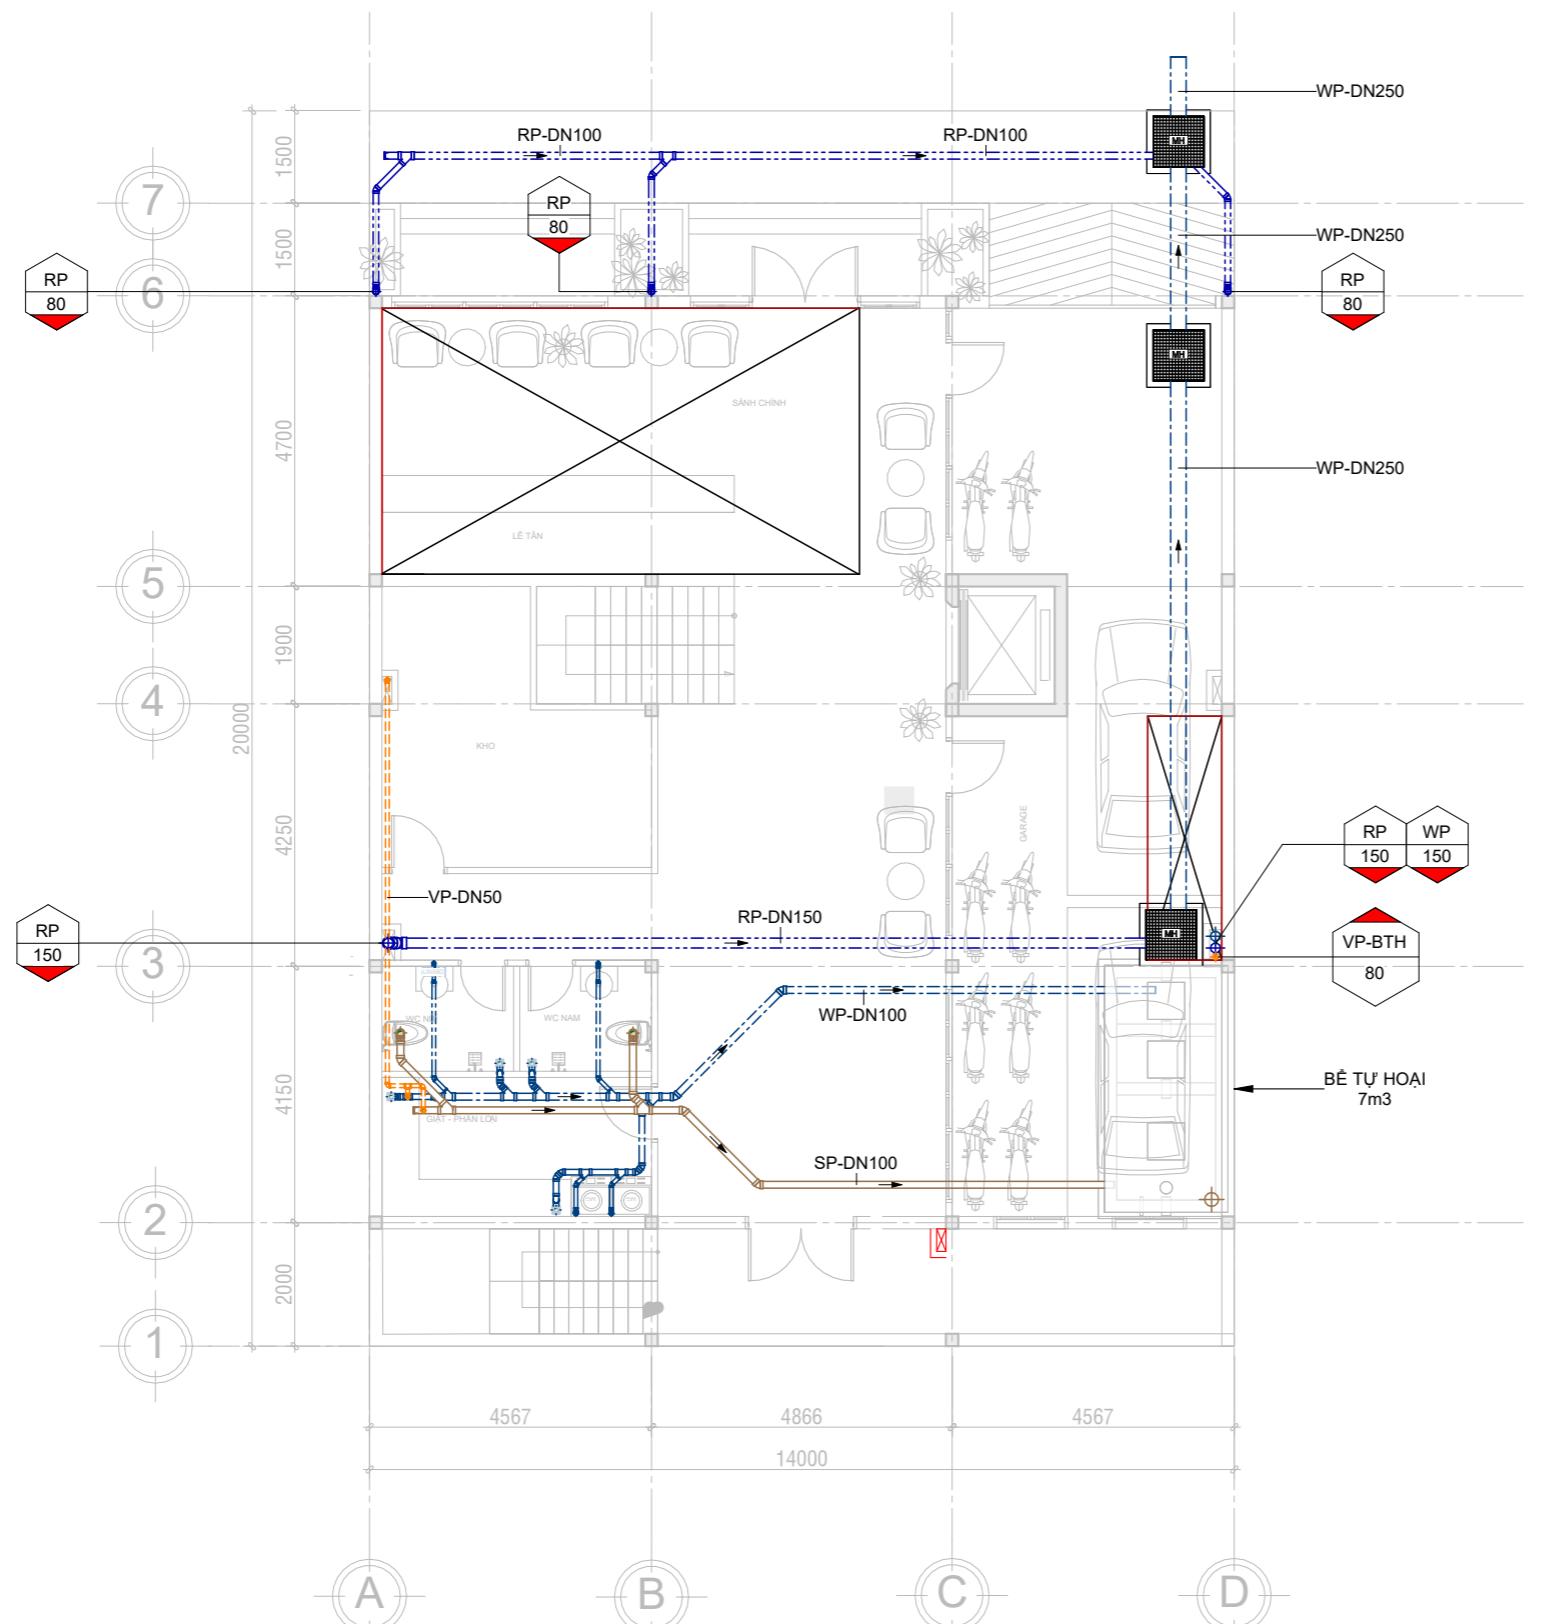

MẶT BẰNG TẦNG 1

TL:1/100

Mục đích phát hành/Release status:
Thiết kế sơ/Preliminary:
Bản vẽ trình duyệt/For approval:
Bản vẽ tham khảo/For reference:
Bản vẽ thi công/For construction:
Bản vẽ hiệu chỉnh/Revising:
Bản vẽ hoàn công/As built:

Đơn vị thiết kế - Thi công:

**CÔNG TY
CỔ PHẦN KIẾN TRÚC
- XÂY DỰNG ĐỨC AN**

Địa chỉ:
60/10/2 Lâm Văn Bền - Phường
Tân Kiểng - Quận 7- TP.HCM

Công trình/ Project:

BINH DUONG HOTEL

Hạng mục/ Item:

**THIẾT KẾ
ĐIỆN NƯỚC**

Bản vẽ/ Drawing name:

**HỆ THỐNG THOÁT
NƯỚC-TẦNG LƯNG**

Chủ trì thiết kế/ Project manager:


KTS. Vũ Minh Lâm

Thiết kế/ Desginer:

KTS. Vũ Minh Lâm

Tỉ lệ/ Scale: 1/100 Ngày: 04/2025


Số bản vẽ: P2-202 No:

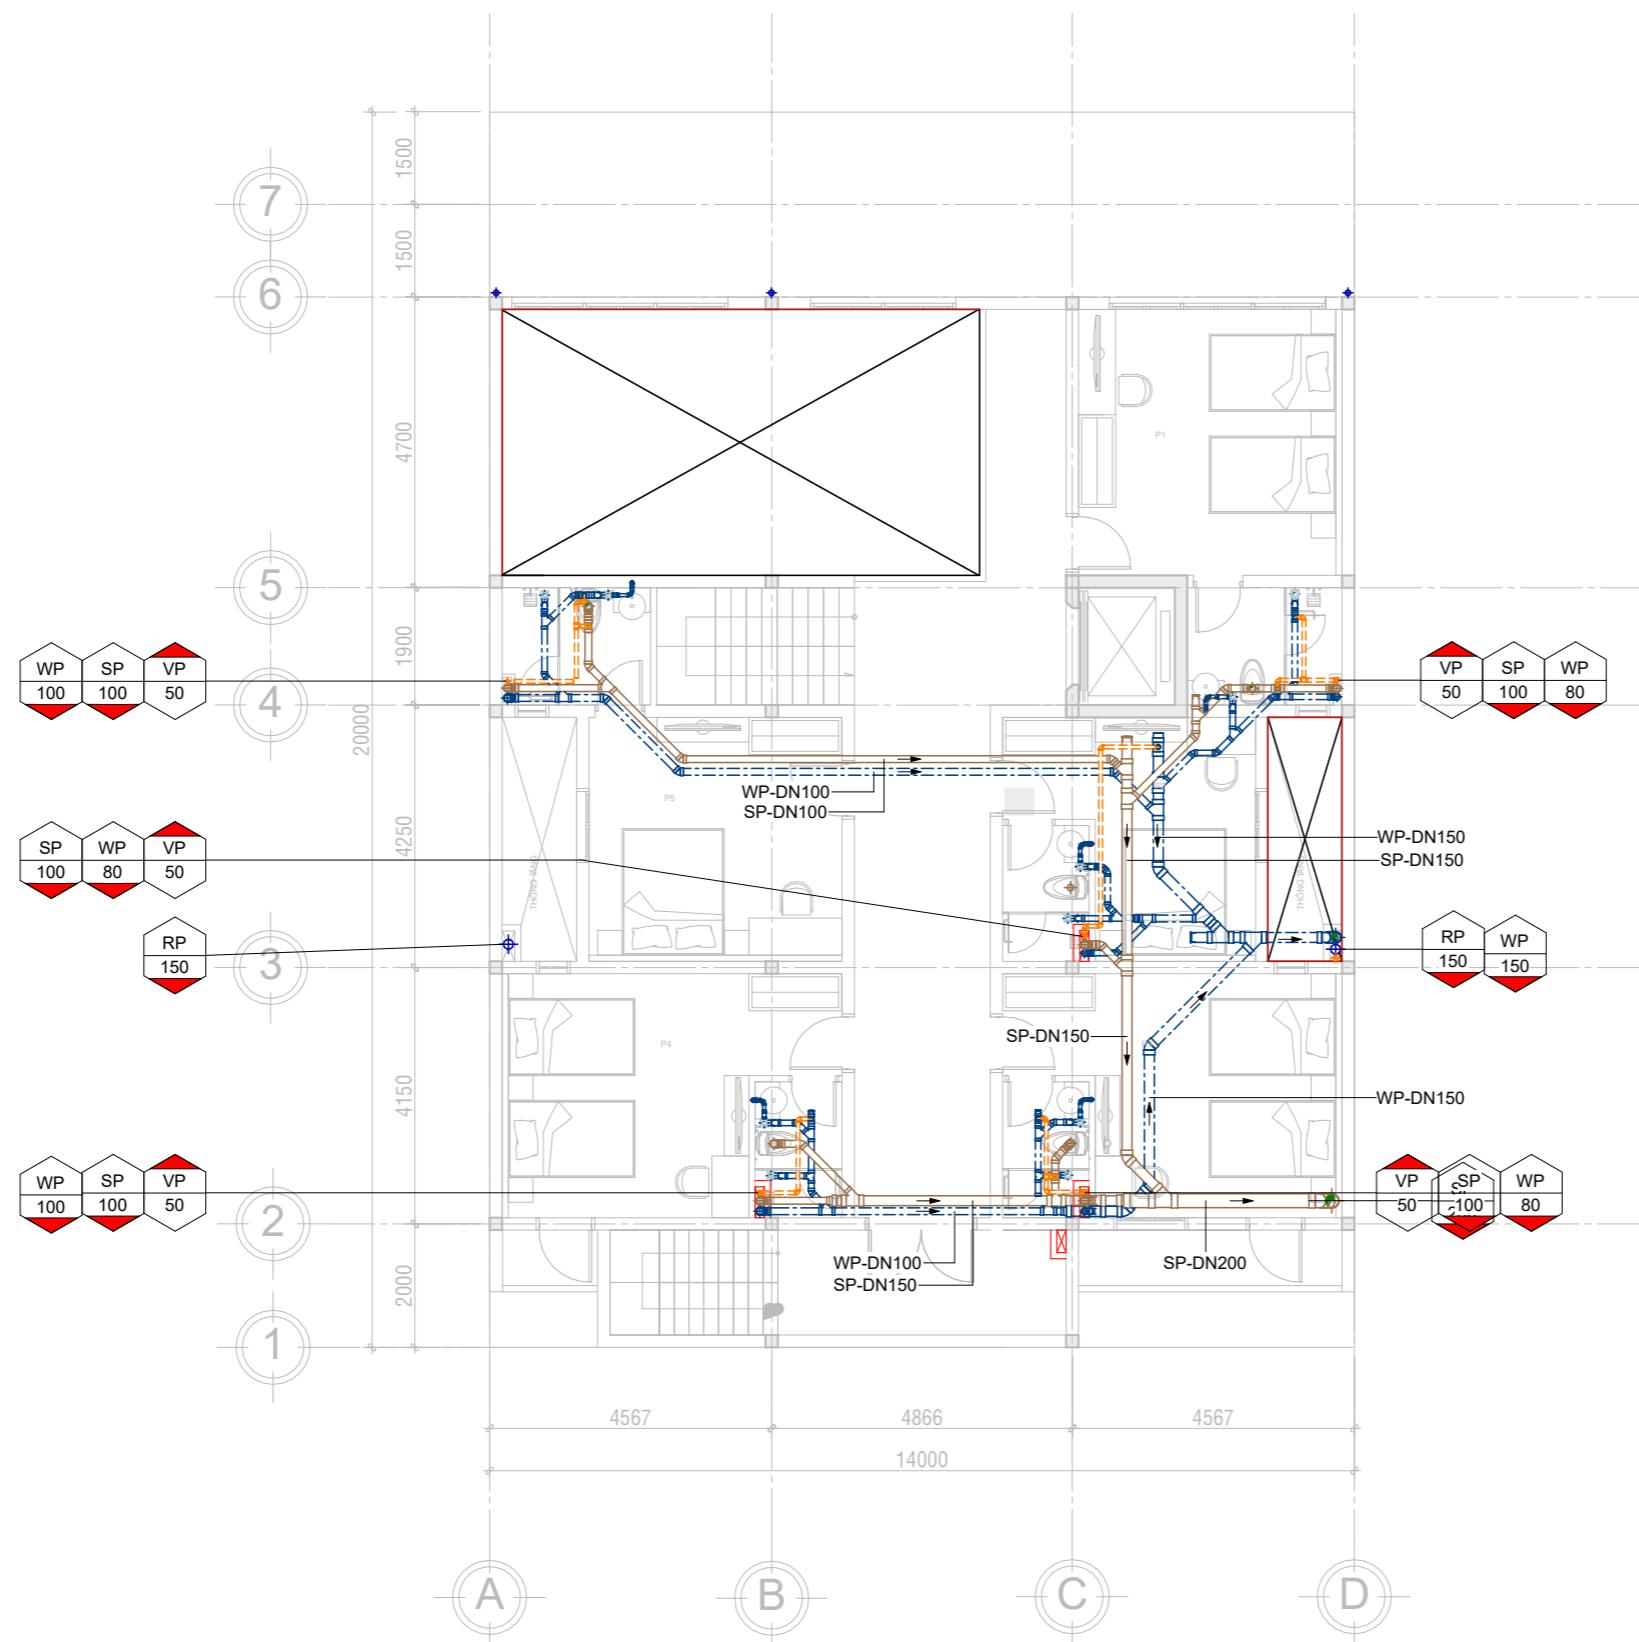

MẶT BẰNG TẦNG LƯNG

TL:1/100

Mục đích phát hành/Release status:
Thiết kế sơ/Preliminary:
Bản vẽ trình duyệt/For approval:
Bản vẽ tham khảo/For reference:
Bản vẽ thi công/For construction:
Bản vẽ hiệu chỉnh/Revising:
Bản vẽ hoàn công/As built:

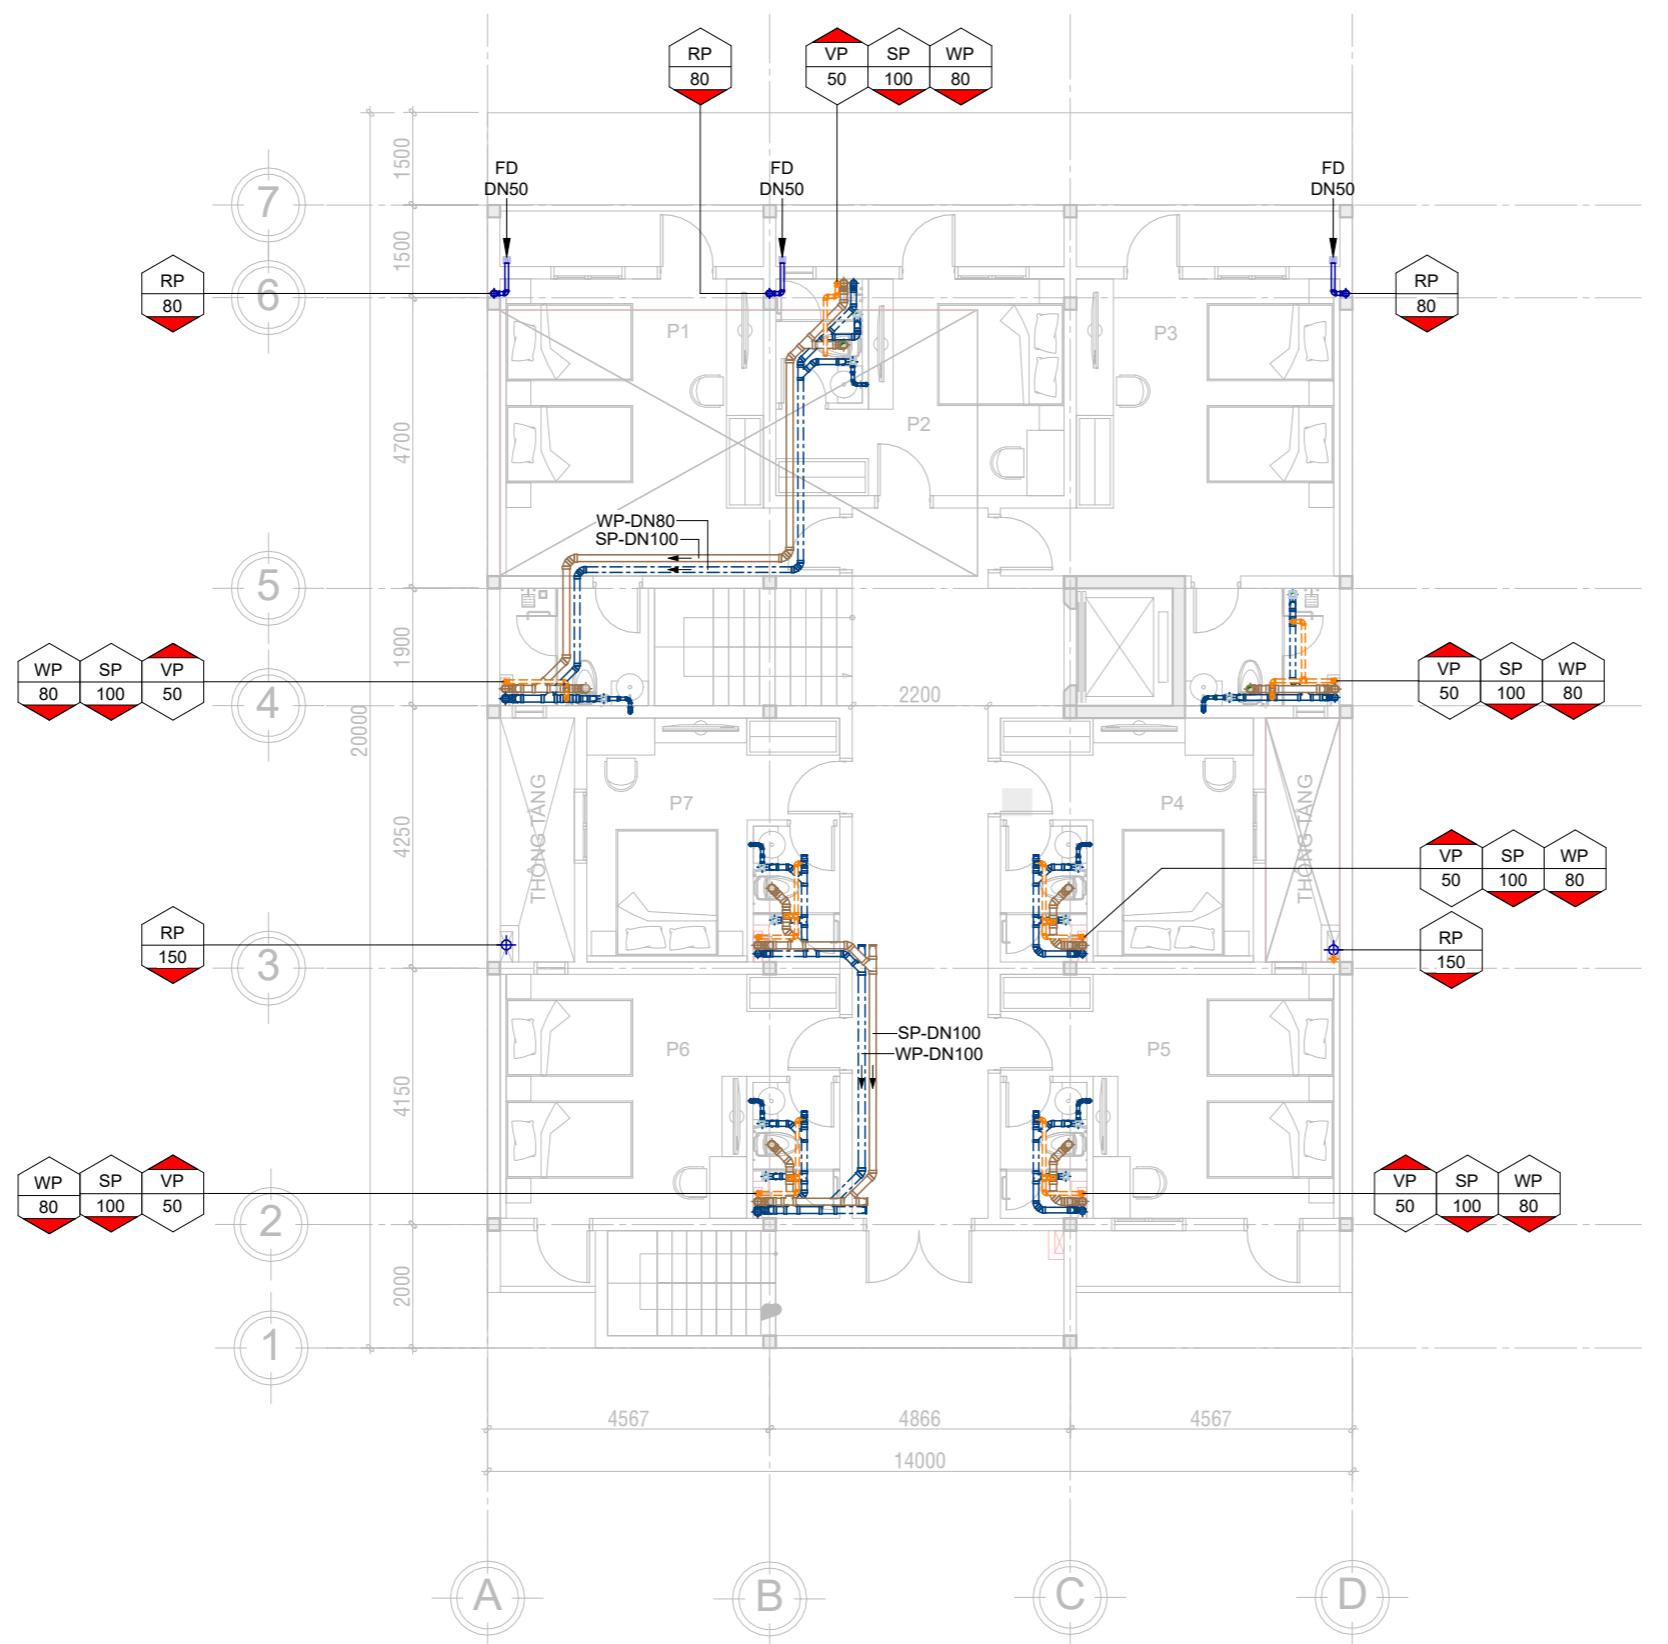

MẶT BẰNG TẦNG ĐIỀN HÌNH 2-6

TL:1/100

Đơn vị thiết kế - Thi công:

**CÔNG TY
CỔ PHẦN KIẾN TRÚC
- XÂY DỰNG ĐỨC AN**

Địa chỉ:

60/10/2 Lâm Văn Bền - Phường
Tân Kiểng - Quận 7 - TP.HCM

Công trình/ Project:

BINH DUONG HOTEL

Hạng mục/ Item:

**THIẾT KẾ
ĐIỆN NƯỚC**

Bản vẽ/ Drawing name:

**HỆ THỐNG THOÁT
NƯỚC-TẦNG 2**

Chủ trì thiết kế/ Project manager:

KTS. Vũ Minh Lâm

Thiết kế/ Desginer:

KTS. Vũ Minh Lâm

Tỉ lệ/ Scale: 1/100 Ngày: 04/2025

Số bản vẽ: P2-203 No:

Mục đích phát hành/Release status:
Thiết kế sơ/Preliminary:
Bản vẽ trình duyệt/For approval:
Bản vẽ tham khảo/For reference:
Bản vẽ thi công/For construction:
Bản vẽ hiệu chỉnh/Revising:
Bản vẽ hoàn công/As built:

Đơn vị thiết kế - Thi công:

**CÔNG TY
CỔ PHẦN KIẾN TRÚC
- XÂY DỰNG ĐỨC AN**

Địa chỉ:
60/10/2 Lâm Văn Bền - Phường
Tân Kiểng - Quận 7 - TP.HCM

Công trình/ Project:

BINH DUONG HOTEL

Hạng mục/ Item:

**THIẾT KẾ
ĐIỆN NƯỚC**

Bản vẽ/ Drawing name:

**HỆ THỐNG THOÁT
NƯỚC-TẦNG 3-6**

Chủ trì thiết kế/ Project manager:


KTS. Vũ Minh Lâm

Thiết kế/ Desginer:

KTS. Vũ Minh Lâm

Tỉ lệ/ Scale: 1/100 Ngày: 04/2025

Số bản vẽ: P2-204 No:

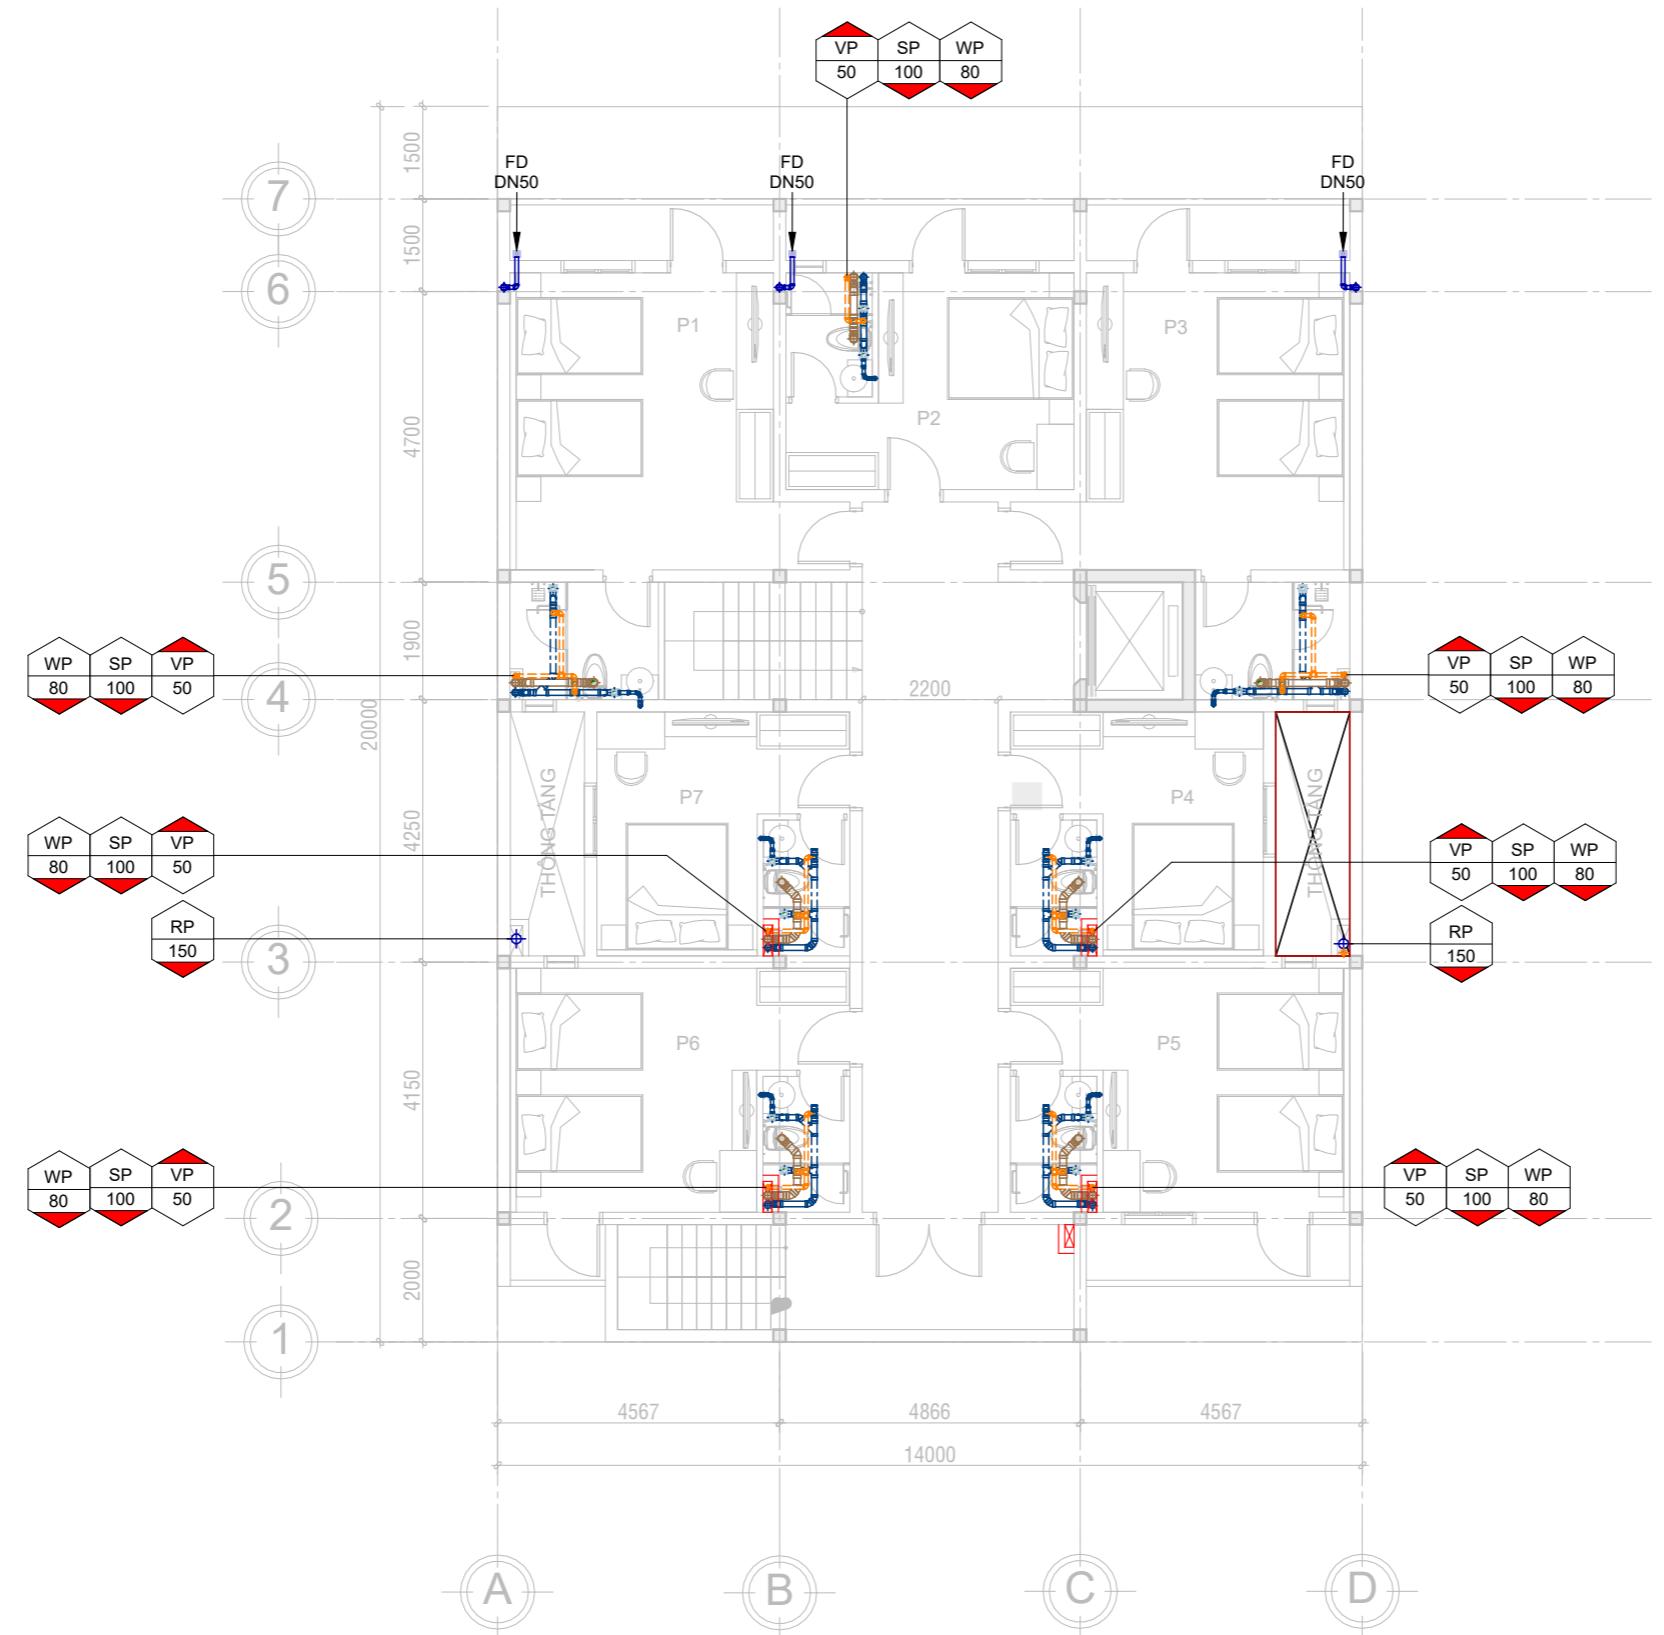

MẶT BẰNG TẦNG ĐIỂN HÌNH 2-6

TL:1/100

Mục đích phát hành/Release status:
Thiết kế sơ/Preliminary:
Bản vẽ trình duyệt/For approval:
Bản vẽ tham khảo/For reference:
Bản vẽ thi công/For construction:
Bản vẽ hiệu chỉnh/Revising:
Bản vẽ hoàn công/As built:

Đơn vị thiết kế - Thi công:

**CÔNG TY
CỔ PHẦN KIẾN TRÚC
- XÂY DỰNG ĐỨC AN**

Địa chỉ:
60/10/2 Lâm Văn Bền - Phường
Tân Kiểng - Quận 7 - TP.HCM

Công trình/ Project:

BINH DUONG HOTEL

Hạng mục/ Item:

**THIẾT KẾ
ĐIỆN NƯỚC**

Bản vẽ/ Drawing name:

**HỆ THỐNG THOÁT
NƯỚC-SÂN THƯỢNG**

Chủ trì thiết kế/ Project manager:


KTS. Vũ Minh Lâm

Thiết kế/ Desginer:

KTS. Vũ Minh Lâm

Tỉ lệ/ Scale: 1/100 Ngày: 04/2025

Số bản vẽ: P2-205 No:

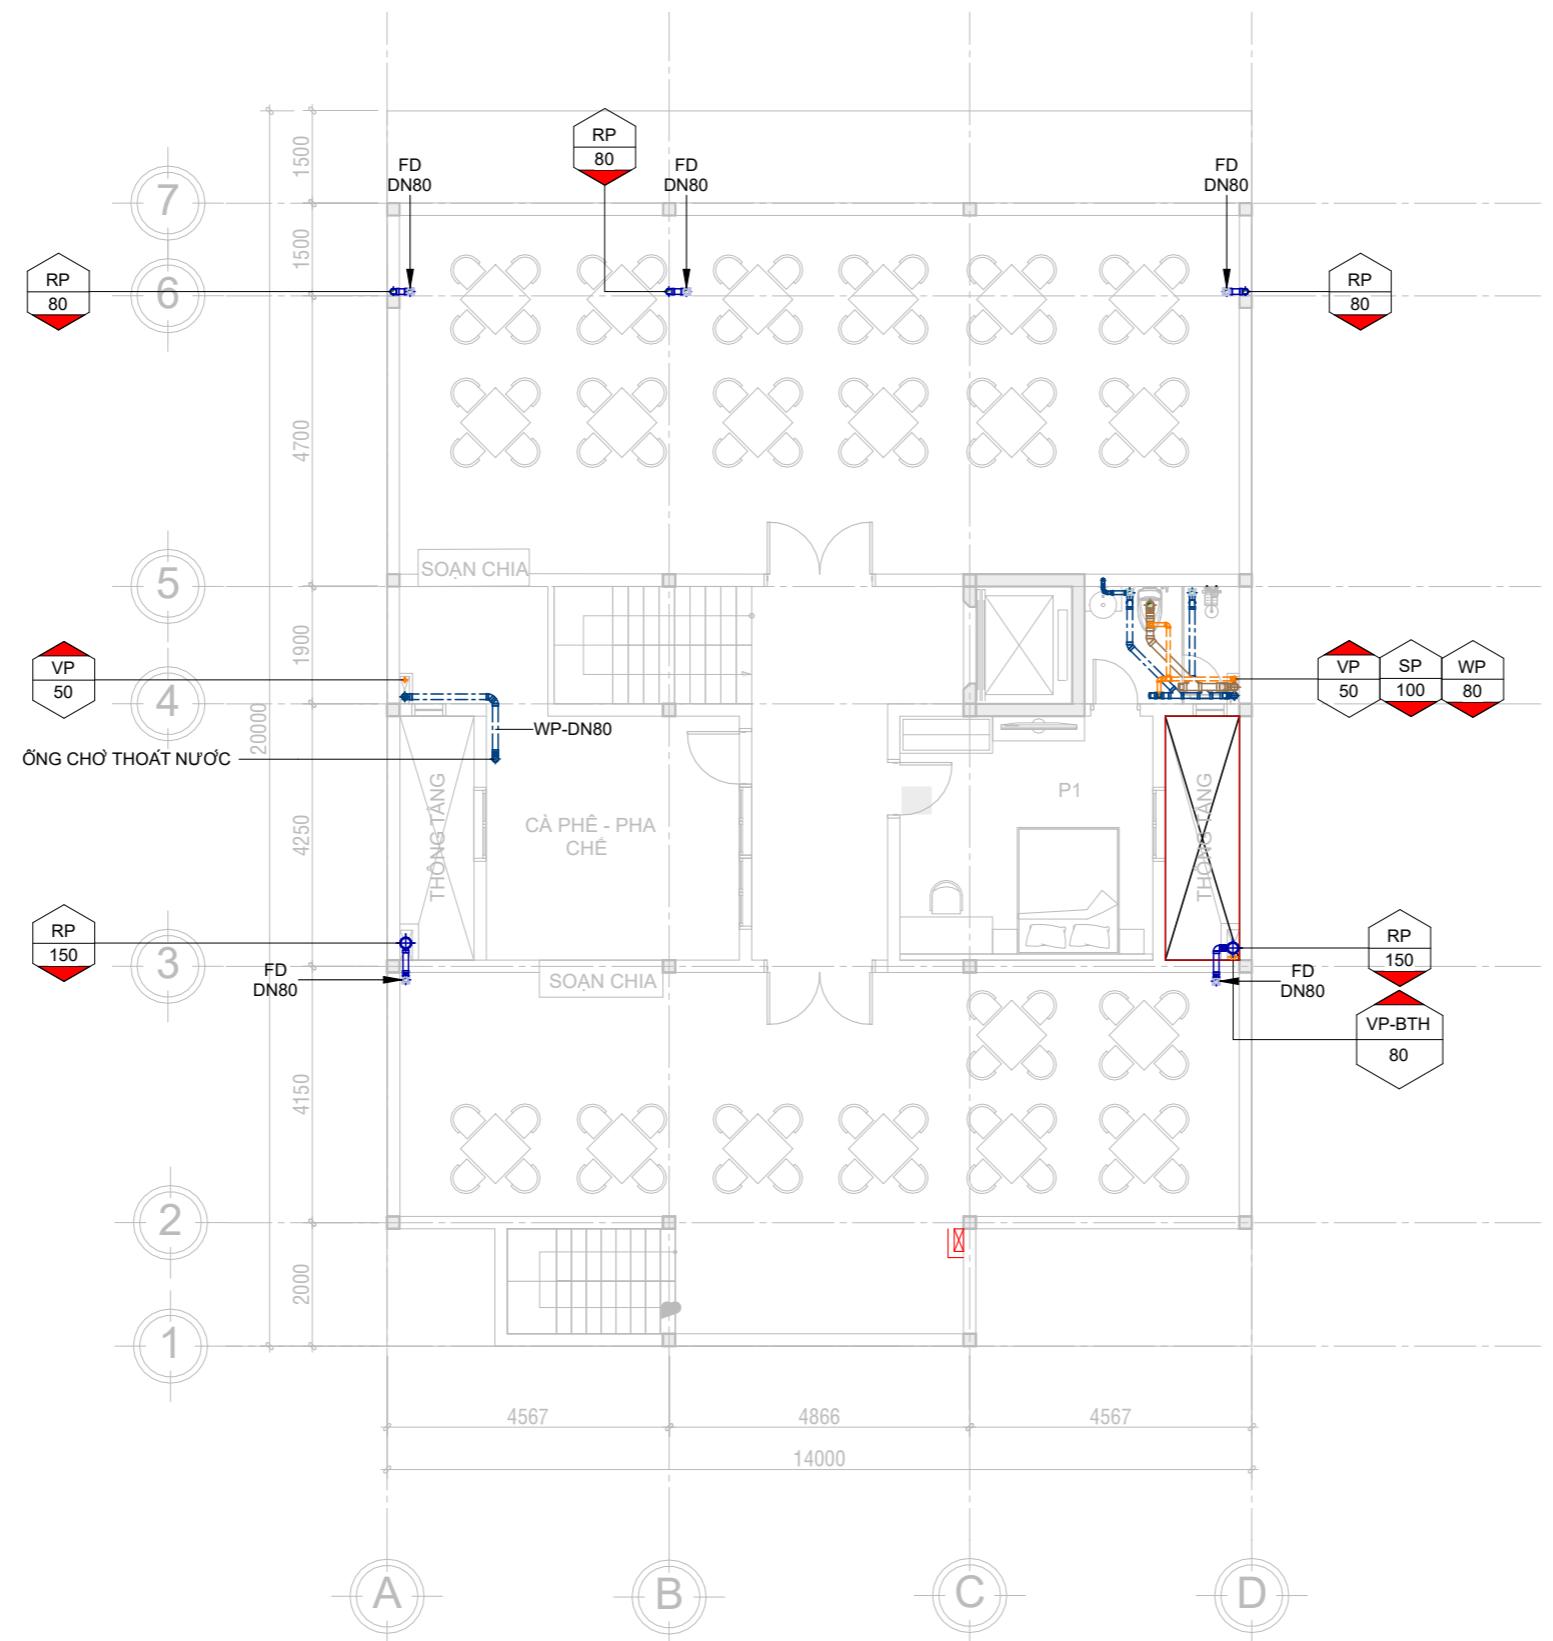

MẶT BẰNG TẦNG SÂN THƯỢNG

TL:1/100

Mục đích phát hành/Release status:	
Thiết kế sơ/Preliminary:	
Bản vẽ trình duyệt/For approval:	
Bản vẽ tham khảo/For reference:	
Bản vẽ thi công/For construction:	<input checked="" type="checkbox"/>
Bản vẽ hiệu chỉnh/Revising:	
Bản vẽ hoàn công/As built:	

Đơn vị thiết kế - Thi công:

**CÔNG TY
CỔ PHẦN KIẾN TRÚC
- XÂY DỰNG ĐỨC AN**

Địa chỉ:
60/10/2 Lâm Văn Bền - Phường
Tân Kiểng - Quận 7 - TP.HCM

Công trình/ Project:

BINH DUONG HOTEL

Hạng mục/ Item:

**THIẾT KẾ
ĐIỆN NƯỚC**

Bản vẽ/ Drawing name:

**HỆ THỐNG THOÁT
NƯỚC-MÁI**

Chủ trì thiết kế/ Project manager:


KTS. Vũ Minh Lâm

Thiết kế/ Desginer:

KTS. Vũ Minh Lâm

Tỉ lệ/ Scale: 1/100 Ngày: 04/2025


Số bản vẽ: P2-206 №:

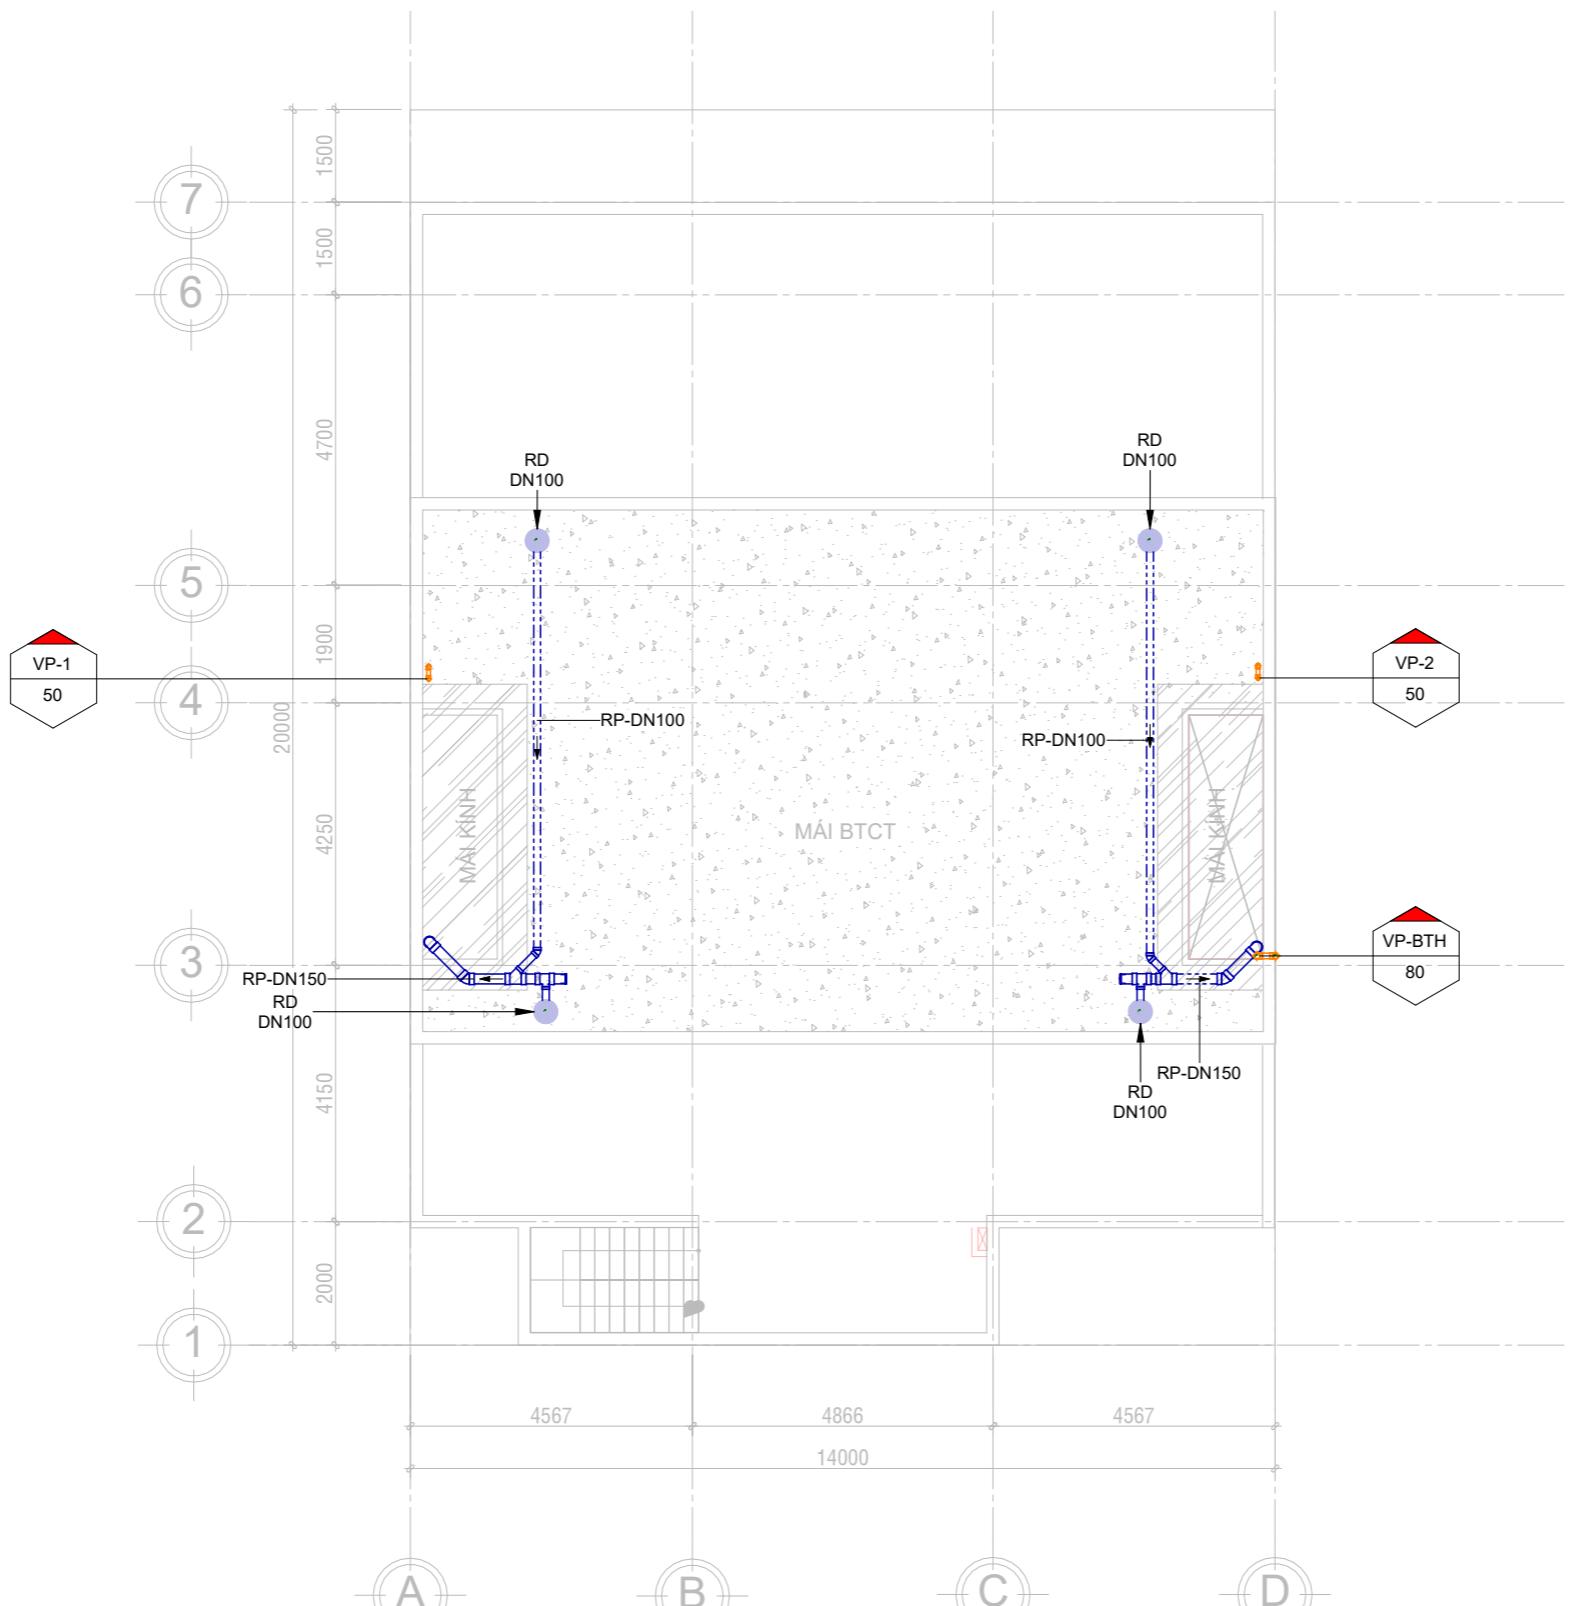

MẶT BẰNG MÁI

TL:1/100

Mục đích phát hành/Release status:
Thiết kế sơ/Preliminary:
Bản vẽ trình duyệt/For approval:
Bản vẽ tham khảo/For reference:
Bản vẽ thi công/For construction:
Bản vẽ hiệu chỉnh/Revising:
Bản vẽ hoàn công/As built:

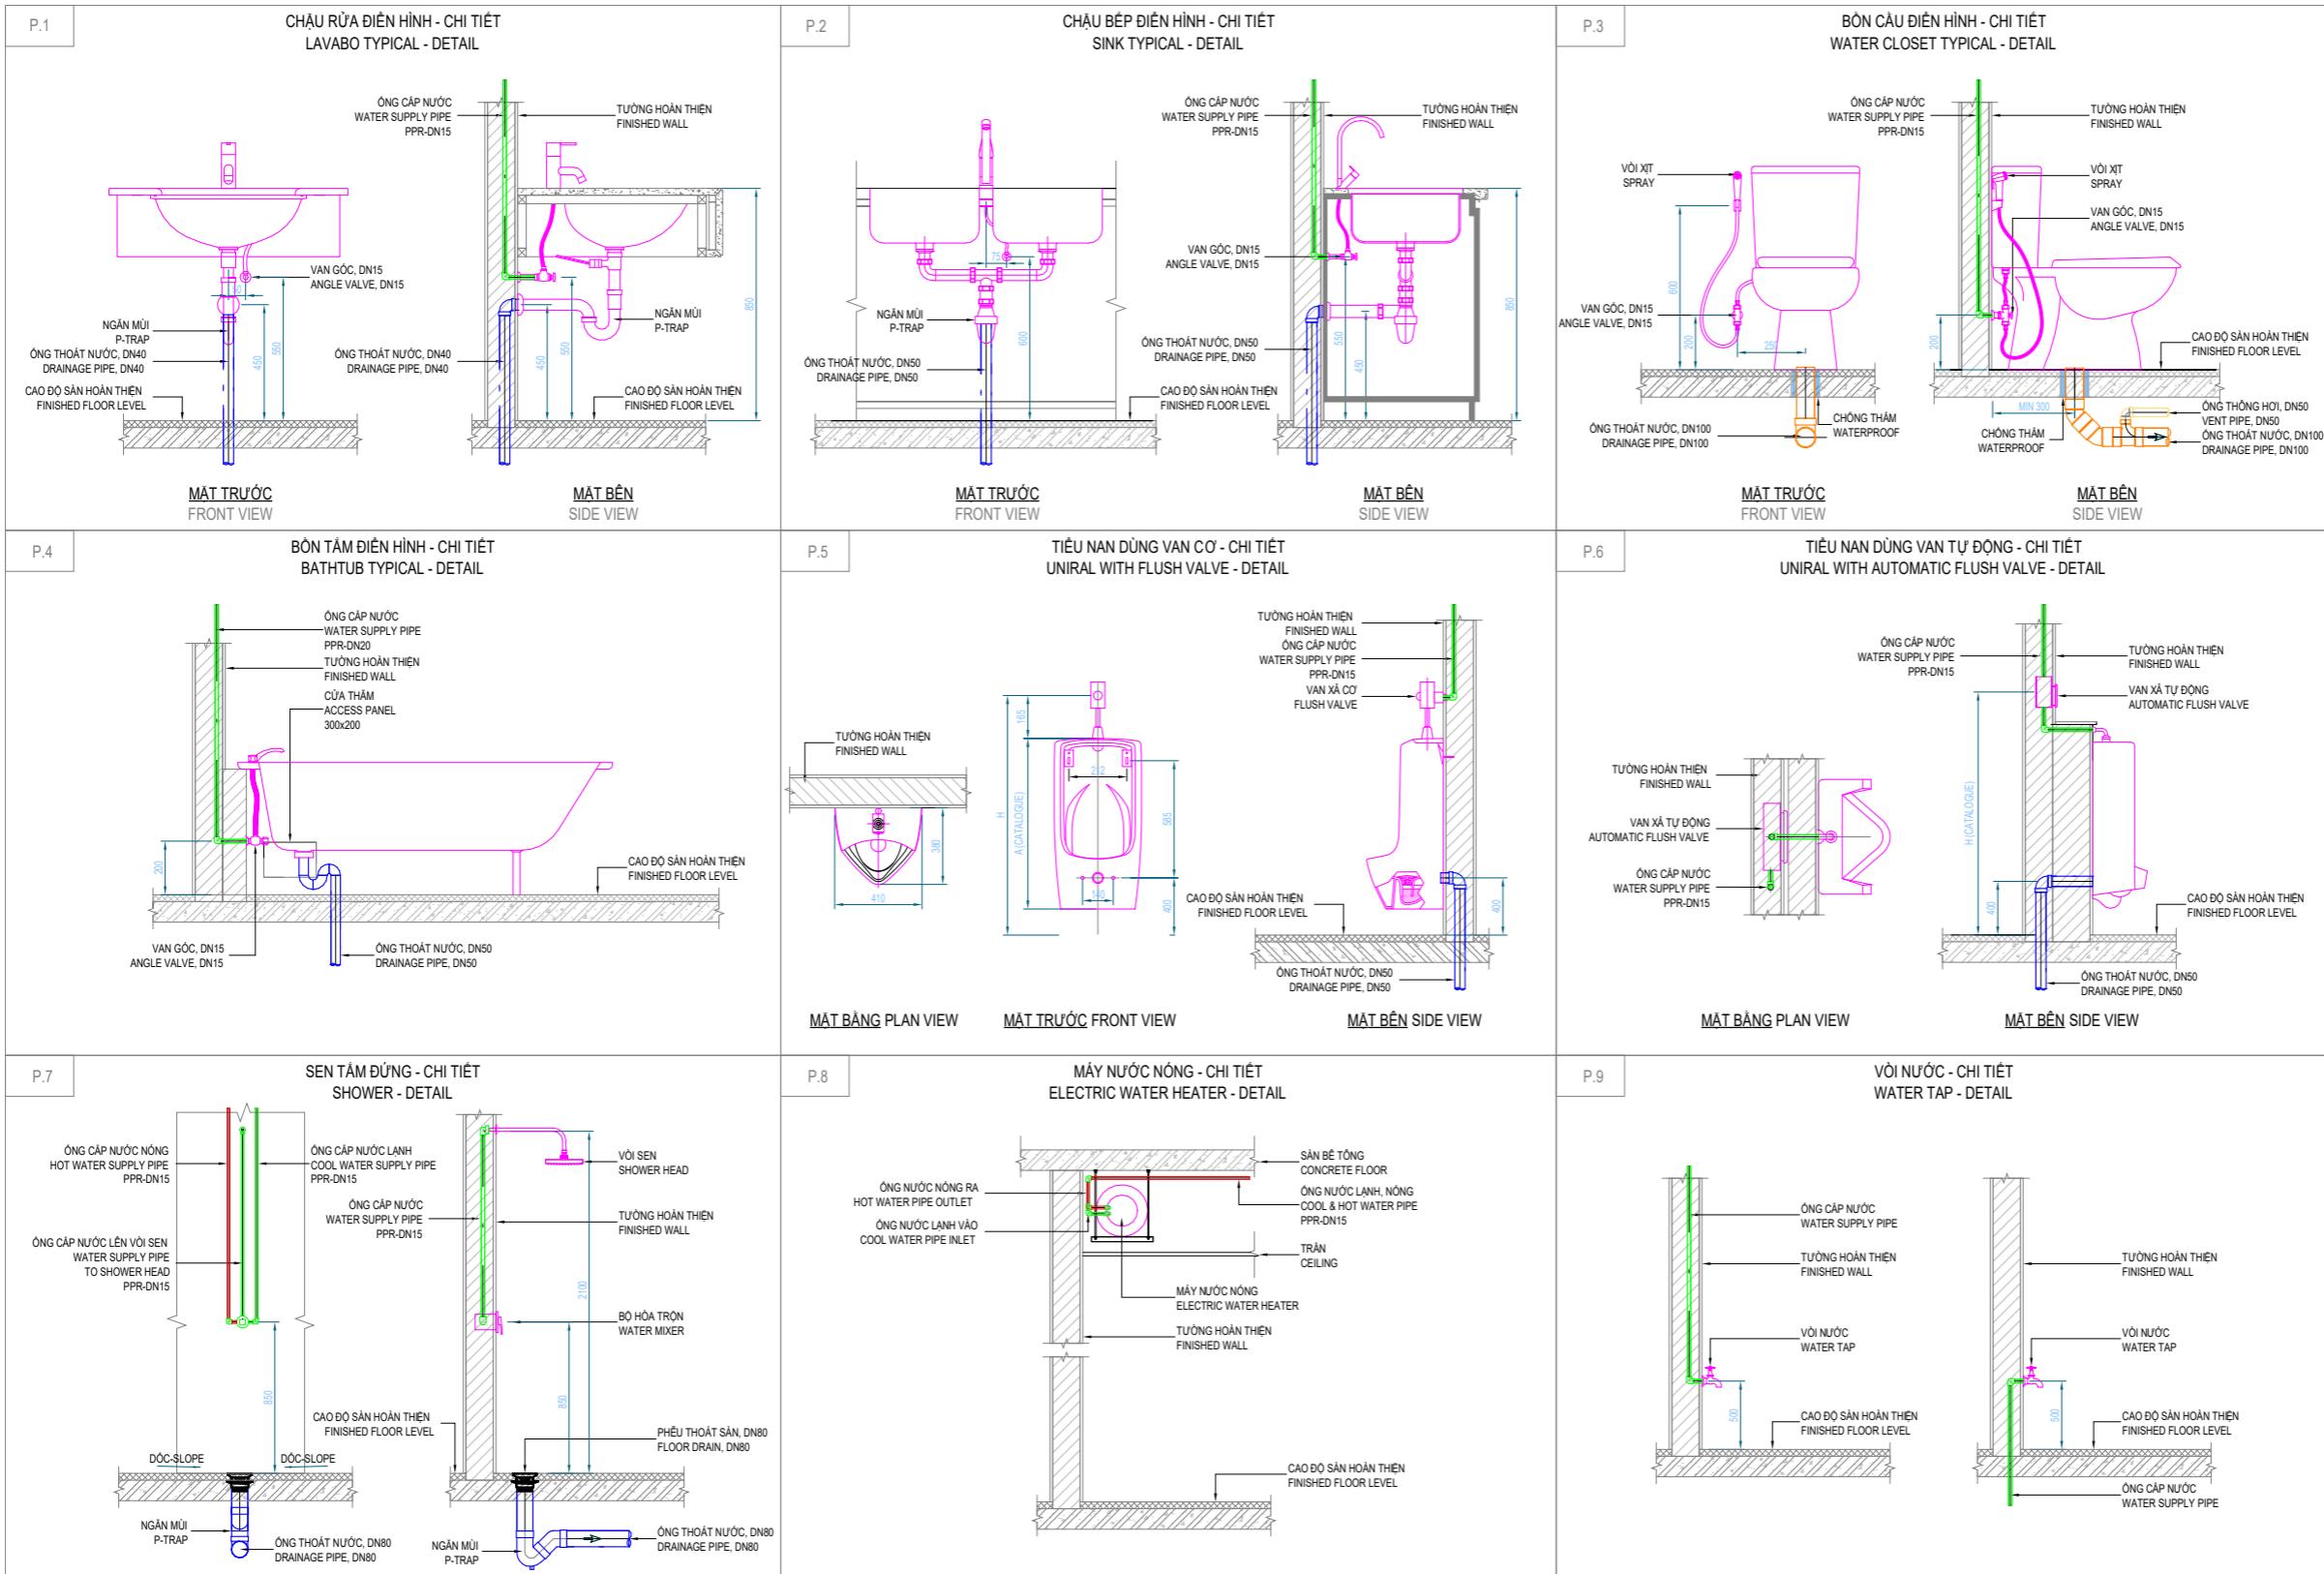

Đơn vị thiết kế - Thi công:
**CÔNG TY
CỔ PHẦN KIẾN TRÚC
- XÂY DỰNG ĐỨC AN**

Địa chỉ:
60/10/2 Lâm Văn Bền - Phường
Tân Kiểng - Quận 7 - TP.HCM

Công trình/ Project:

BINH DUONG HOTEL

Hạng mục/ Item:

**THIẾT KẾ
ĐIỆN NƯỚC**

Bản vẽ/ Drawing name:

**CHI TIẾP LẮP ĐẶT CTN
1**

Chủ trì thiết kế/ Project manager:

KTS. Vũ Minh Lâm

Thiết kế/ Desginer:


KTS. Vũ Minh Lâm

Tỉ lệ/ Scale: 1/100 Ngày: 04/2025

Số bản vẽ: P3-401

No:

Mục đích phát hành/Release status:
Thiết kế sơ/Preliminary:
Bản vẽ trình duyệt/For approval:
Bản vẽ tham khảo/For reference:
Bản vẽ thi công/For construction:
Bản vẽ hiệu chỉnh/Revising:
Bản vẽ hoàn công/As built:

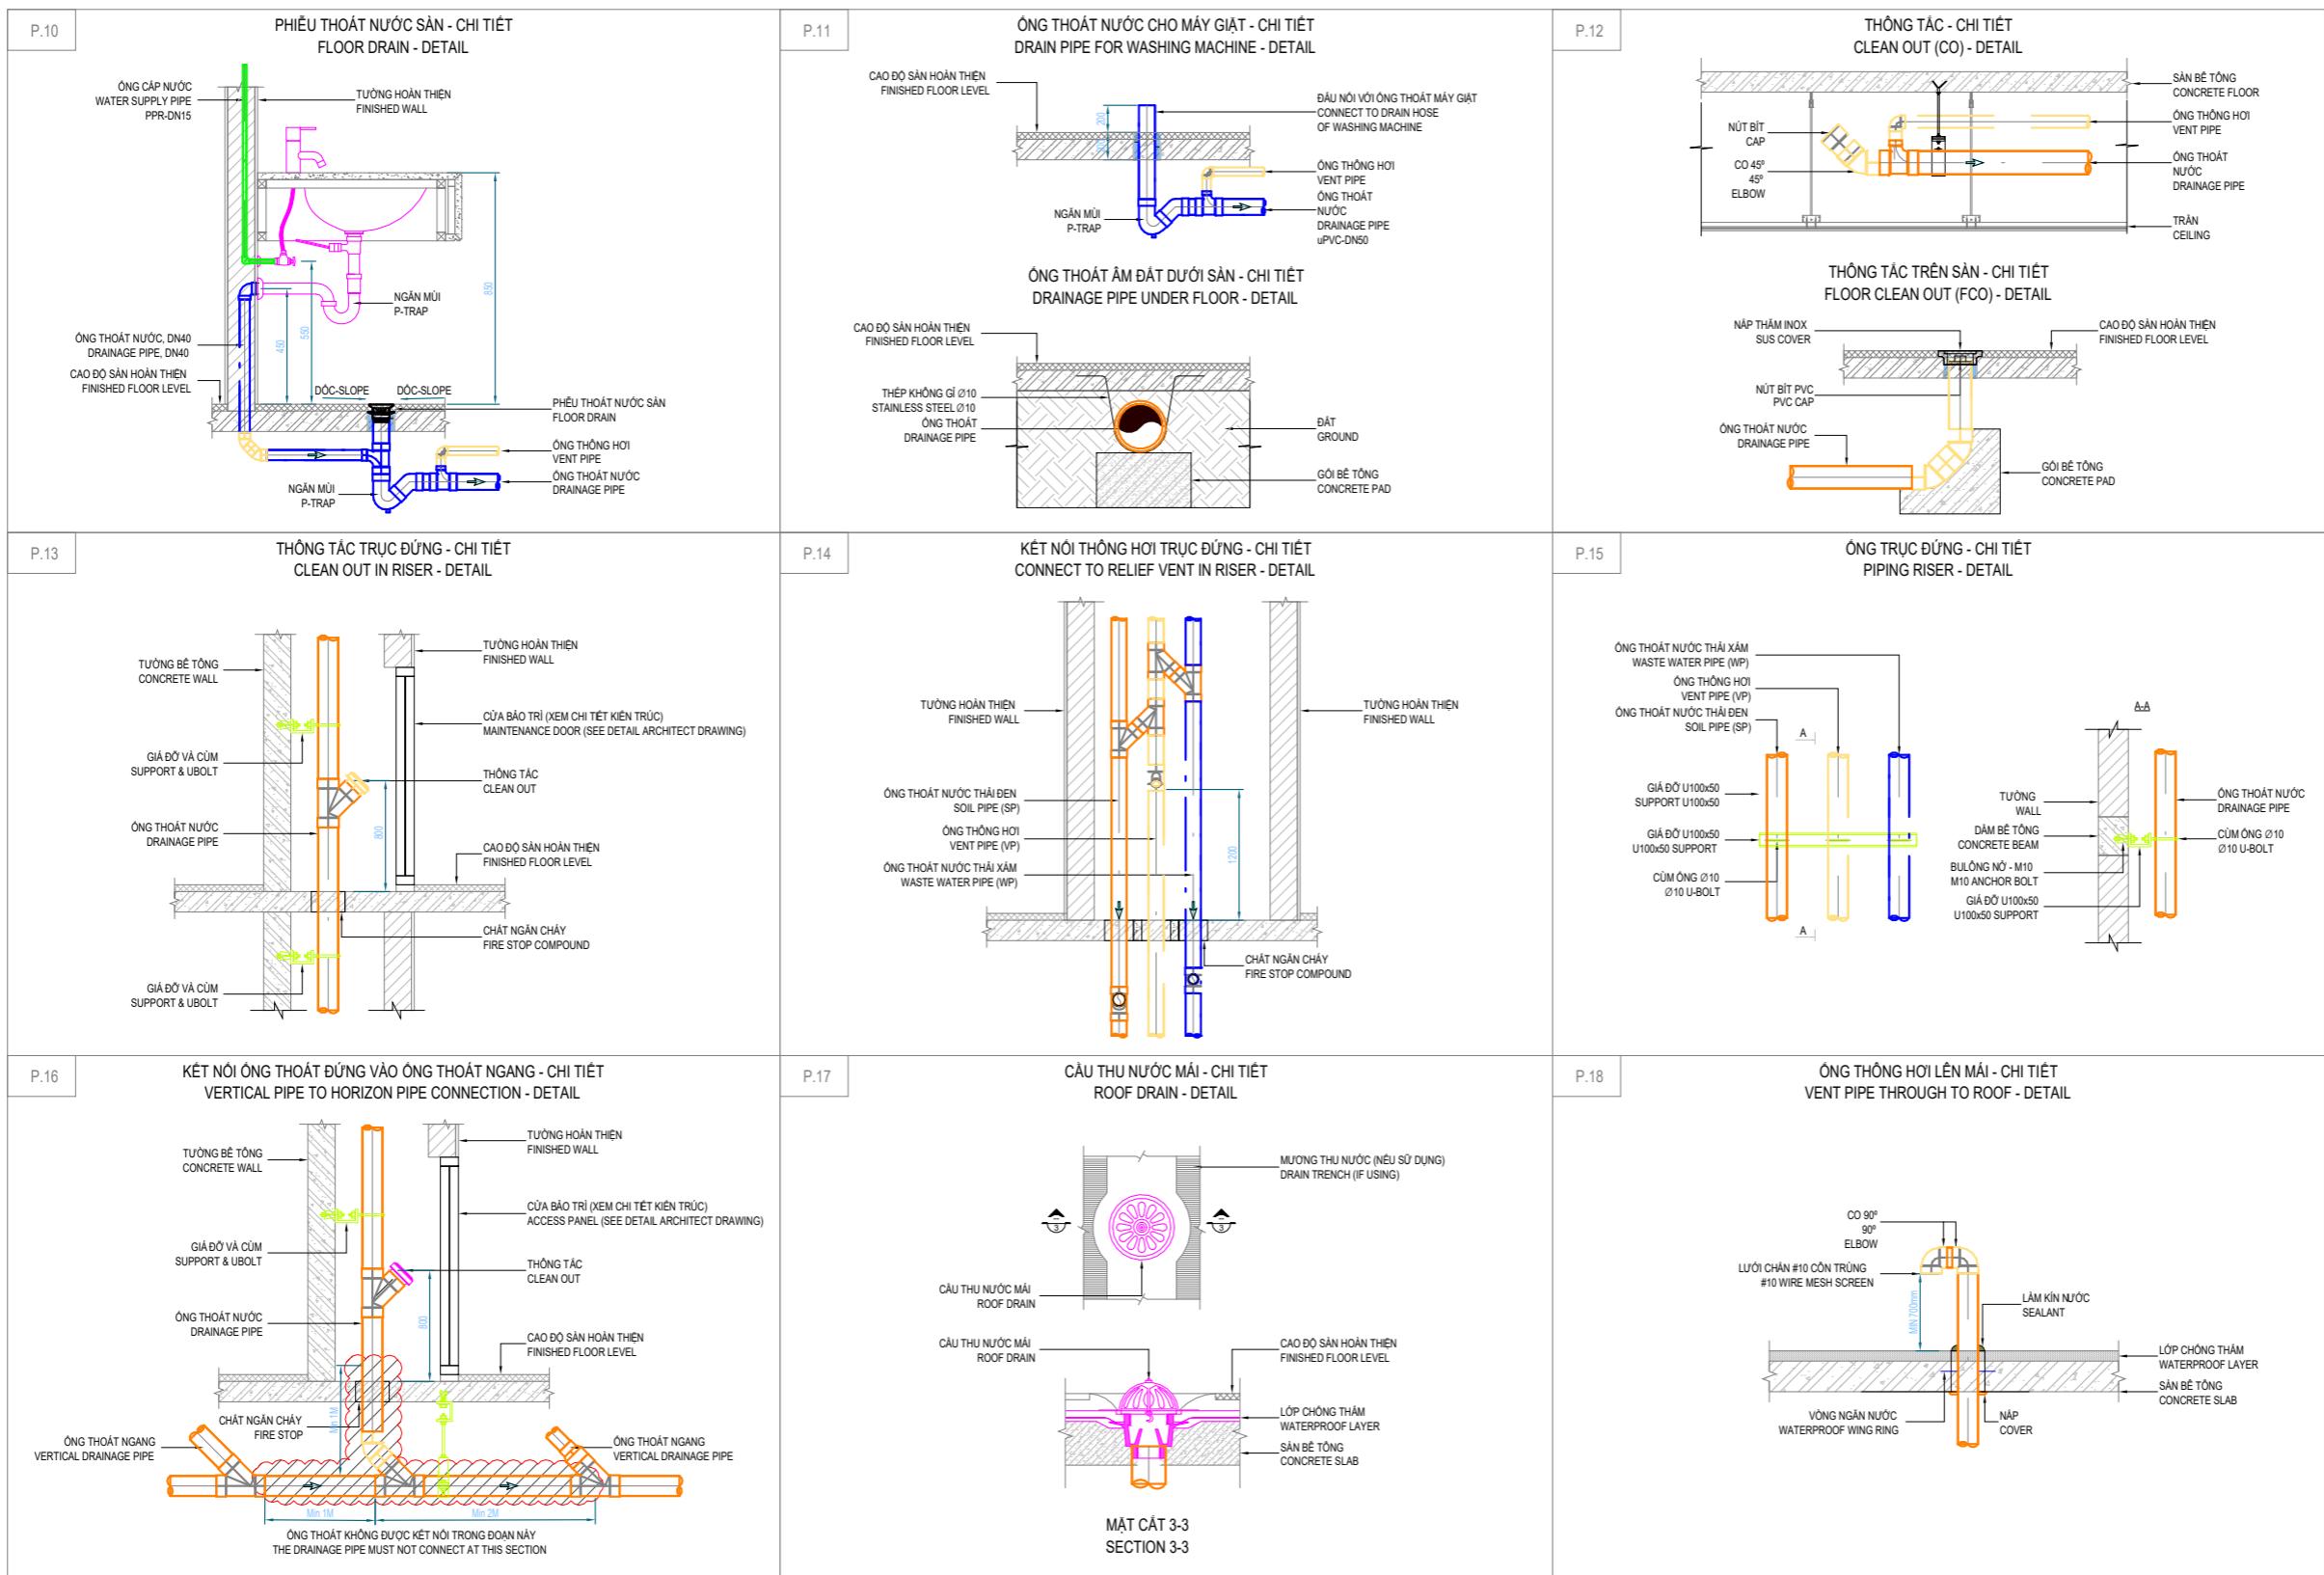

Đơn vị thiết kế - Thi công:

CÔNG TY
CỔ PHẦN KIẾN TRÚC
- XÂY DỰNG ĐỨC AN

Địa chỉ:

60/10/2 Lâm Văn Bền - Phường
Tân Kiểng - Quận 7 - TP.HCM

Công trình/ Project:

BINH DUONG HOTEL

Hạng mục/ Item:

THIẾT KẾ
ĐIỆN NƯỚC

Bản vẽ/ Drawing name:

CHI TIẾT LẮP ĐẶT CTN
2

Chủ trì thiết kế/ Project manager:

KTS. Vũ Minh Lâm

Thiết kế/ Desginer:

KTS. Vũ Minh Lâm

Tỉ lệ/ Scale: 1/100 Ngày: 04/2025

Số bản vẽ: P3-402

No: